

LIIT ARQUITECTURA

LIIT

Provenza, Bucaramanga

Apartamento CORPAR

CONTENIDO:

-PLANO DE COTAS - PUERTASY VENTANAS

PROYECTO:

LIIT ARQUITECTURA

FECHA:

18/05/2023


ESCALA:

1:50

PLANO Nº:

4/11

PLANO DE COTAS - PUERTASY VENTANAS

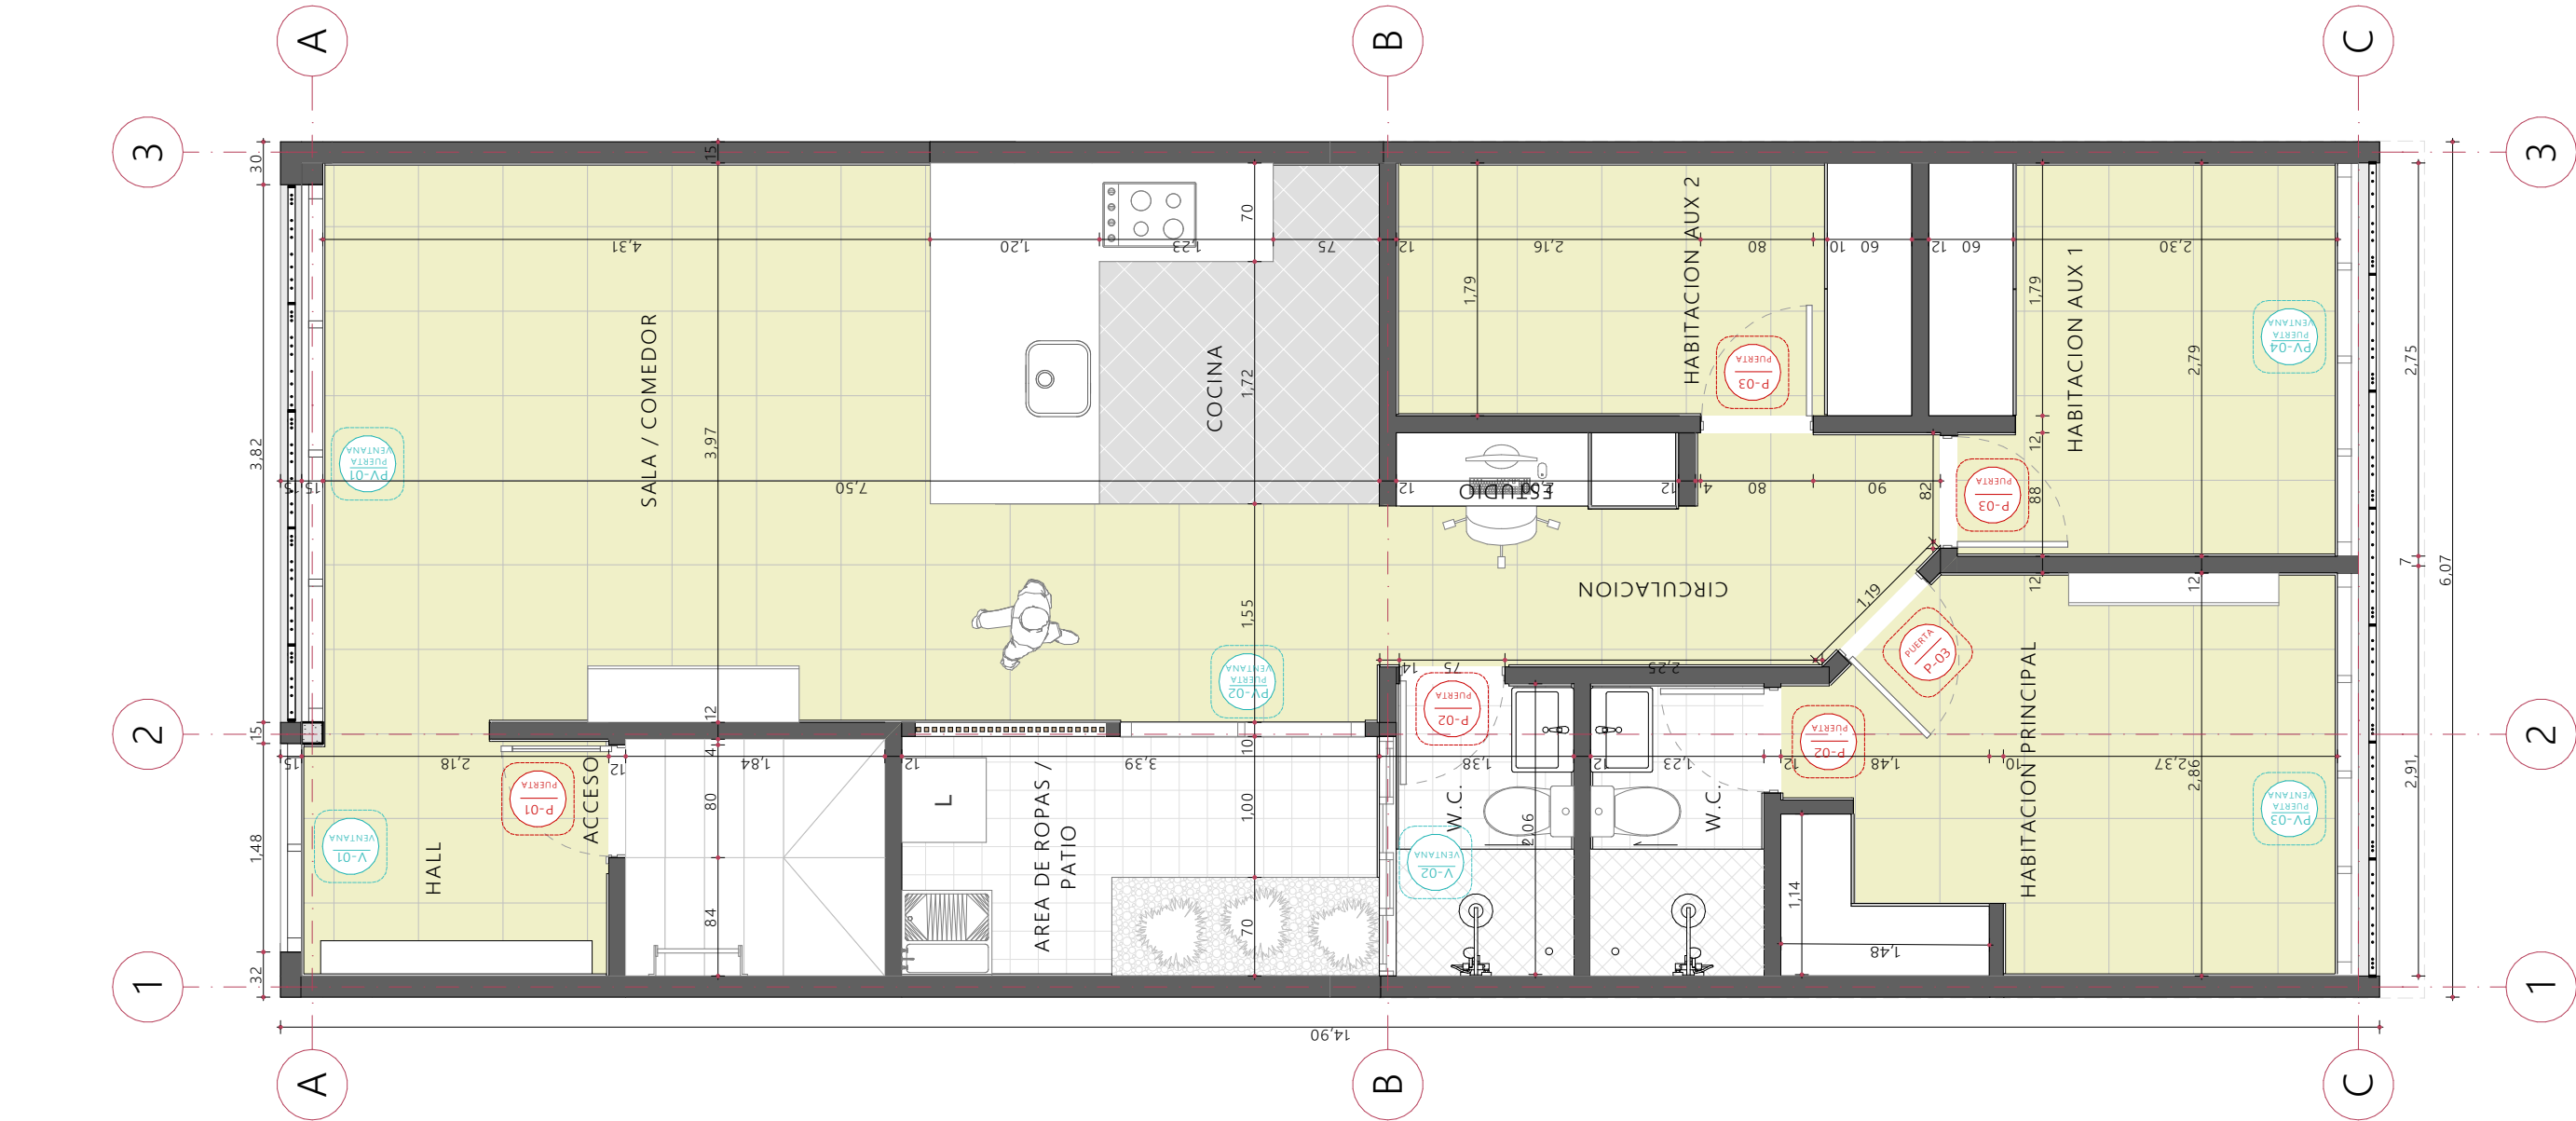

| CUADRO DE ÁREAS            |          |                       |         |
|----------------------------|----------|-----------------------|---------|
| HALL / CIRCULACION         | 20.41 M2 | ESTUDIO               | 1.5 M2  |
| SALA / COMEDOR             | 11 M2    | HABITACION PRINCIPAL  | 11.2 M2 |
| COCINA                     | 7.8 M2   | HABITACION AUXILIAR 1 | 8.3 M2  |
| PATIO                      | 5.8 M2   | HABITACION AUXILIAR 2 | 6.6 M2  |
| AREA TOTAL DE INTERVENCION |          | 82 M2                 |         |

| VENTANAS |                        |          |                  |               |
|----------|------------------------|----------|------------------|---------------|
| Tipo     | Medidas                | Cantidad | Altura Antepecho | Altura Dintel |
| V-01     | 1.30 alto x 1.50 ancho | 1        | 1.0 m            | 0.10 m        |
| V-02     | 0.40 alto x 1.70 ancho | 1        | 2.10 m           | 0.0 m         |

| PUERTAS |                        |          |                 |               |
|---------|------------------------|----------|-----------------|---------------|
| Tipo    | Medidas                | Cantidad | Ubicación       | Altura Dintel |
| P-01    | 2.10 alto x 0.80 ancho | 1        | Acceso / Diseño | 0.40 m        |
| P-02    | 2.10 alto x 0.75 ancho | 1        | Zonas Húmedas   | 0.40 m        |
| P-03    | 2.10 alto x 0.80 ancho | 1        | Habitaciones    | 0.40 m        |

| PUERTA - VENTANA |                        |          |                  |               |
|------------------|------------------------|----------|------------------|---------------|
| Tipo             | Medidas                | Cantidad | Altura Antepecho | Altura Dintel |
| PV-01            | 2.10 alto x 3.80 ancho | 1        | 0.20 m           | 0.20 m        |
| PV-02            | 2.10 alto x 1.75 ancho | 1        | 0.0 m            | 0.40 m        |
| PV-03            | 2.10 alto x 2.85 ancho | 1        | 0.20 m           | 0.20 m        |
| PV-04            | 2.10 alto x 2.80 ancho | 1        | 0.20 m           | 0.20 m        |