



PROYECTO DE VIVIENDA UNIFAMILIAR, VILLA GUADALQUIVIR, LOTE 4-12, FLORIDABLANCA

Plano de Sótano:

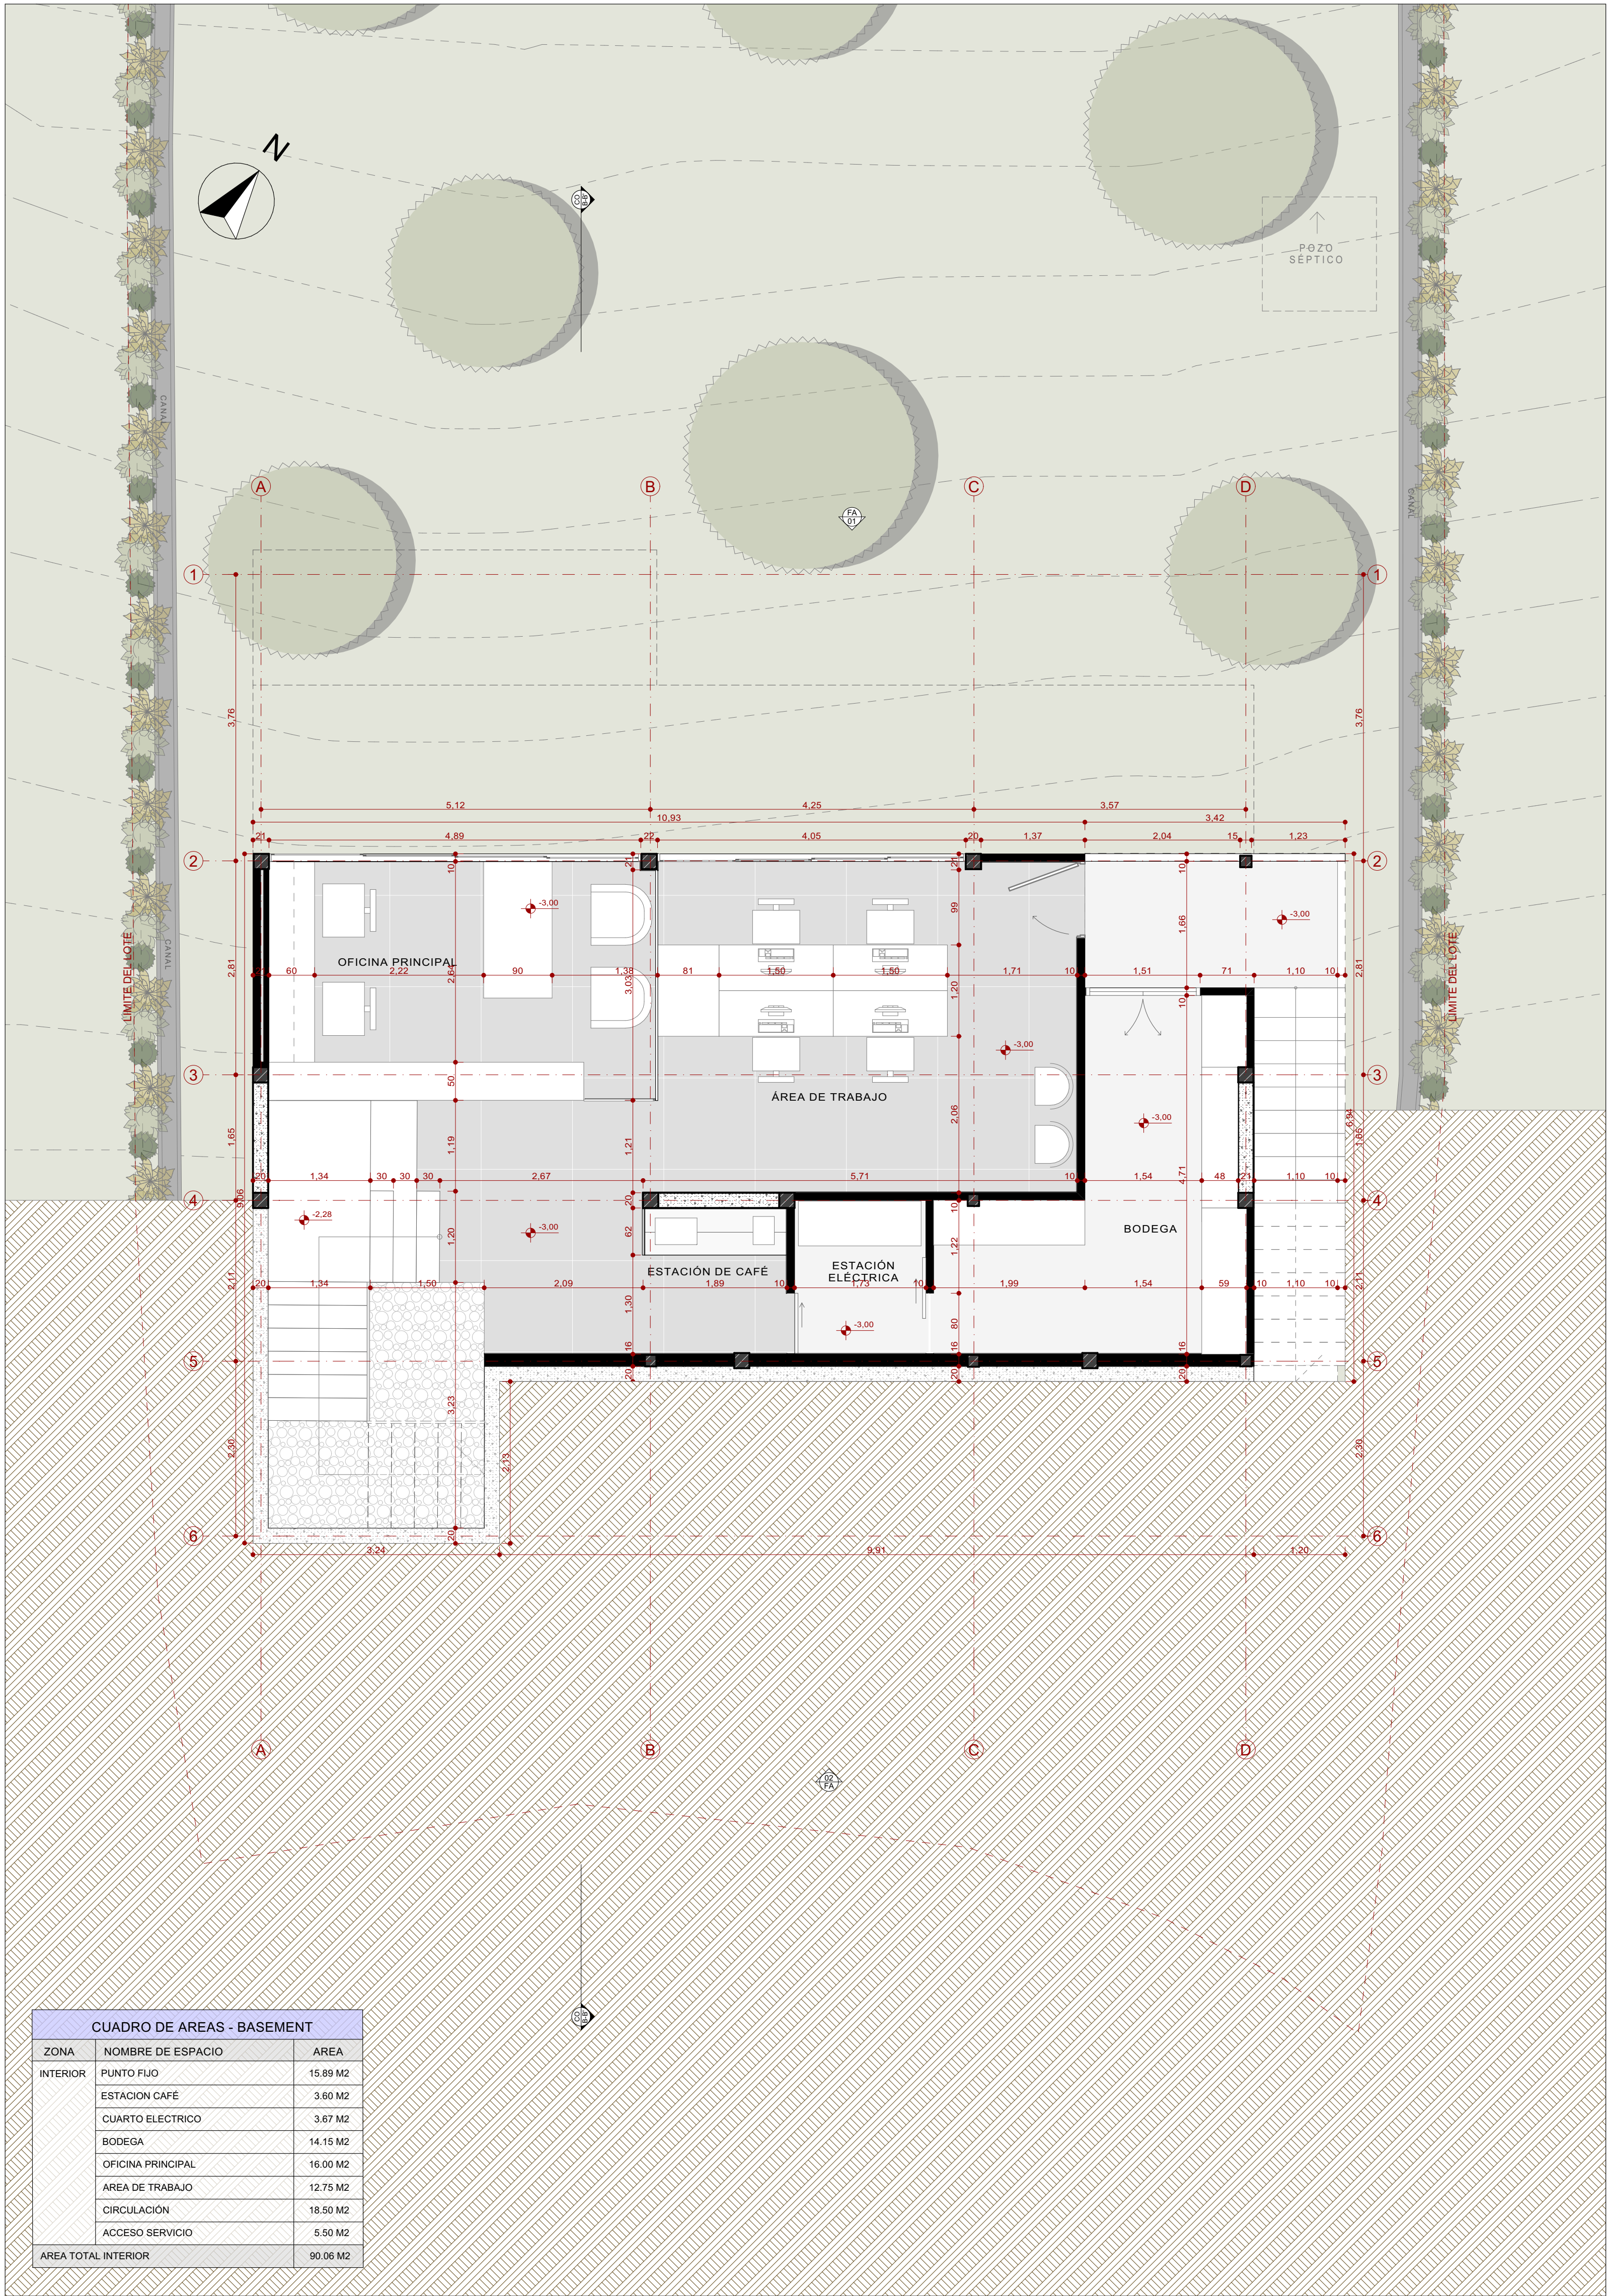

Plano de Primer Piso:

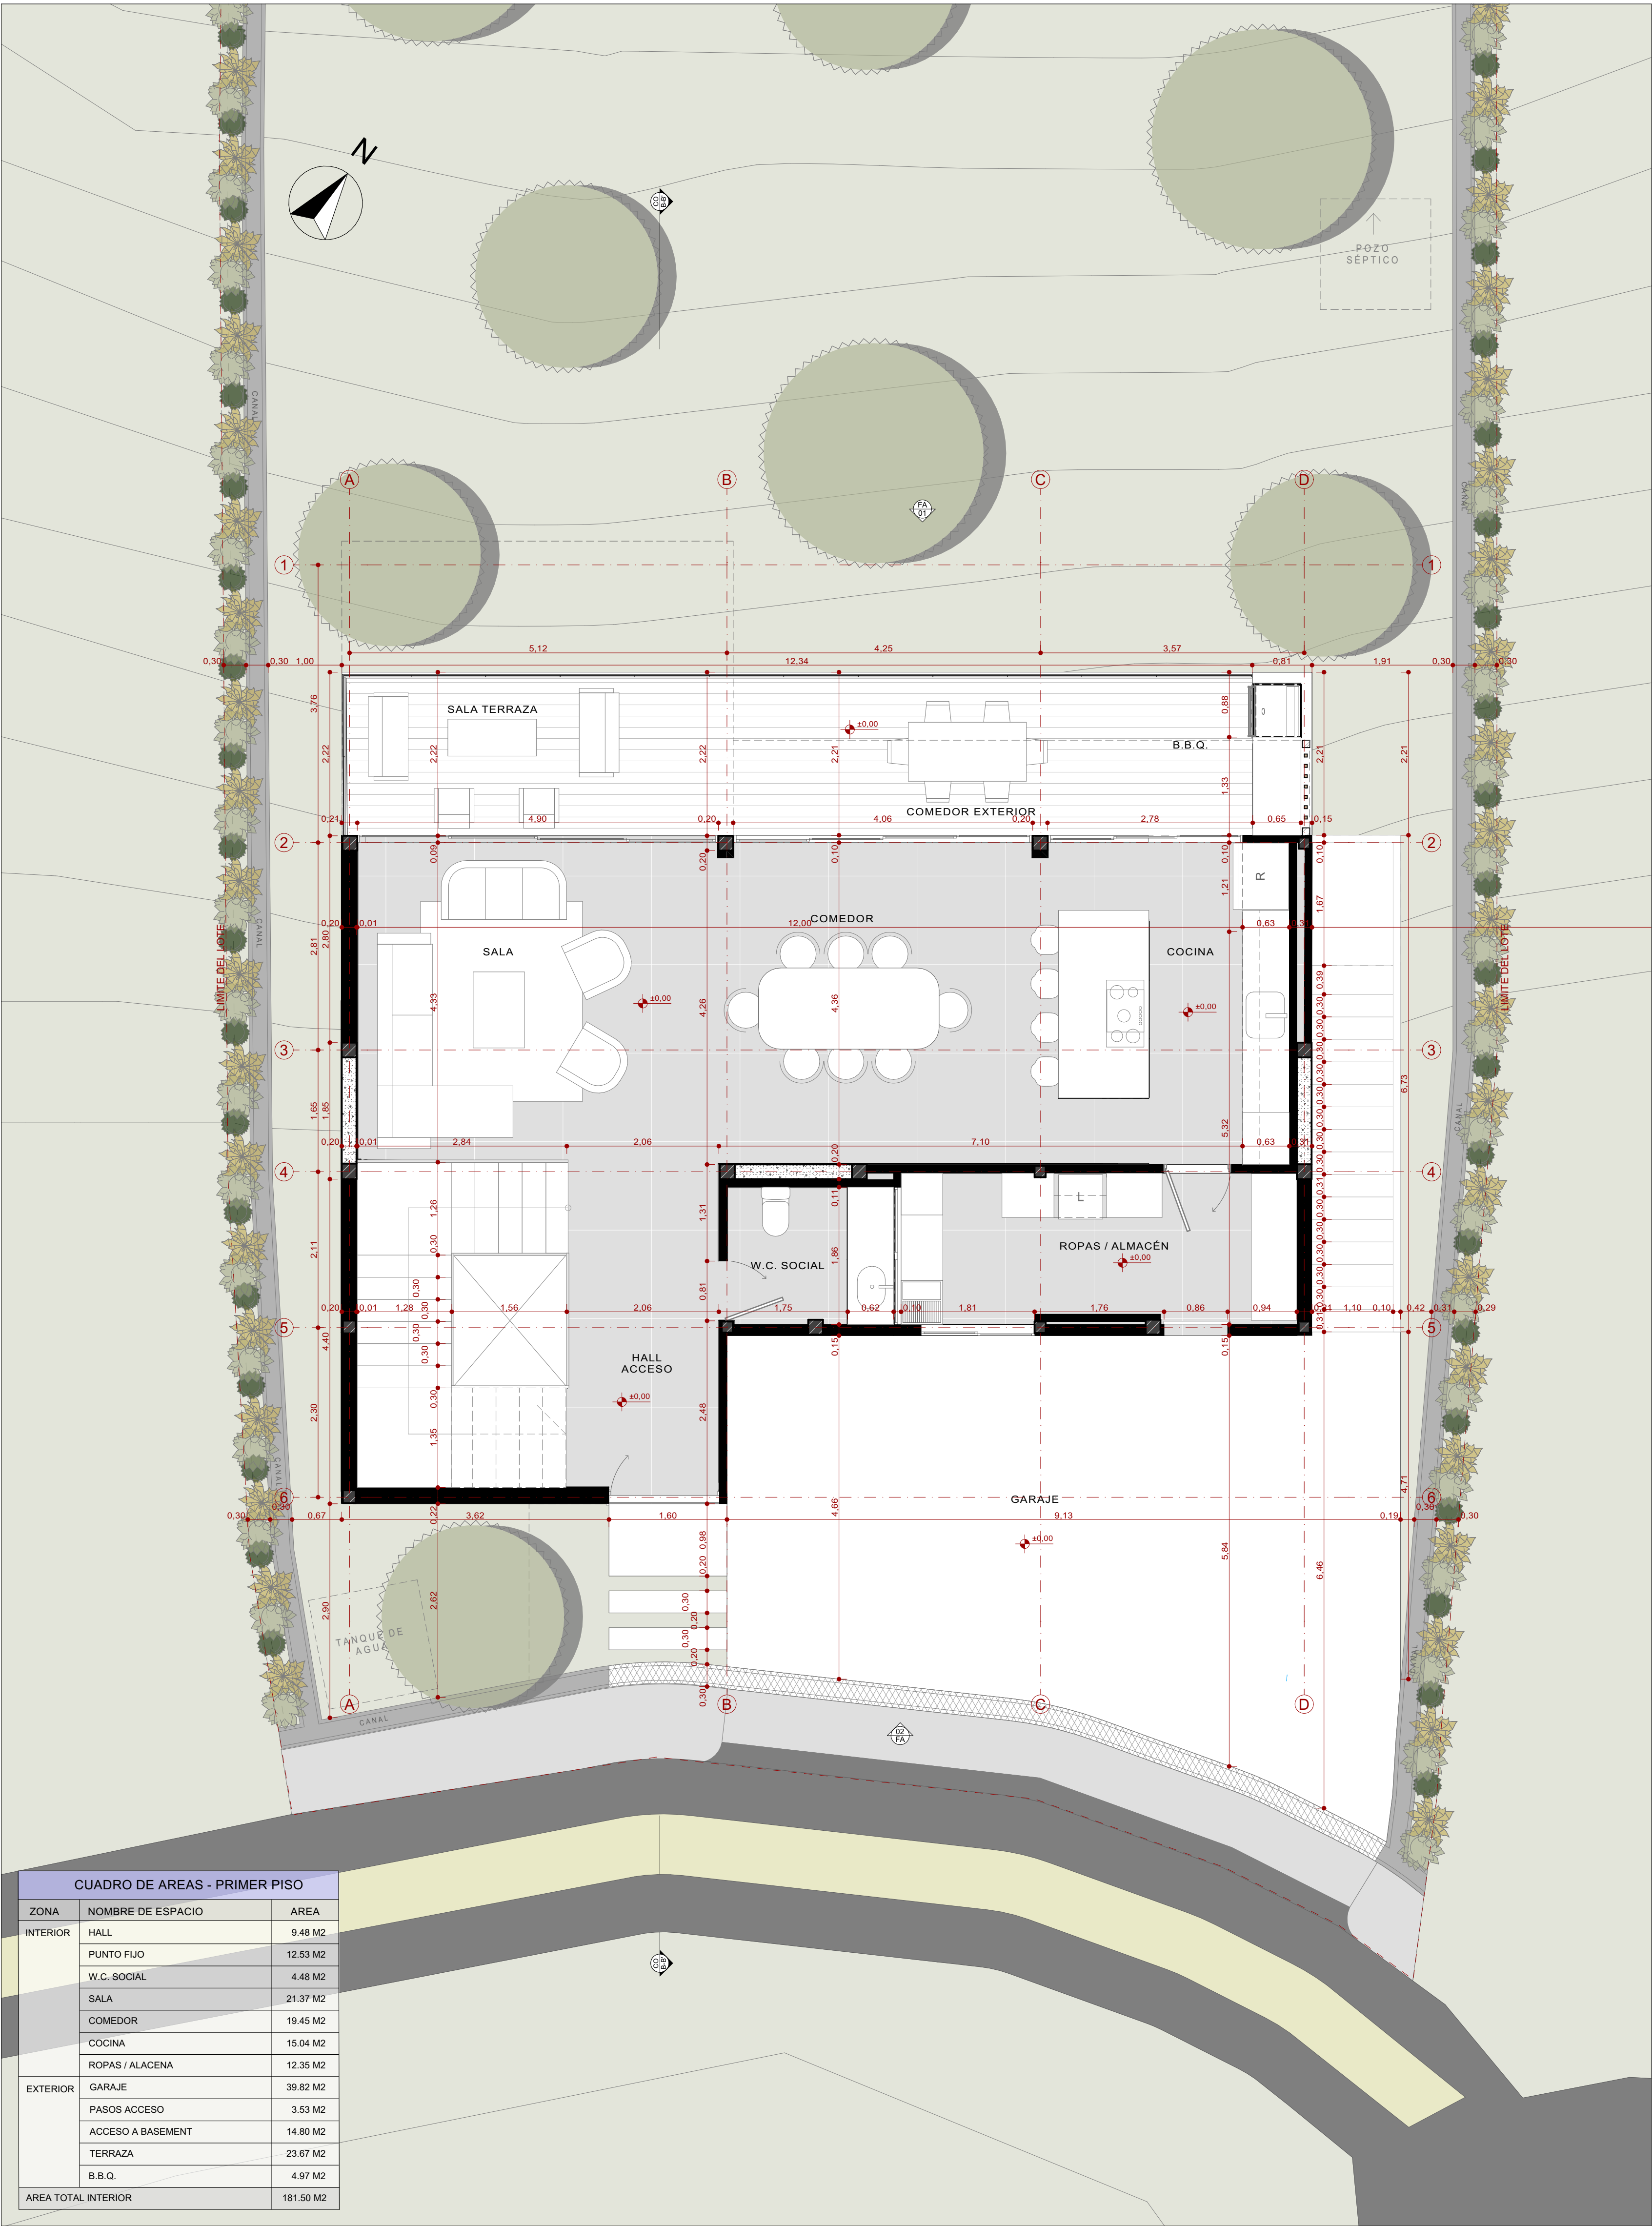

DIRECCION:
VILLA GUADALQUIVIR, LOTE 4-12,
FLORIDABLANCA

PROPIETARIOS

BRAYAN PÉREZ DELGADO
C.C. 1.098.810.706

DISEÑADOR

ARQ. JUAN SEBASTIAN BALAMANCA ARDILA
M.P. A36322019-1098742250
LIIT ARQUITECTURA

ACTUACION

PLANIMETRIAS ARQUITECTONICAS
PROYECTO DE VIVIENDA UNIFAMILIAR,
EN VILLA GUADALQUIVIR,
FLORIDABLANCA

CONTENIDO

- PLANO ARQUITECTONICO SÓTANO
- PLANO ARQUITECTONICO PRIMER PISO

NOTAS GENERALES

ESCALAS

1:50

28/11/2025

01-PLANO ARQUITECTONICO