



PROYECTO DE VIVIENDA UNIFAMILIAR, VILLA GUADALQUIVIR, LOTE 4-12, FLORIDABLANCA

Plano de Segundo Piso:

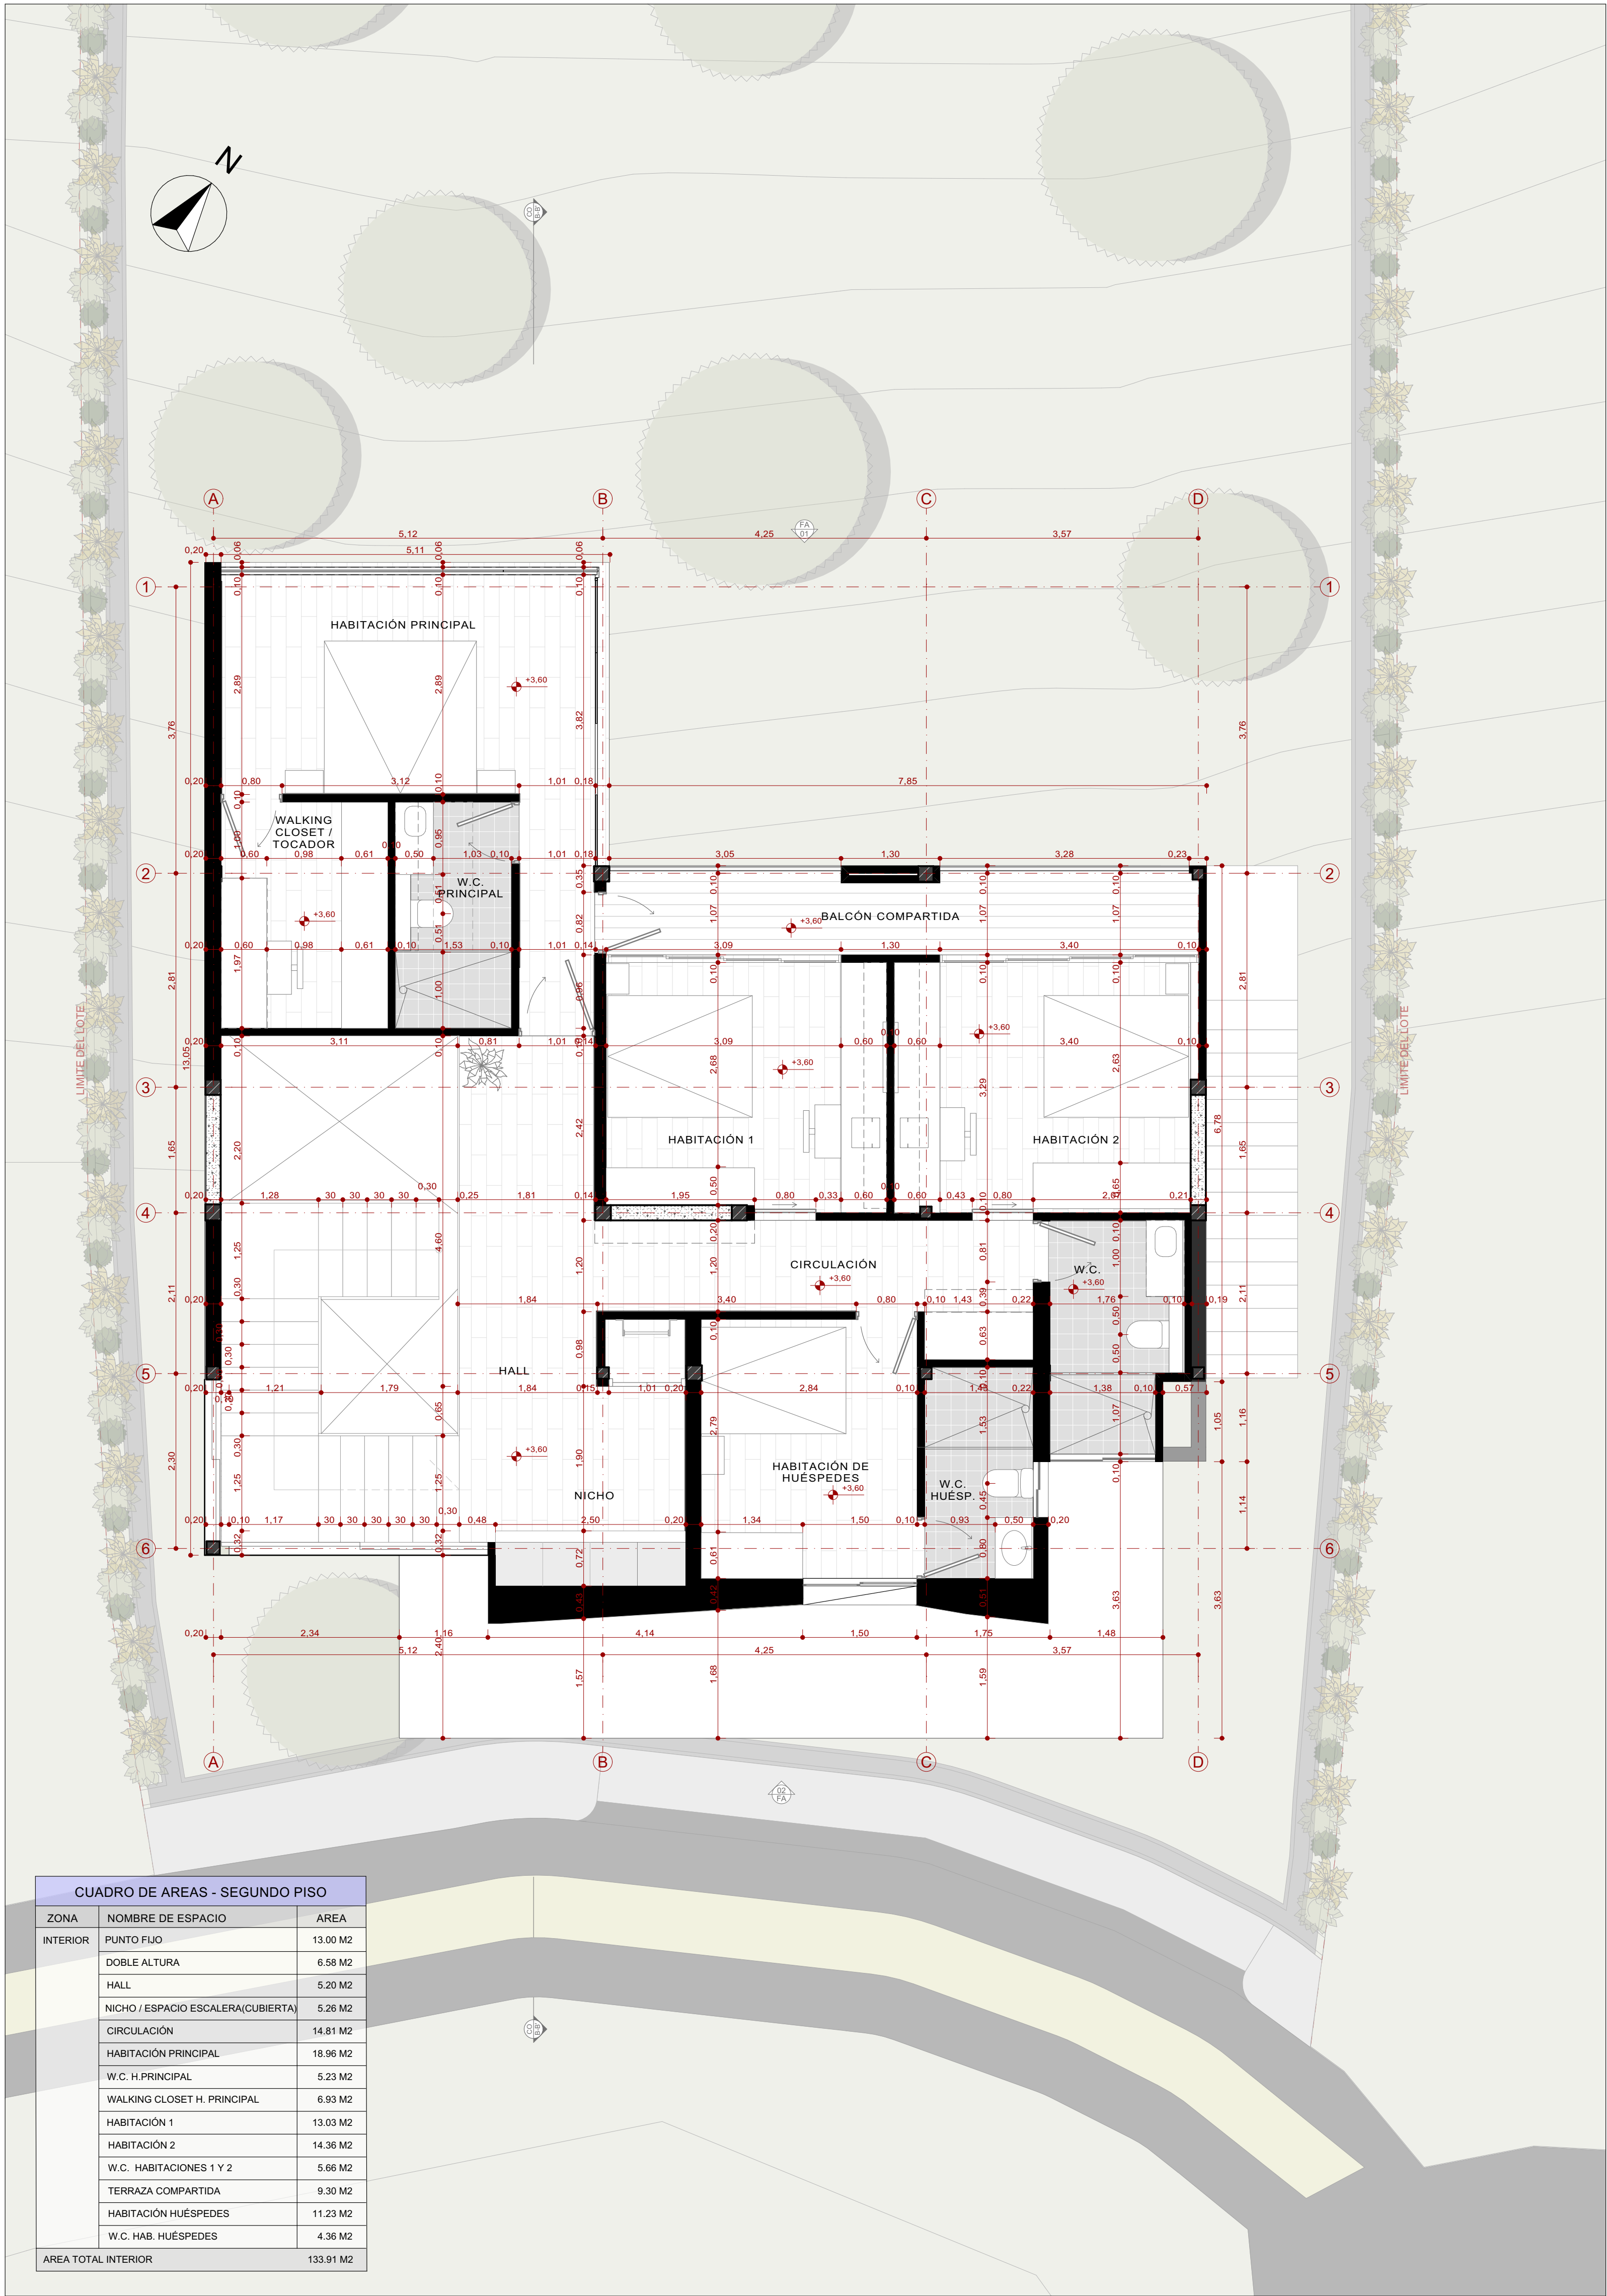

Plano de Cubiertas:

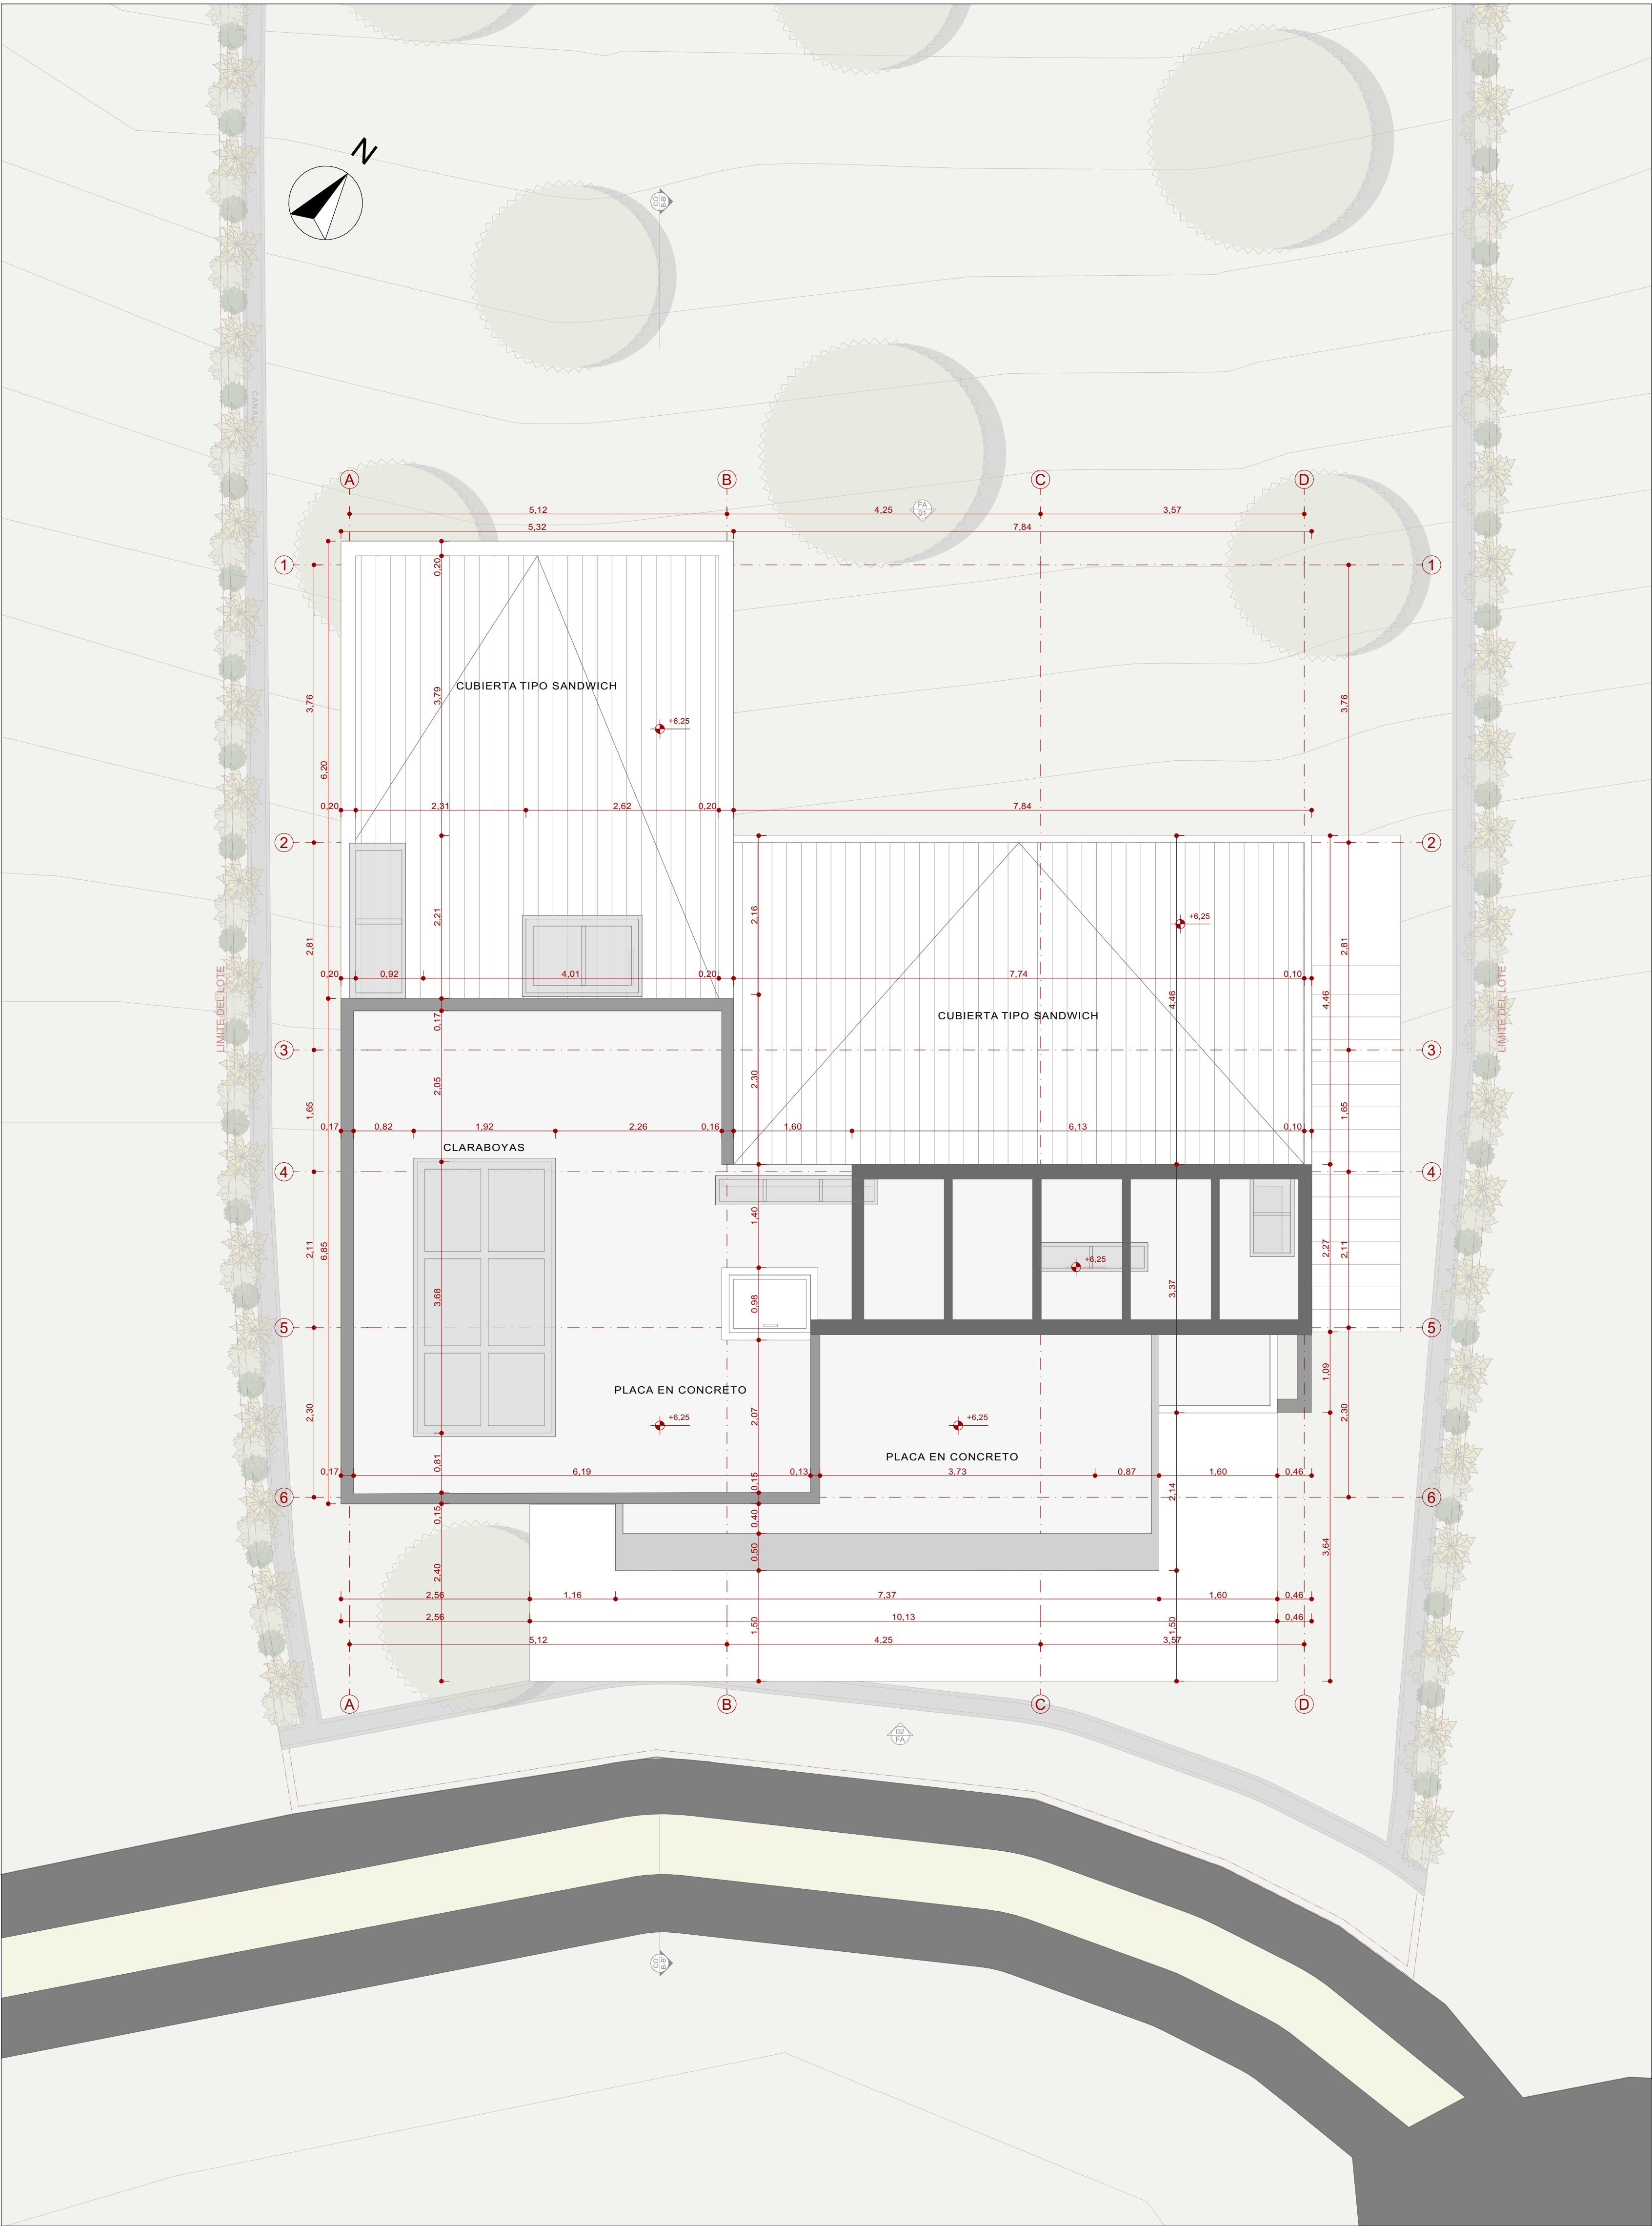

LIIT ARQUITECTURA

LOCALIZACION



DATOS DE PREDIO

DIRECCION:

VILLA GUADALQUIVIR, LOTE 4-12,
FLORIDABLANCA

PROPIETARIOS

BRAYAN PÉREZ DELGADO
C.C. 1.098.810.706

DISEÑADOR

ARQ. JUAN SEBASTIAN BALAMANCA ARDILA
M.P. A30322019-1098742250

LIIT ARQUITECTURA

ACTUACION

PLANIMETRIAS ARQUITECTONICAS
PROYECTO DE VIVIENDA UNIFAMILIAR,
EN VILLA GUADALQUIVIR,
FLORIDABLANCA

CONTENIDO

- PLANO ARQUITECTÓNICO SEGUNDO PISO

- PLANO ARQUITECTÓNICO CUBIERTAS

NOTAS GENERALES

ESCALAS

1:50

28/11/2025

02-PLANO ARQUITECTONICO

PLANO 2 DE 13