



PLANO DE PUERTAS, VENTANAS Y UBICACIÓN DE DETALLES GENERALES

Plano de Sótano:

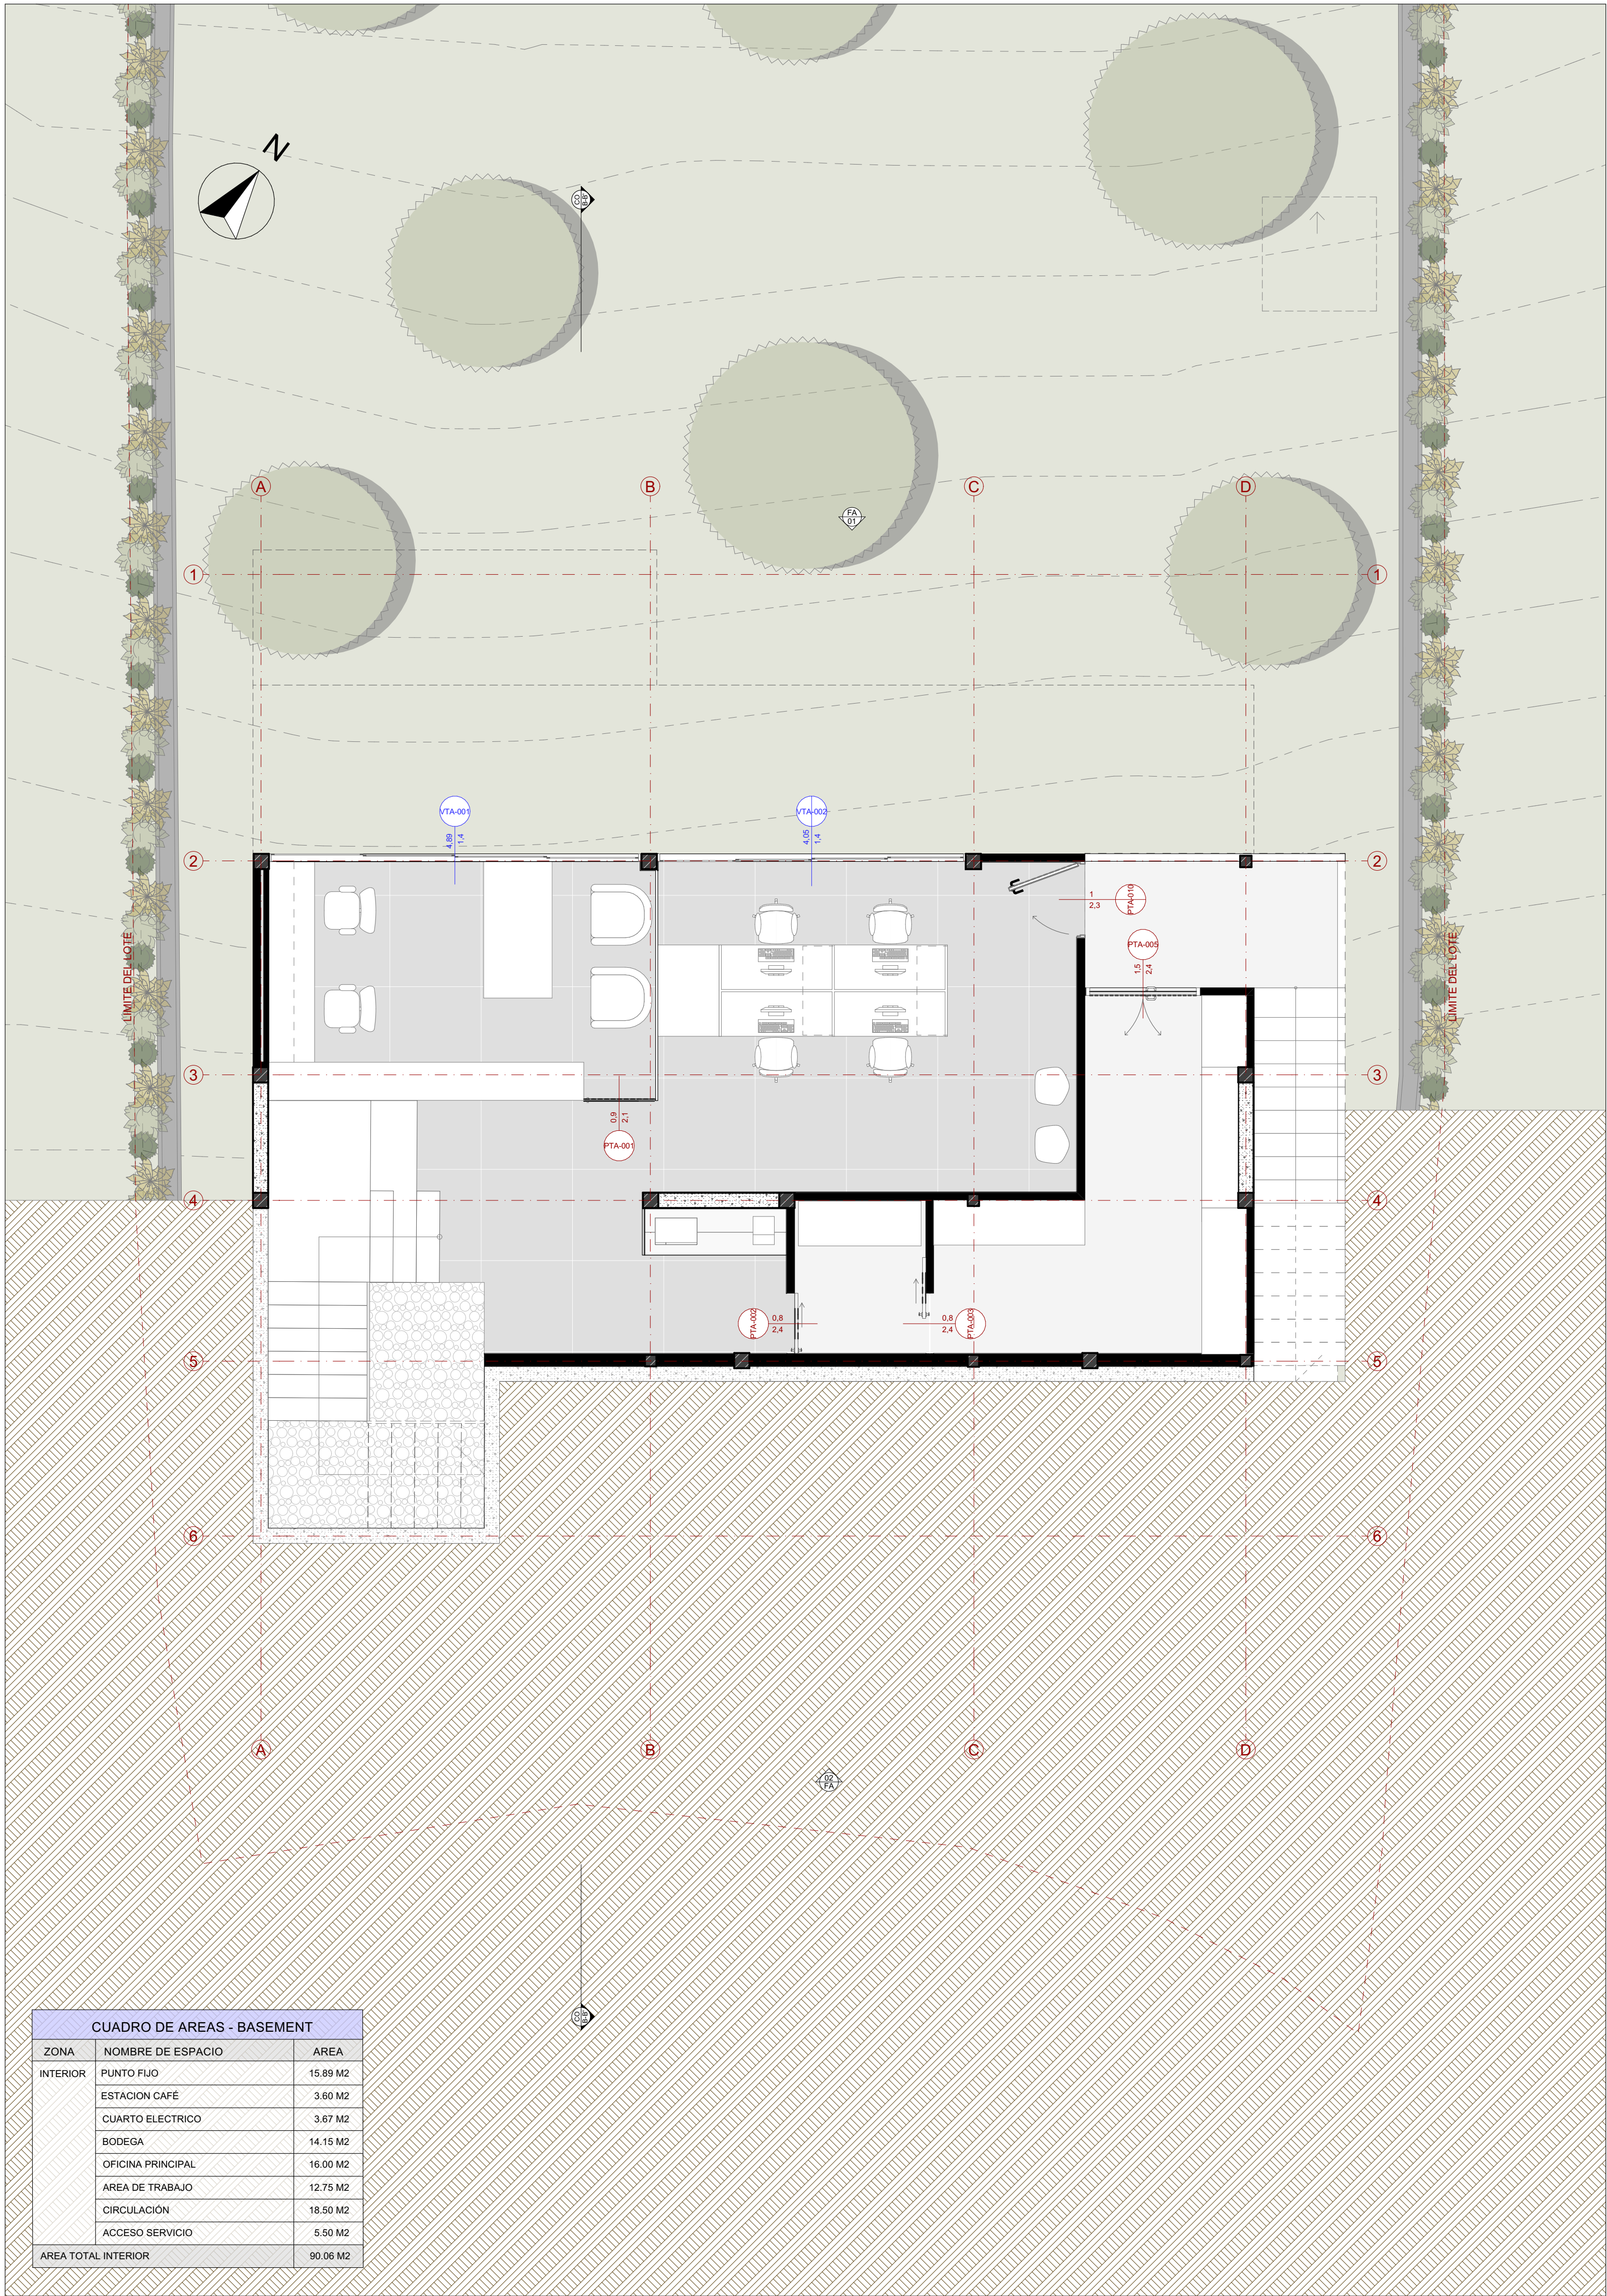

Plano de Primer Piso:

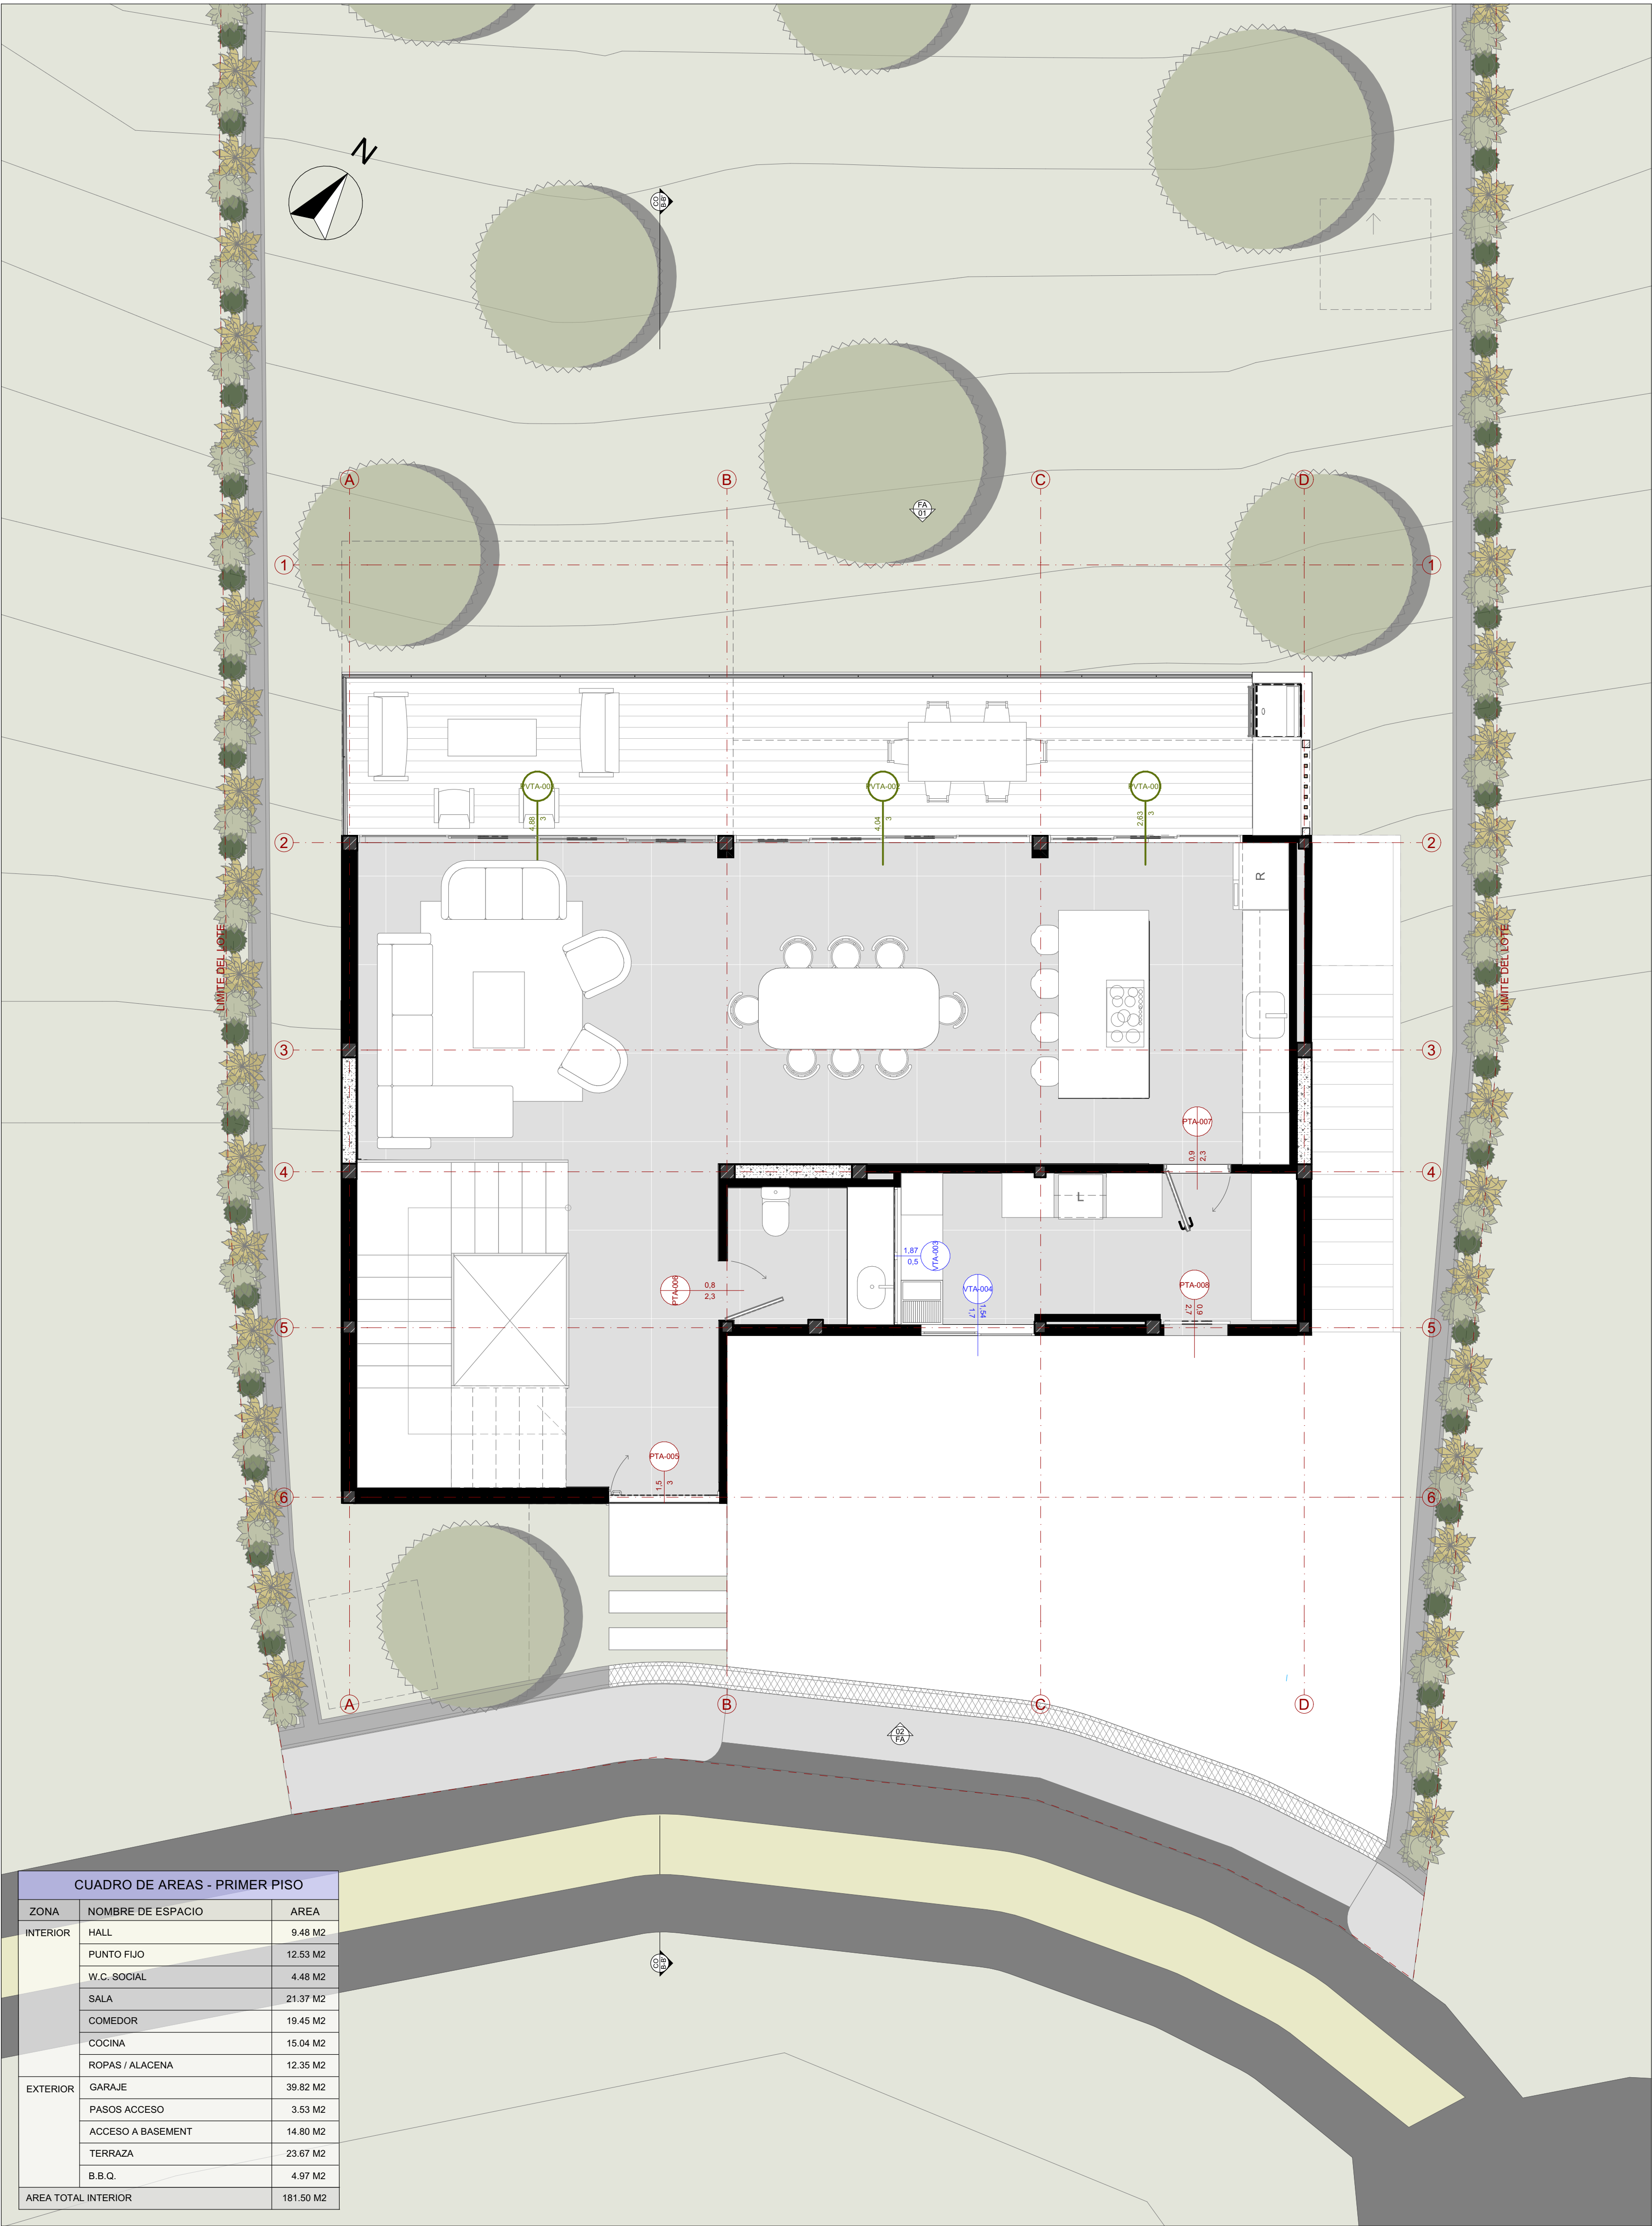

LIIT ARQUITECTURA

LOCALIZACION



DATOS DE PREDIO

DIRECCION:

VILLA GUADALQUIVIR, LOTE 4-12,  
FLORIDABLANCA

PROPIETARIOS

BRAYAN PÉREZ DELGADO  
C.C. 1.098.810.706

DISEÑADOR

ARQ. JUAN SEBASTIAN SALAMANCA ARDILA  
M.P. A30322019-1098742250

LIIT ARQUITECTURA

ACTUACION

PLANIMETRIAS ARQUITECTONICAS  
PROYECTO DE VIVIENDA UNIFAMILIAR,  
EN VILLA GUADALQUIVIR,  
FLORIDABLANCA

CONTENIDO

- PLANO DE PUERTAS, VENTANAS Y  
UBICACIÓN DE DETALLES GENERALES  
DEL SÓTANO

- PLANO DE PUERTAS, VENTANAS Y  
UBICACIÓN DE DETALLES GENERALES  
DEL PRIMER PISO

NOTAS GENERALES

ESCALAS

1:50

28/11/2025

04 - PLANO DE PUERTAS,  
VENTANAS Y DETALLES