



PLANO DE PUERTAS, VENTANAS Y UBICACIÓN DE DETALLES GENERALES

Plano de Segundo Piso:

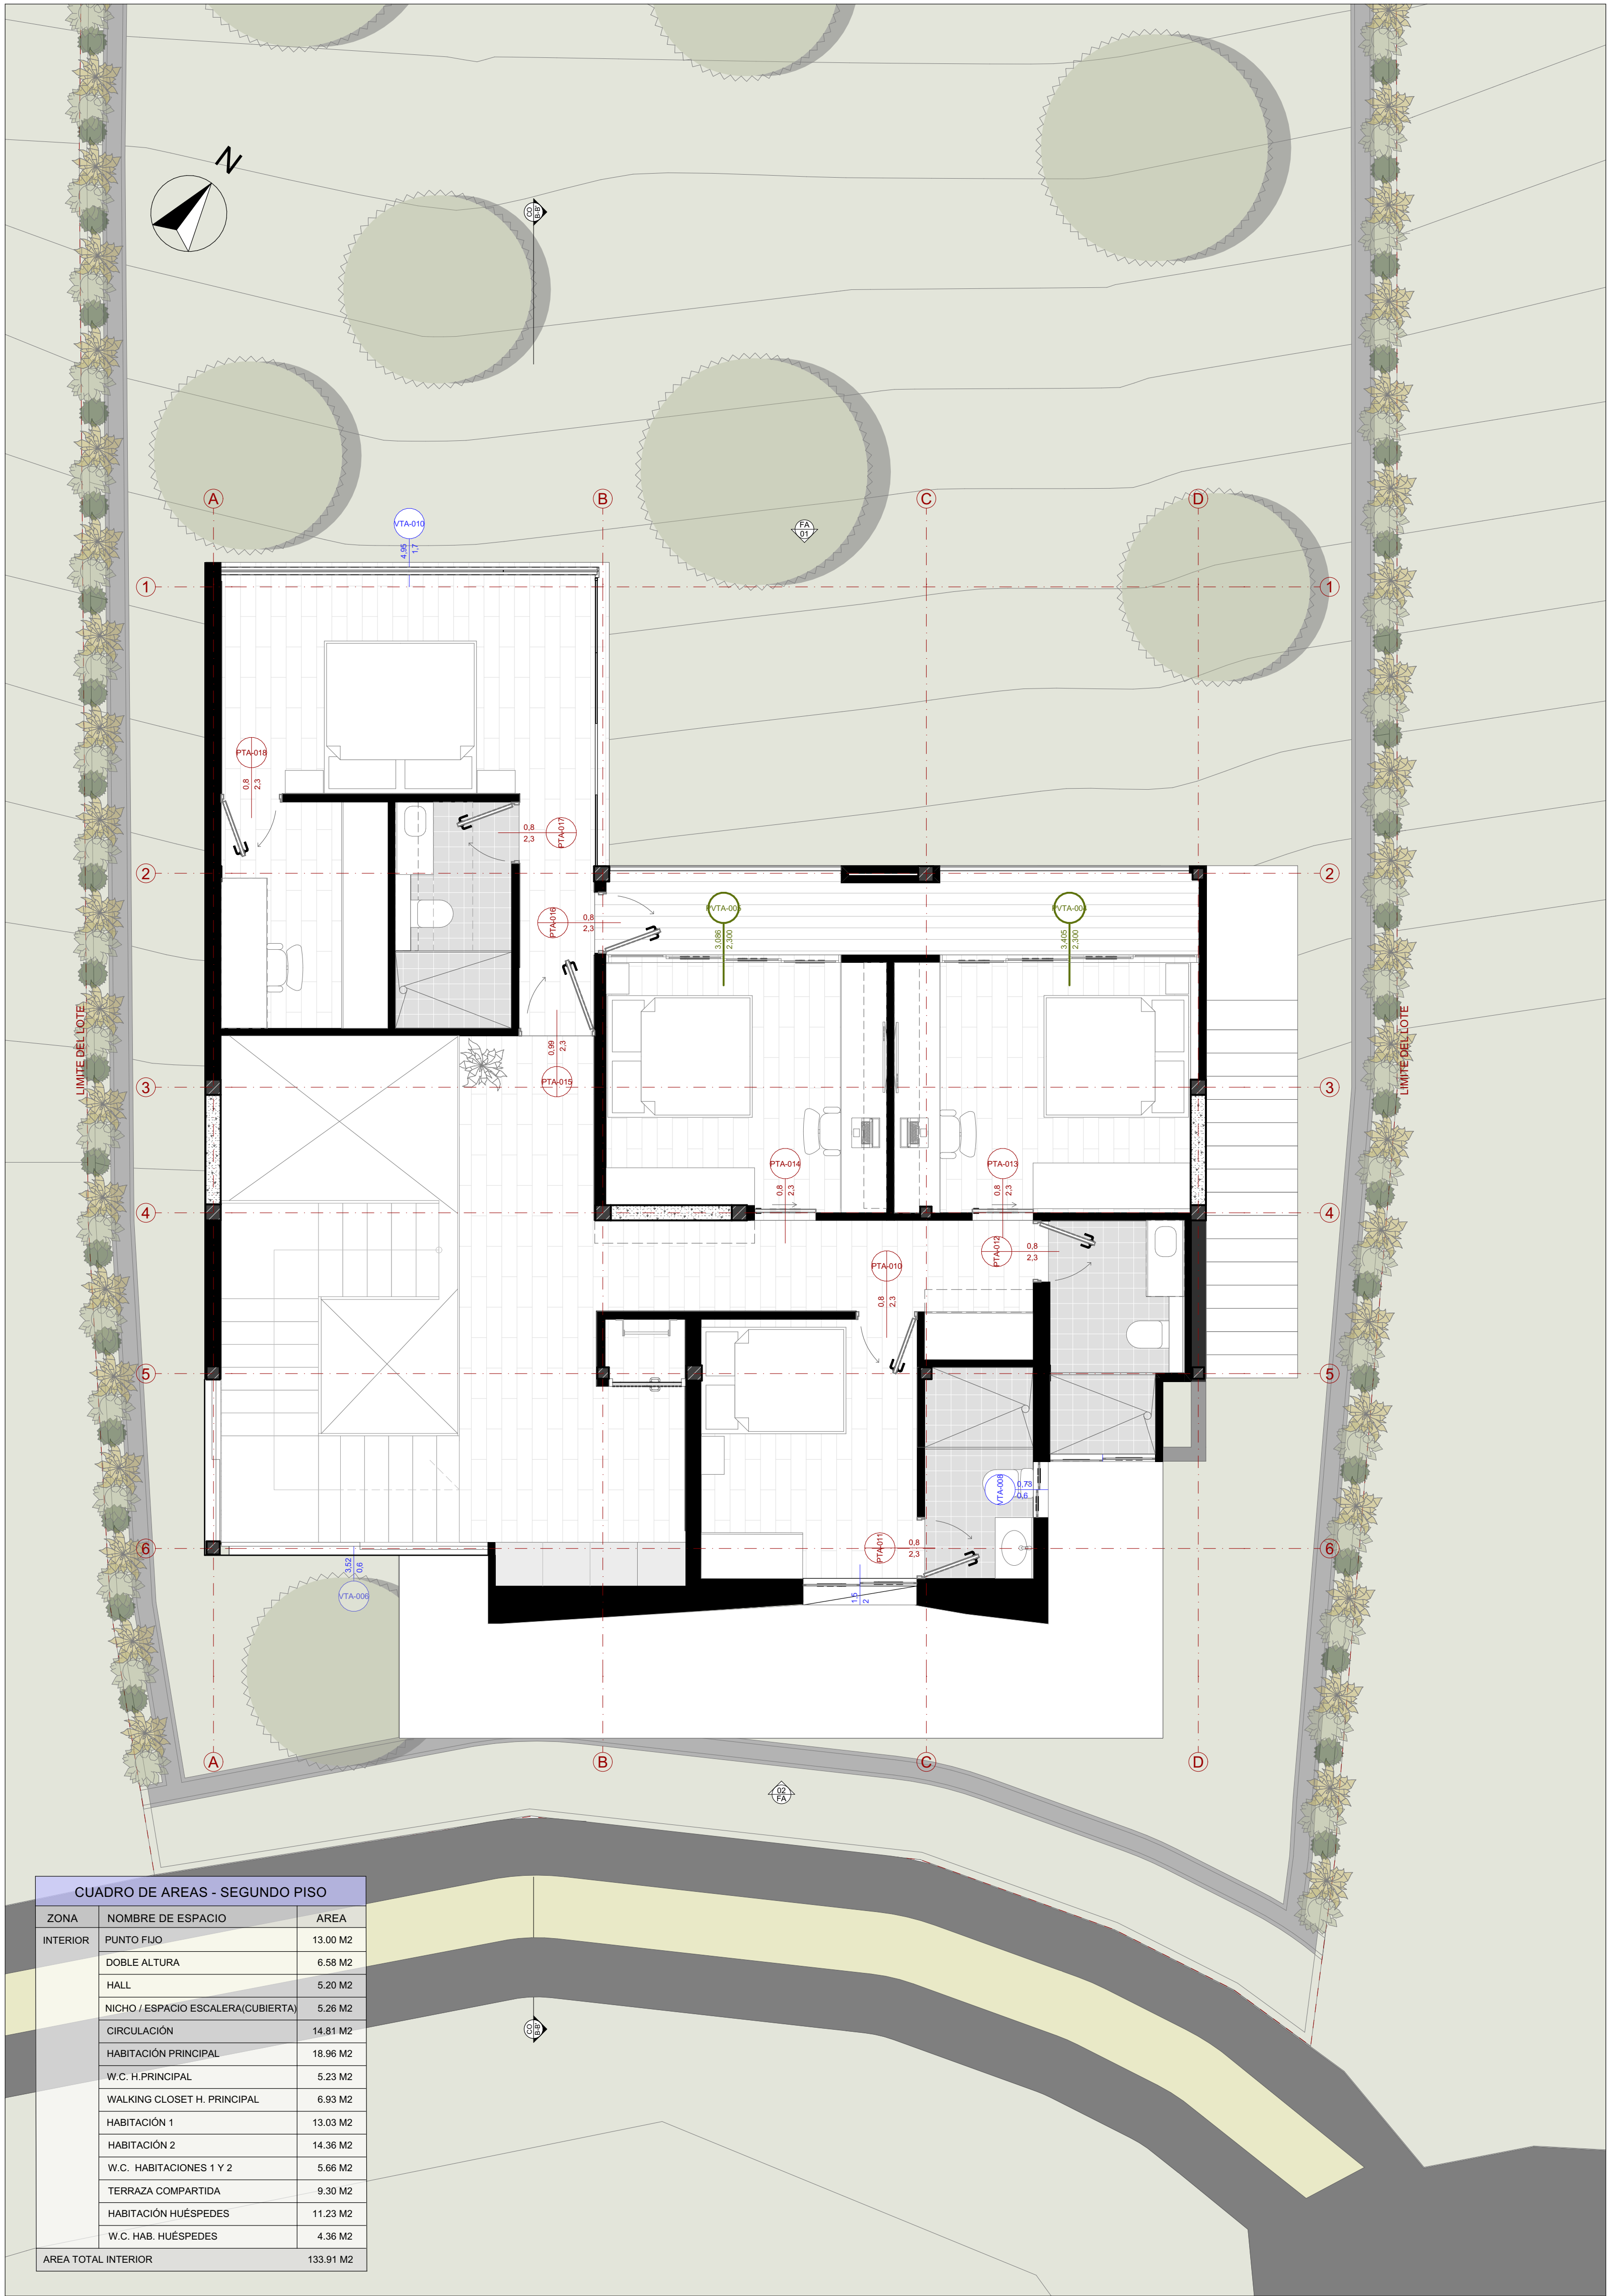

Plano de Cubiertas:

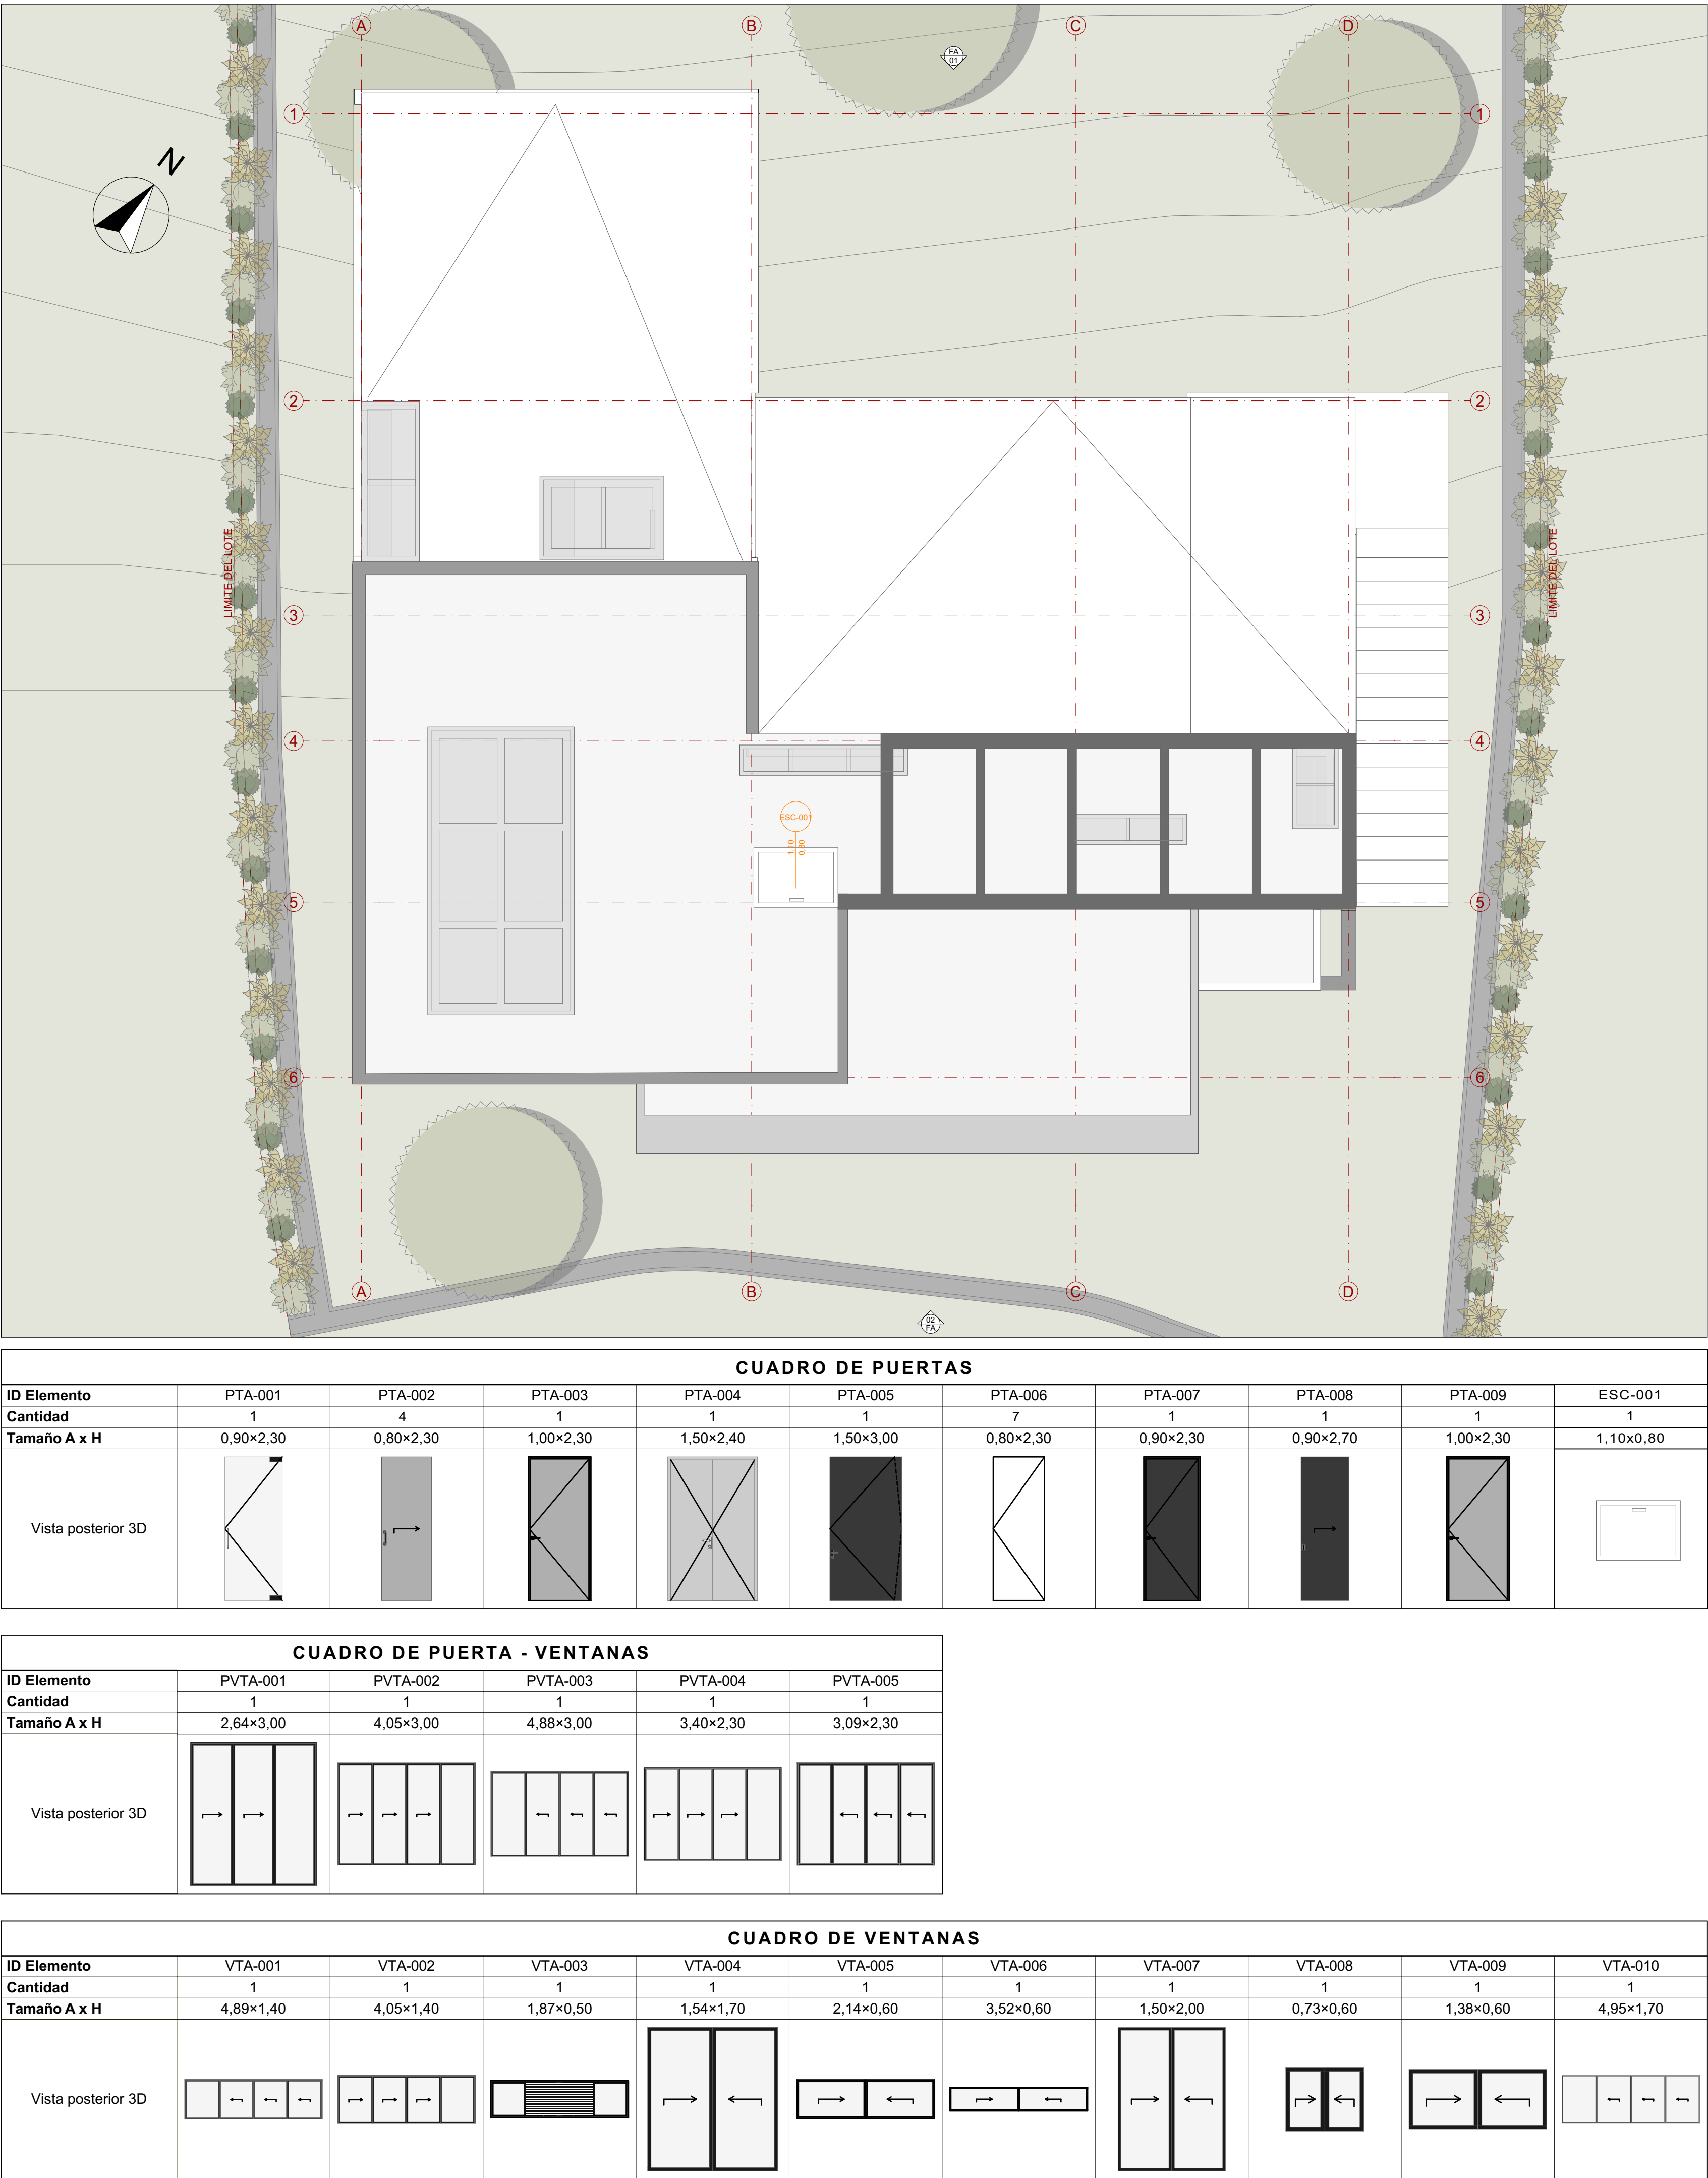

LIIT

ARQUITECTURA

LOCALIZACION

DATOS DE PREDIO

DIRECCION:

VILLA GUADALQUIVIR, LOTE 4-12, FLORIDABLANCA

PROPIETARIOS

BRAYAN PÉREZ DELGADO
C.C. 1.098.810.706

DISEÑADOR

ARQ. JUAN SEBASTIAN SALAMANCA ARDILA
M.P. A30322019-1098742250

LIIT ARQUITECTURA

ACTUACION

PLANIMETRÍAS ARQUITECTONICAS
PROYECTO DE VIVIENDA UNIFAMILIAR,
EN VILLA GUADALQUIVIR,
FLORIDABLANCA

CONTENIDO

- PLANO DE PUERTAS, VENTANAS Y
UBICACIÓN DE DETALLES GENERALES
DEL SEGUNDO PISO

- PLANO DE PUERTAS, VENTANAS Y
UBICACIÓN DE DETALLES GENERALES DE
LAS CUBIERTAS

NOTAS GENERALES

ESCALAS

1:50

28/11/2025

06-PLANO DE PUERTAS,
VENTANAS Y DETALLES

PLANO 6 DE 13