



PLANO DE ACABADOS GENERALES DE PISOS Y MUROS

Plano de Sótano:

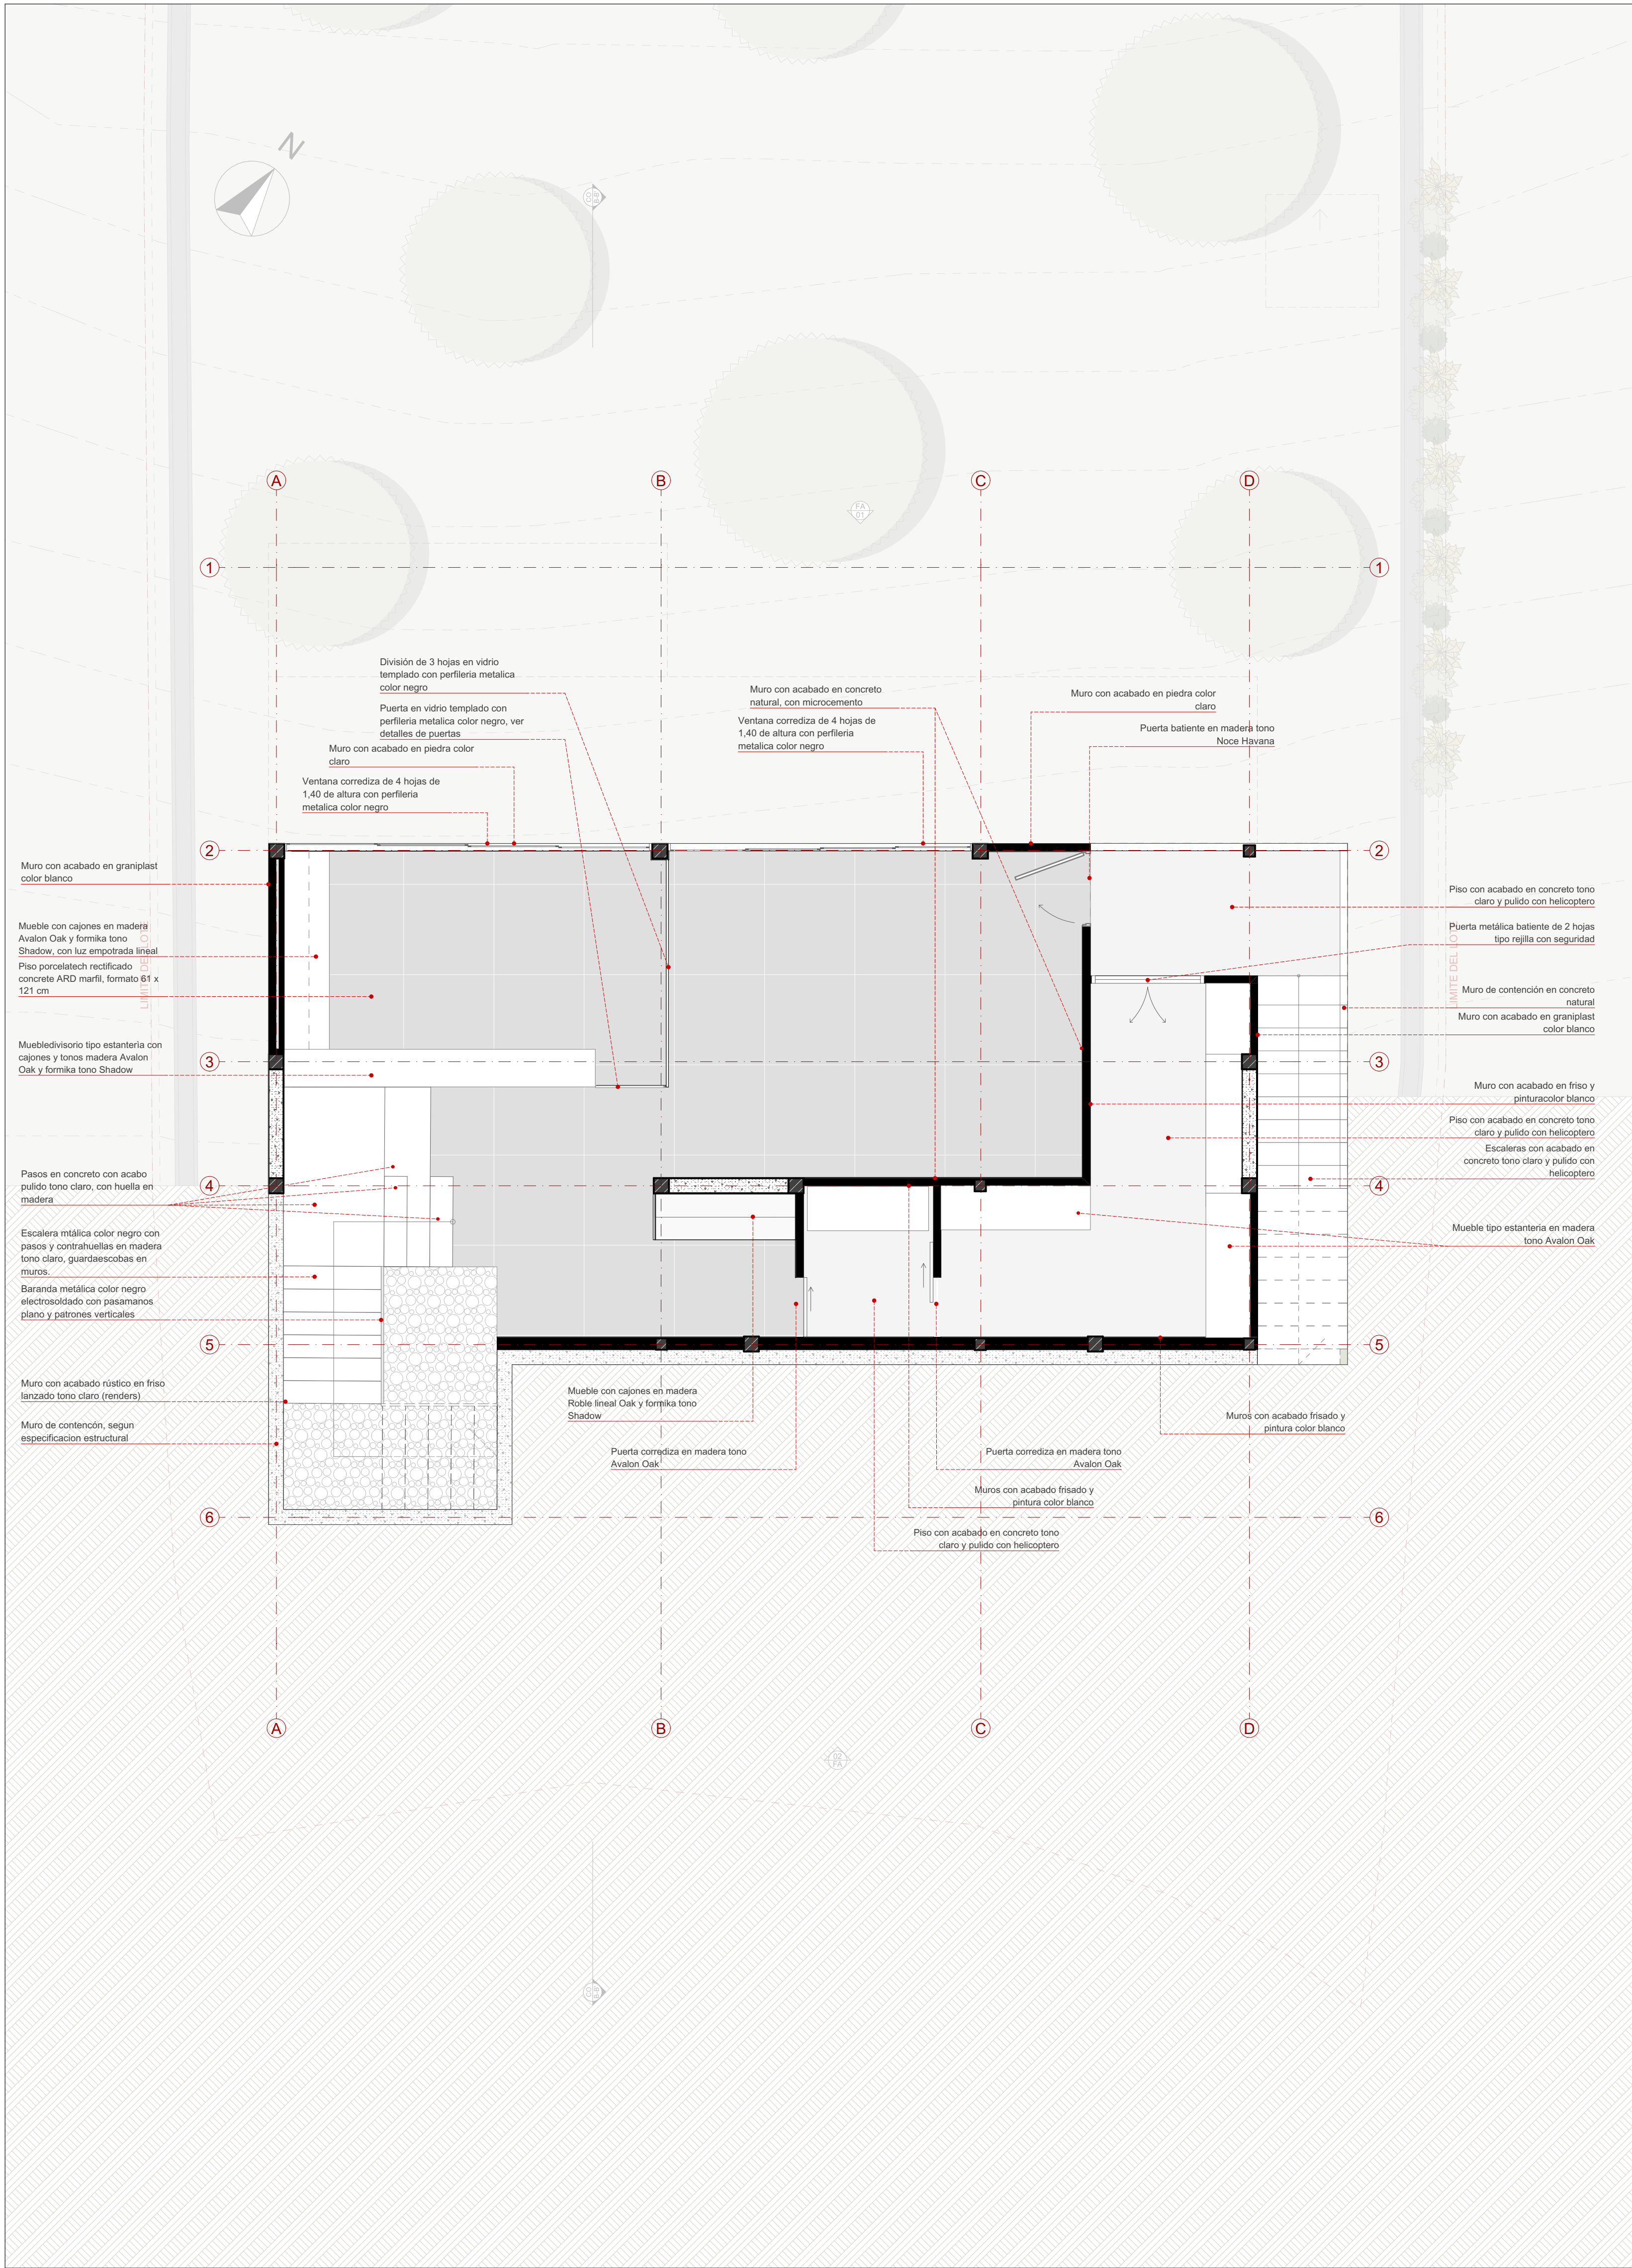

Plano de Primer Piso:

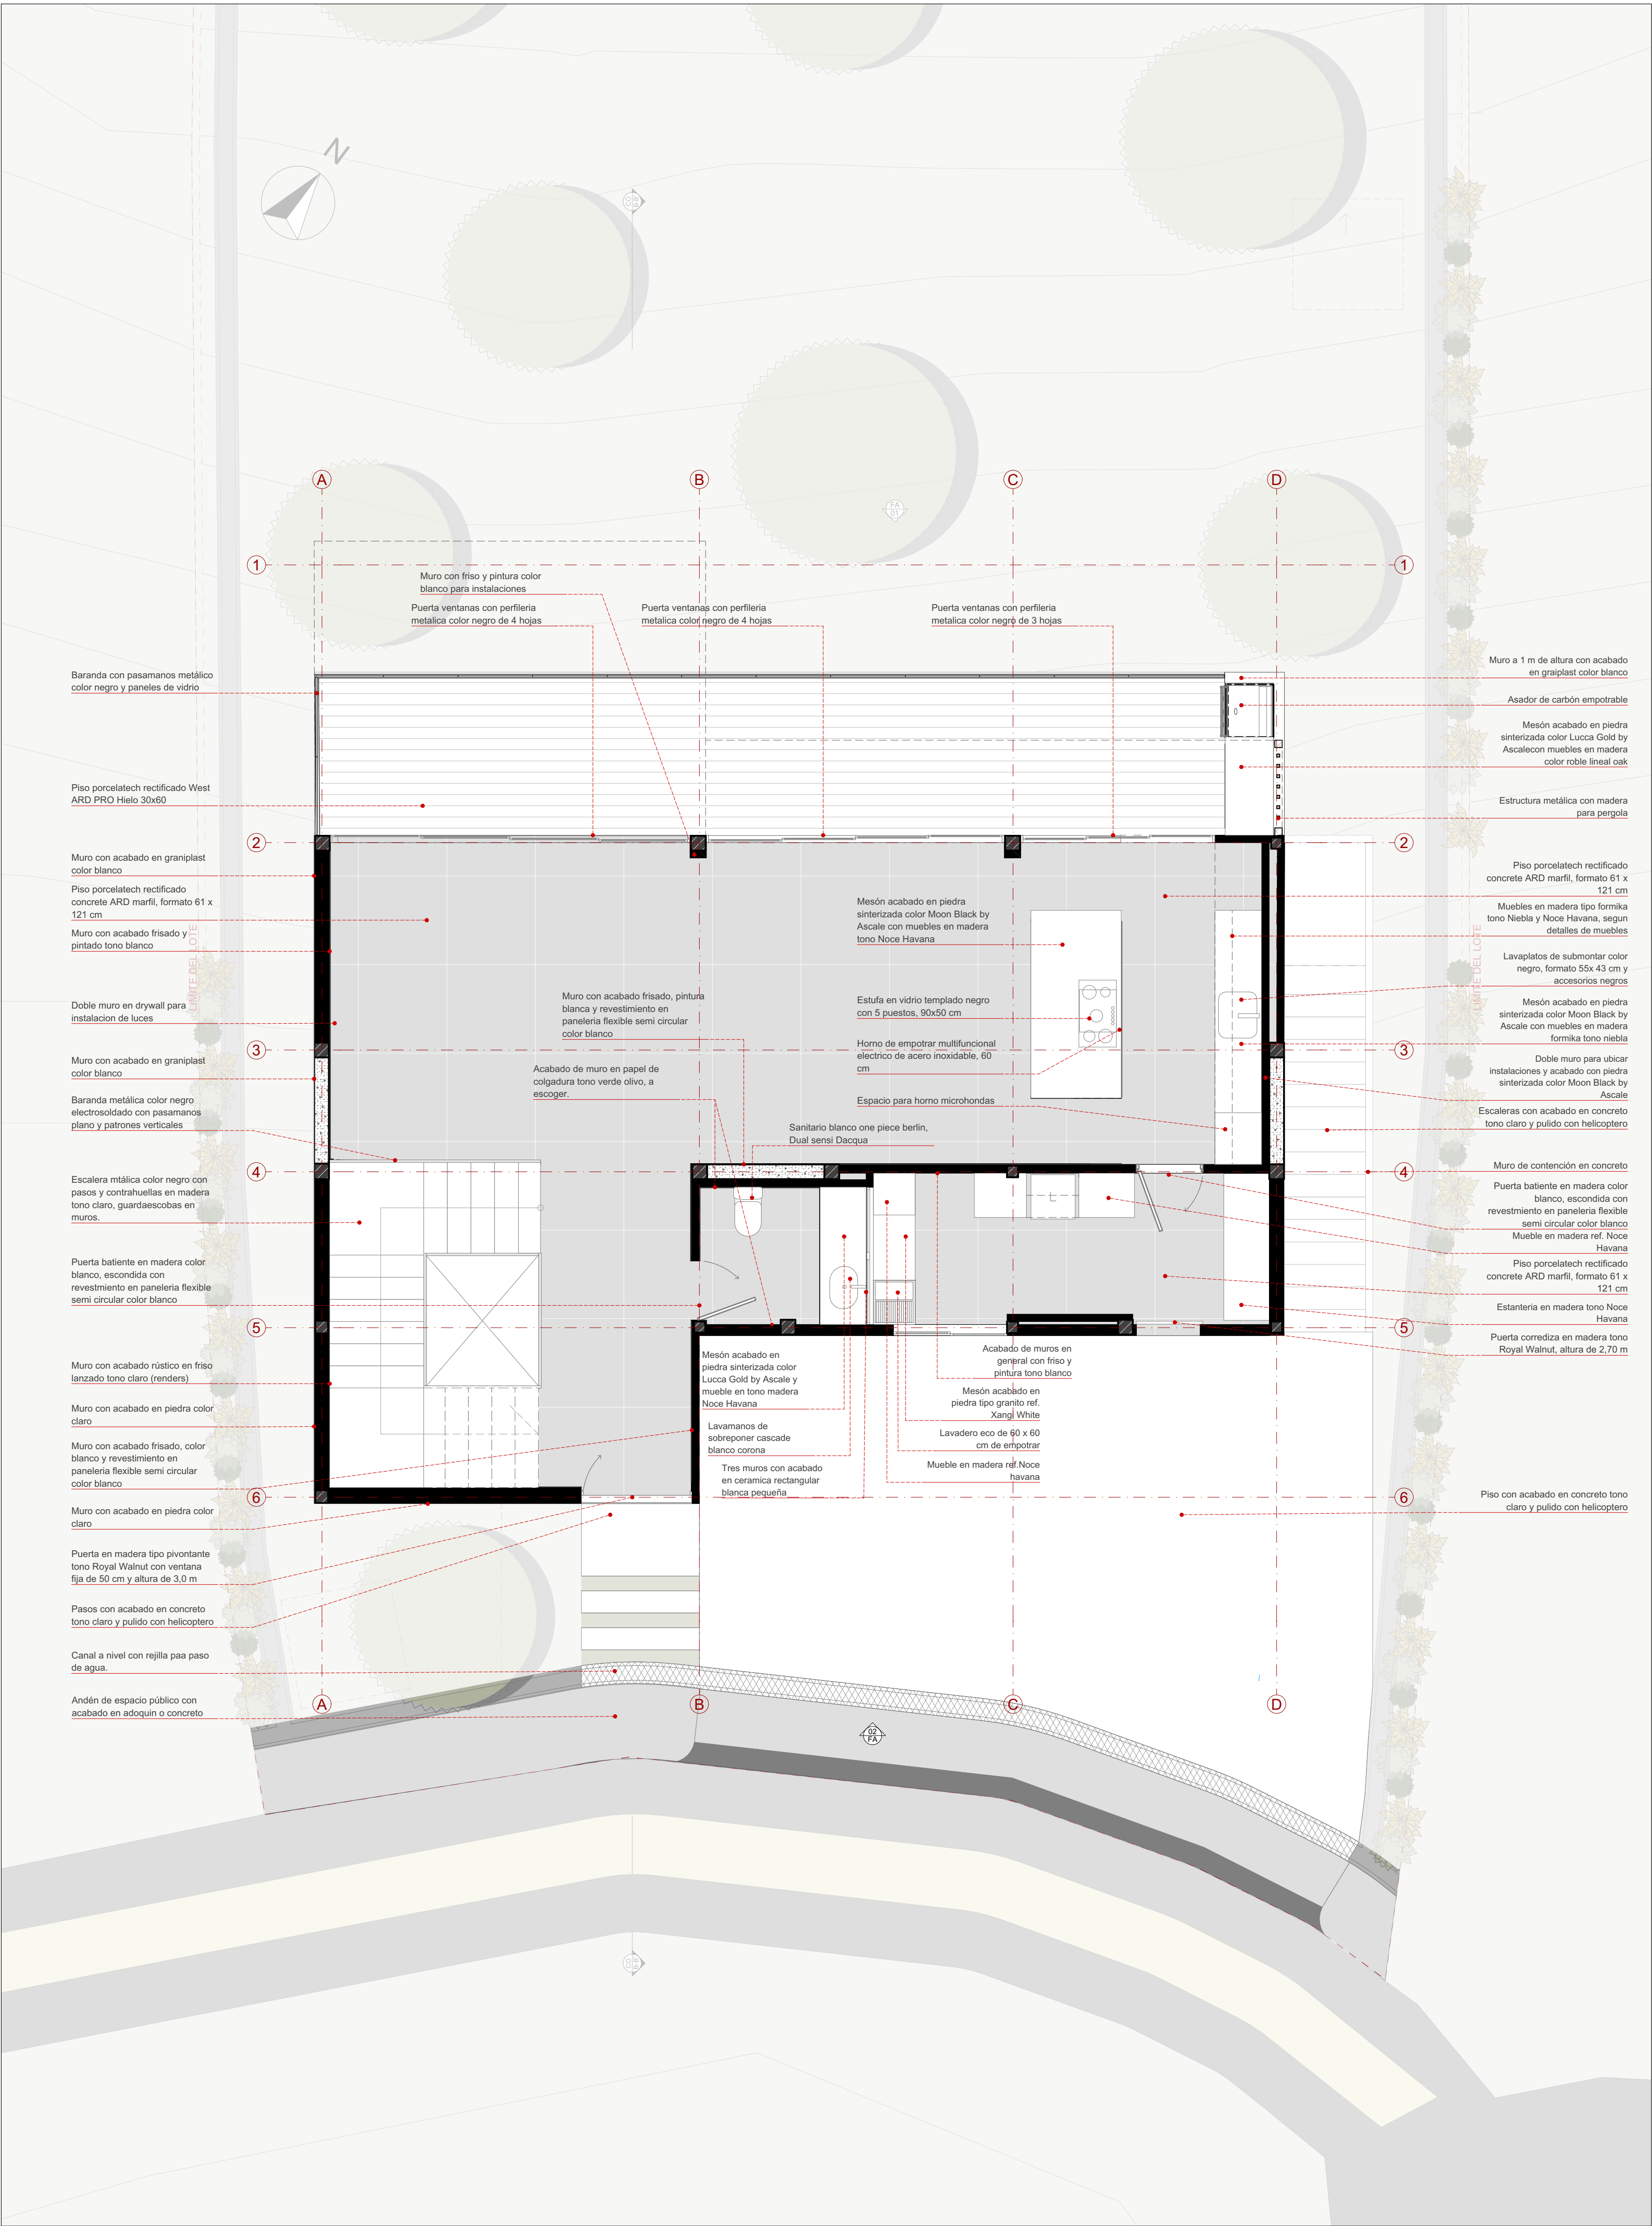

DATOS DE PREDIO

DIRECCION:

VILLA GUADALQUIVIR, LOTE 4-12, FLORIDABLANCA

PROPIETARIOS

BRAYAN PÉREZ DELGADO
C.C. 1.098.810.706

DISEÑADOR

ARQ. JUAN SEBASTIAN SALAMANCA ARDILA
M.P. A36322019-1098742250

LIIT ARQUITECTURA

ACTUACION

PLANIMETRIAS ARQUITECTONICAS
PROYECTO DE VIVIENDA UNIFAMILIAR,
EN VILLA GUADALQUIVIR,
FLORIDABLANCA

CONTENIDO

- PLANO DE ACABADOS GENERALES DE
PISOS Y MUROS DEL SÓTANO

- PLANO DE ACABADOS GENERALES DE
PISOS Y MUROS DEL PRIMER PISO

NOTAS GENERALES

ESCALAS

1:50

28/11/2025

06 - PLANO DE ACABADOS
GENERALES DE PISOS Y MUROS