



PLANO DE ACABADOS GENERALES DE PISOS Y MUROS

Plano de Segundo Piso:

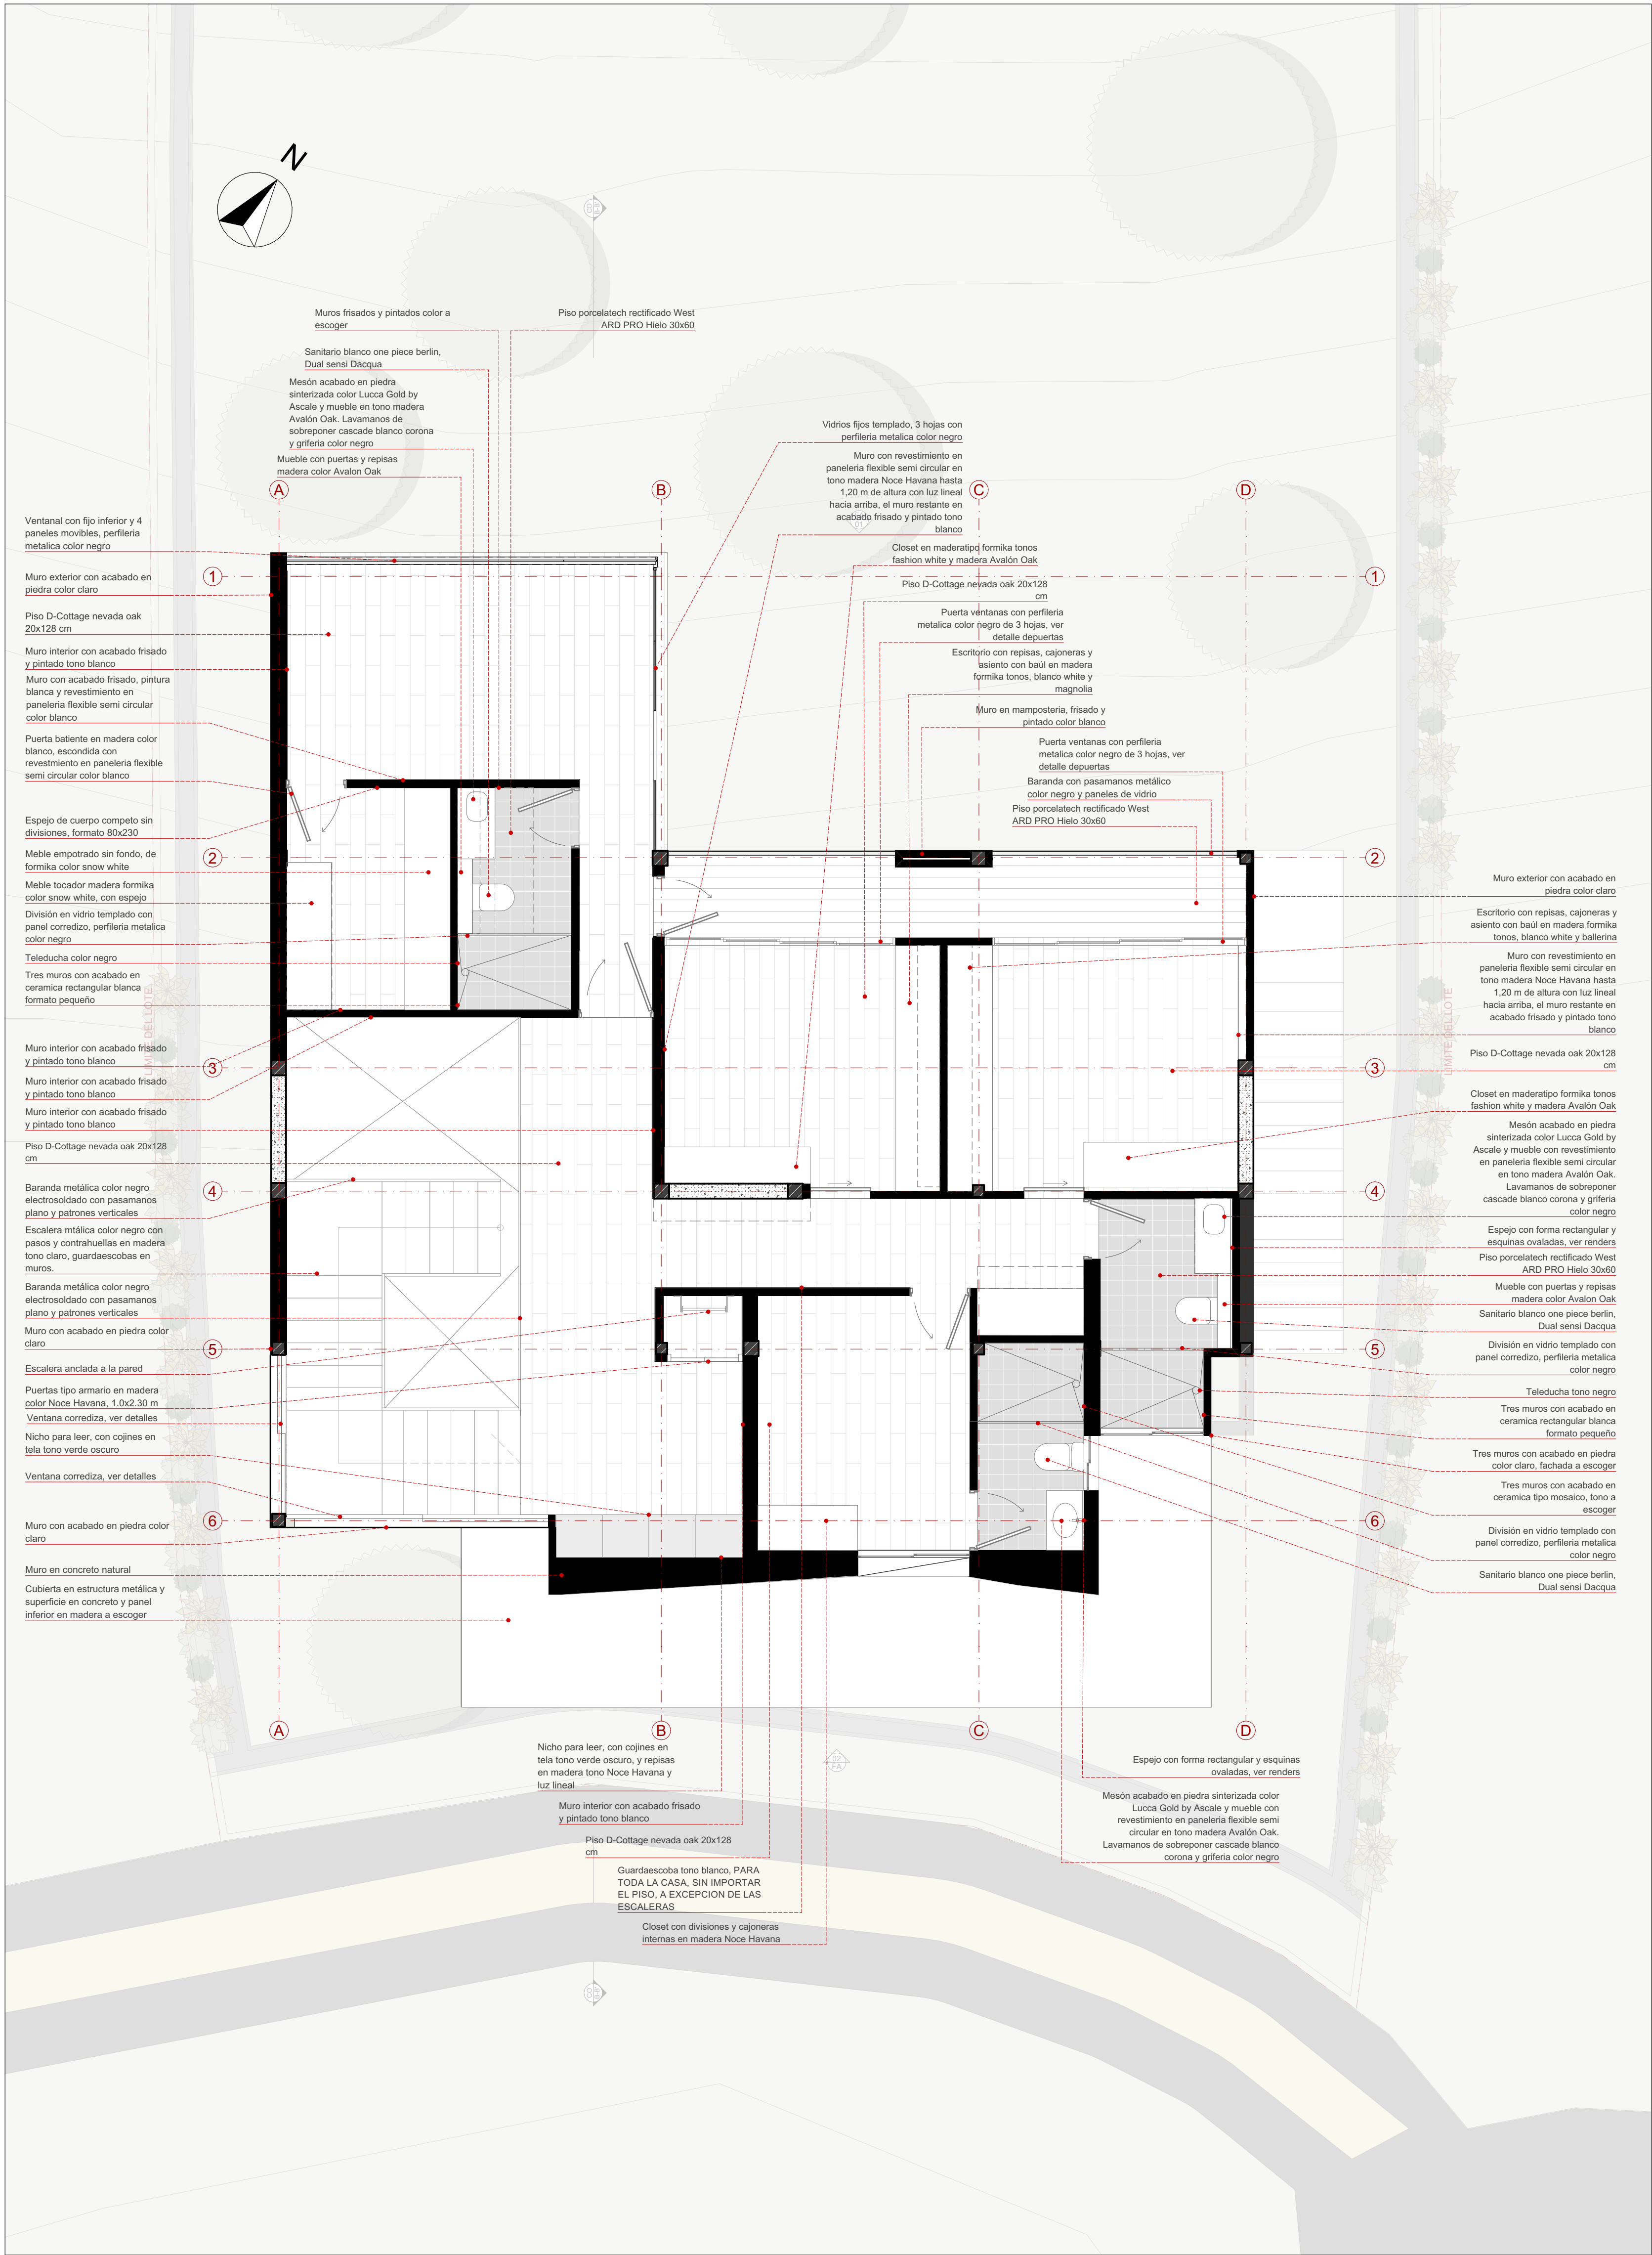

Plano de Cubiertas:

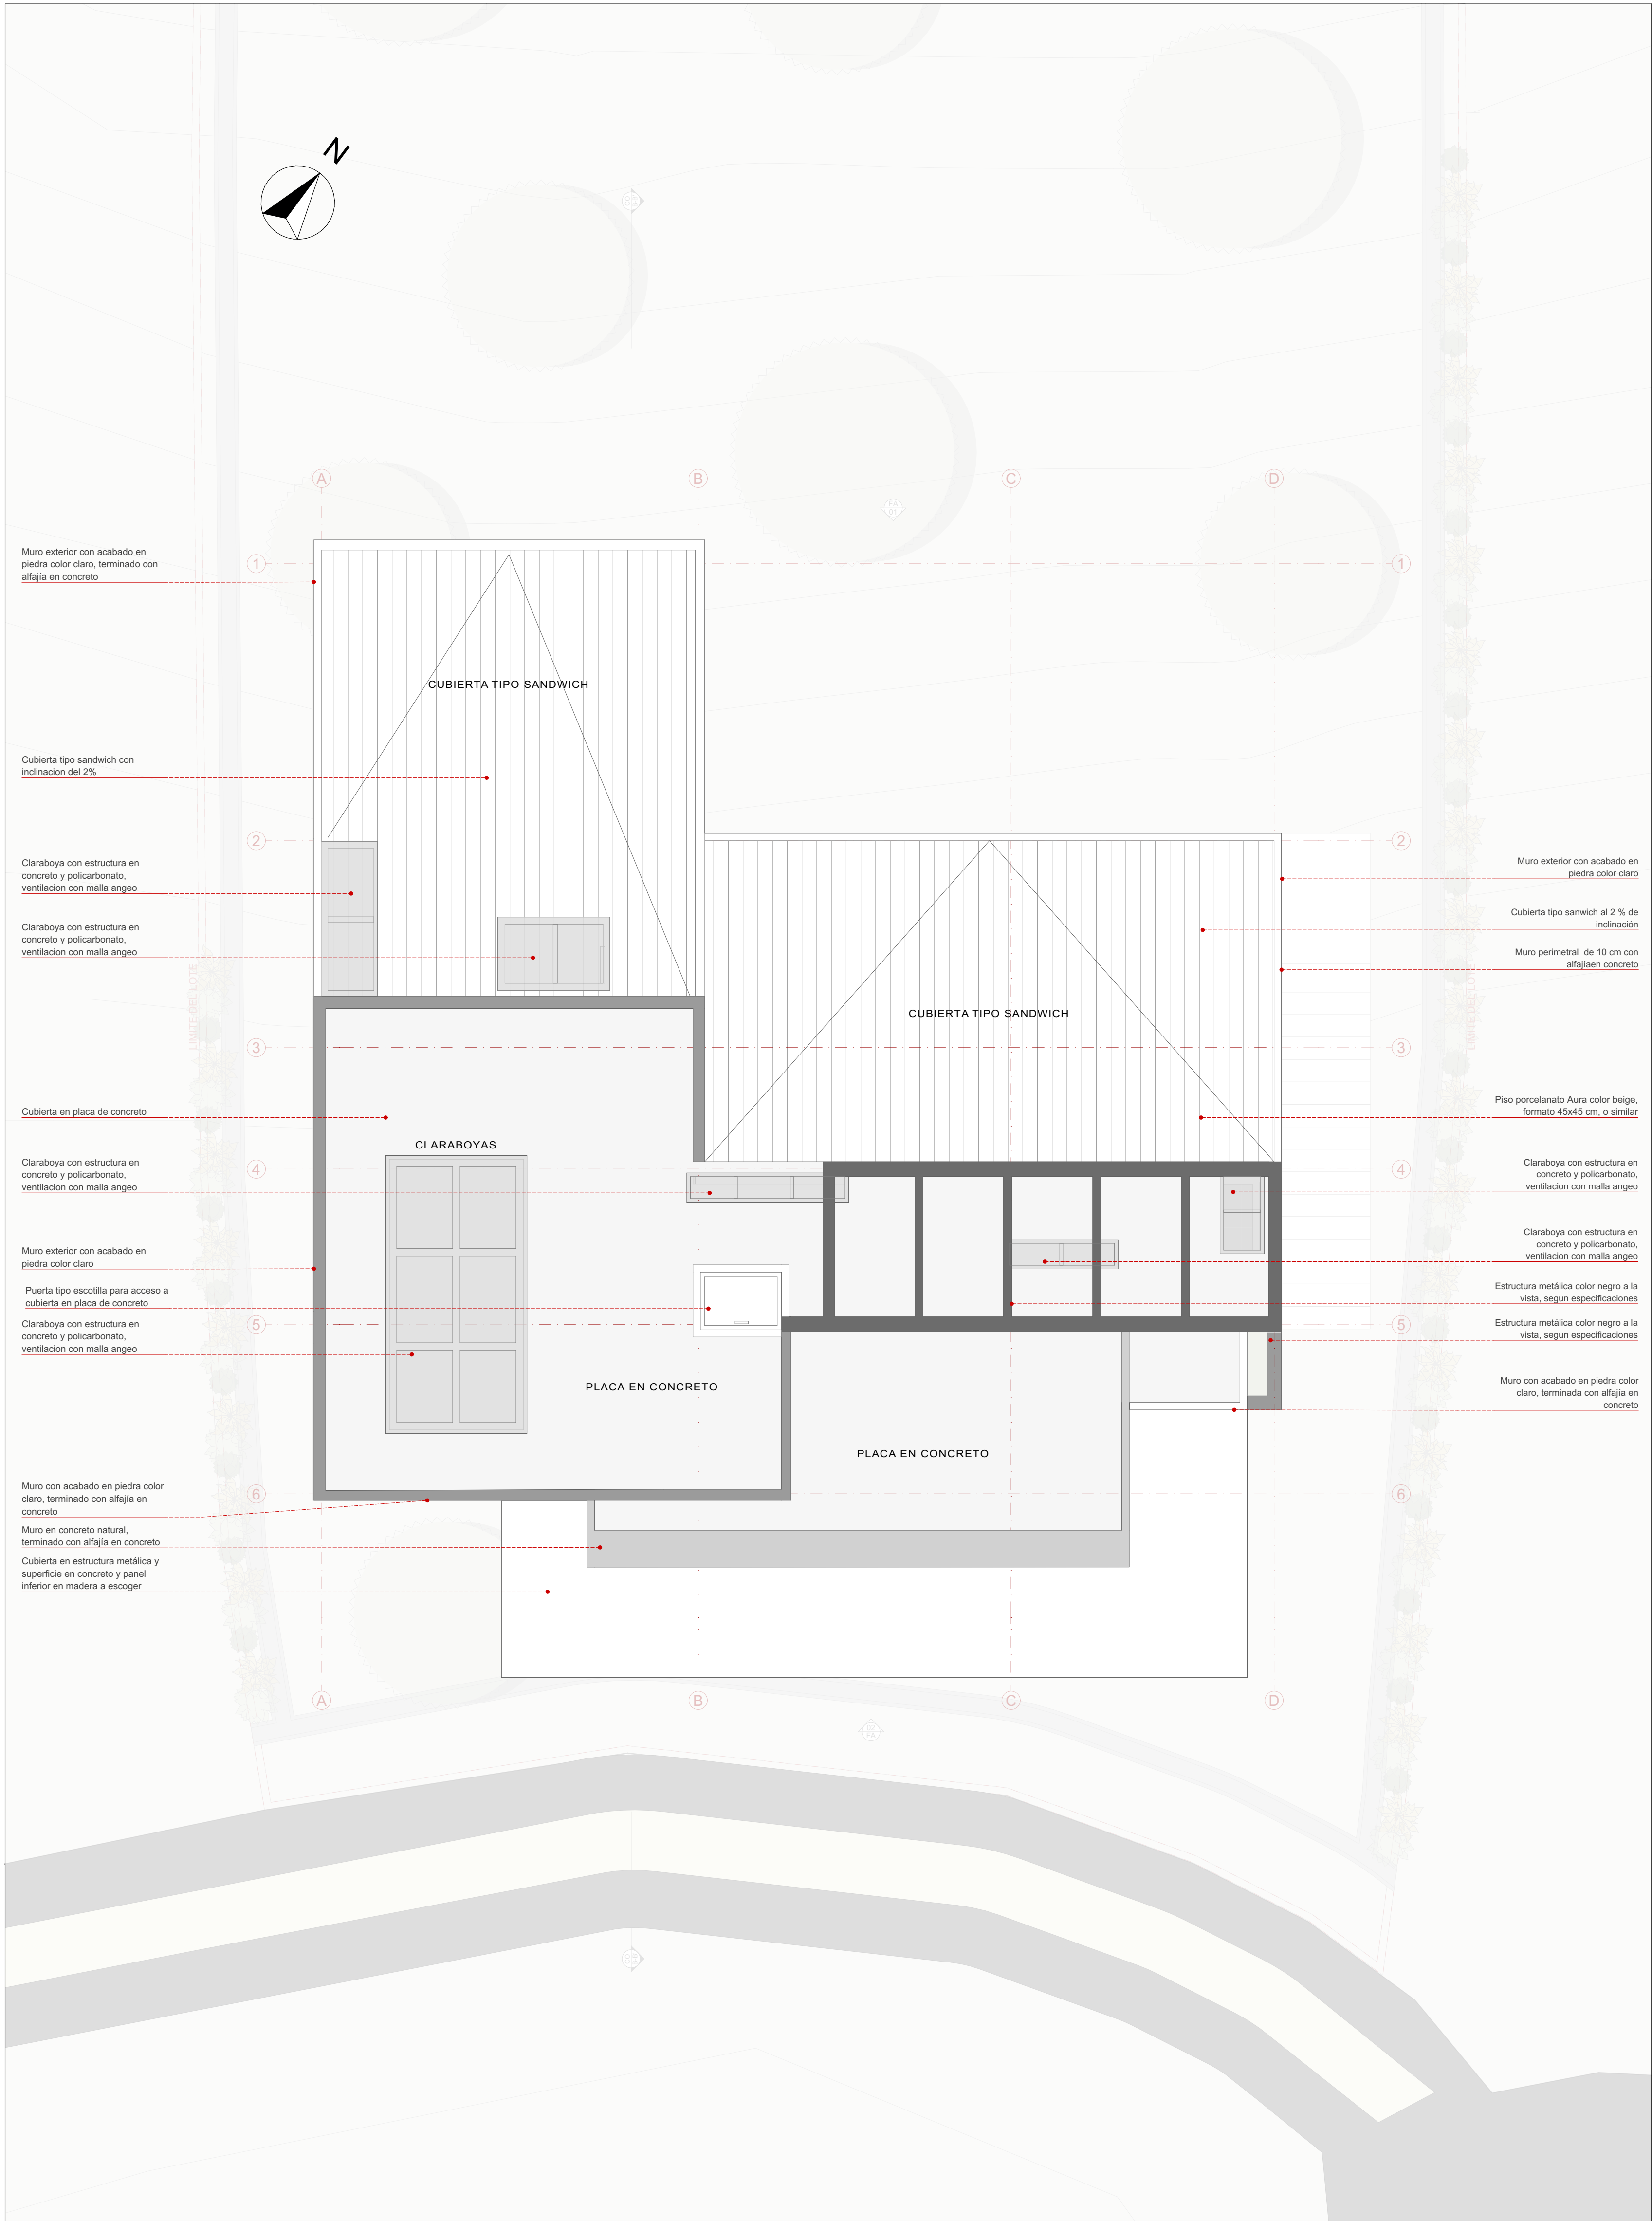

LOCALIZACION



DATOS DE PREDIO

DIRECCION:

VILLA GUADALQUIVR, LOTE 4-12, FLORIDABLANCA

PROPIETARIOS

BRAYAN PÉREZ DELGADO
C.C. 1.098.810.706

DISEÑADOR

ARQ. JUAN SEBASTIAN SALAMANCA ARDILA
M.P. A36322019-1098742250

LIIT ARQUITECTURA

ACTUACION

PLANIMETRÍAS ARQUITECTONICAS
PROYECTO DE VIVIENDA UNIFAMILIAR, EN VILLA GUADALQUIVR, FLORIDABLANCA

CONTENIDO

- PLANO DE ACABADOS GENERALES DE PISOS Y MUROS DEL SEGUNDO PISO

- PLANO DE ACABADOS GENERALES DE PISOS Y MUROS DE LAS CUBIERTAS

NOTAS GENERALES

ESCALAS

1:50

28/11/2025

07 - PLANO DE ACABADOS GENERALES DE PISOS Y MUROS