


PLANO DE CIELORASO E ILUMINACIÓN

Plano de Segundo Piso:

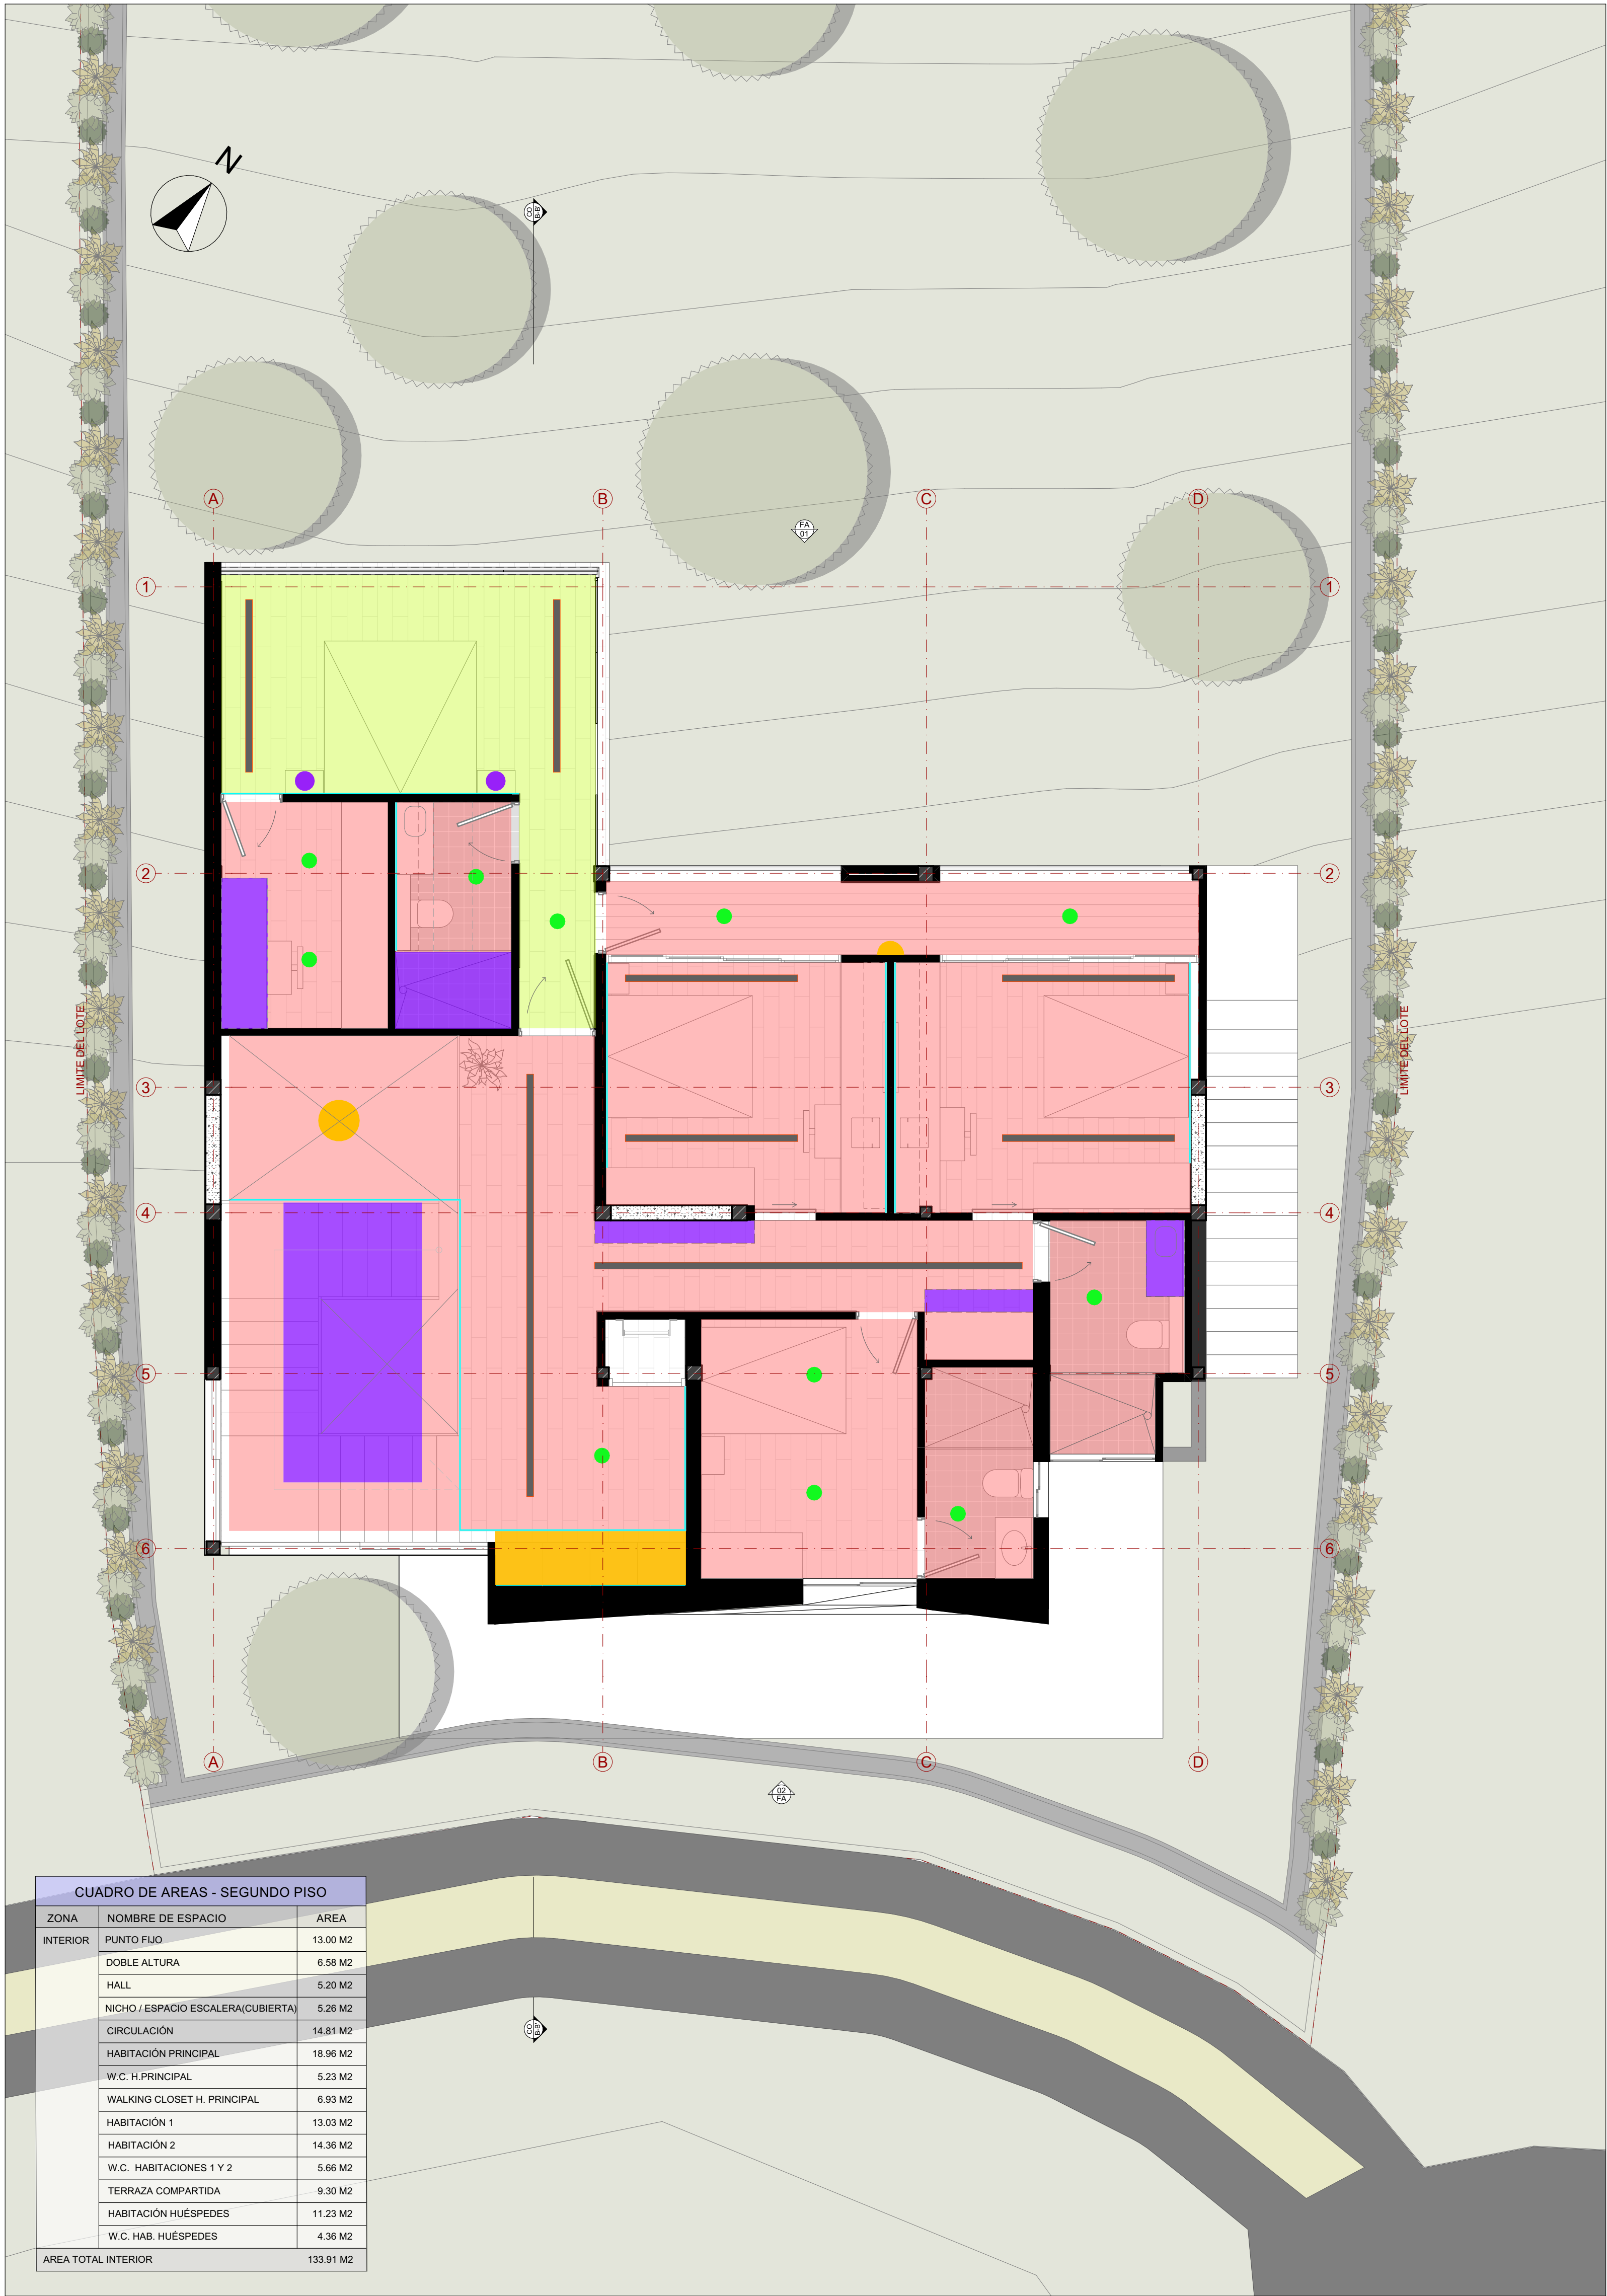

CONVENCIONES ILUMINACIÓN

	Luz tipo panel de incrustar en cieloraso, luz a escoger, de 20 cm de diametro
	Luz tipo panel de sobreponer en pared, luz a escoger, de 20 cm de diametro
	Luminaria tipo aplique de pared color negro, tono de luz a escoger
	Luminaria tipo aplique en piso, diametro pequeno para jardin seco
	Luminaria colgante de perfileria metalica negra, luz blanca, formato 12x120 cm
	Luminaria tipo led de luz de pista con perfileria metalica negra de empotrar
	Luminaria descolgada del techo a escoger para barra de cocina y habitacion principal
	Luminaria descolgada del techo a escoger para doble altura
	Luminaria led circular tipo spot de perfileria negra, luz calida
	Luminaria lineal led, luz neutra, con perfileria metalica delgada, para techo y pared

CONVENCIONES CIELORASOS

	Cieloraso en drywall color blanco puro, altura de 2,40 m
	Cieloraso con acabado de microcemento tono natural
	Cieloraso en drywall color blanco puro, altura de 3 m
	Cubierta con estructura metalica y madera con panel en policarbonato satinado
	Cieloraso con acabado de madera, tono a escoger (parecido al Noce Havana)
	Cieloraso en drywall color blanco puro, altura de 2,80 m
	Cieloraso en drywall color blanco puro, altura de 2,30 m
	Cieloraso en drywall color blanco puro dentro de nicho de lectura, altura de 2,90 m
	Espacio donde irian las claraboyas

LOCALIZACION



DATOS DE PREDIO

DIRECCION:

VILLA GUADALQUIVIR, LOTE 4-12, FLORIDABLANCA

PROPIETARIOS

BRAYAN PÉREZ DELGADO
C.C. 1.098.810.706

DISEÑADOR

ARQ. JUAN SEBASTIAN SALAMANCA ARDILA
M.P. A36322019-1098742250

LIIT ARQUITECTURA

ACTUACION

PLANIMETRÍAS ARQUITECTONICAS
PROYECTO DE VIVIENDA UNIFAMILIAR,
EN VILLA GUADALQUIVIR,
FLORIDABLANCA

CONTENIDO

- PLANO DE CIELORASOS E ILUMINACIÓN
DEL SEGUNDO PISO

NOTAS GENERALES

ESCALAS

1:50

28/11/2025

09 - PLANO DE CIELORASOS E
ILUMINACIÓN