



PLANO ARQUITECTONICO DE INSTALACIONES GENERALES

Plano de Sótano:

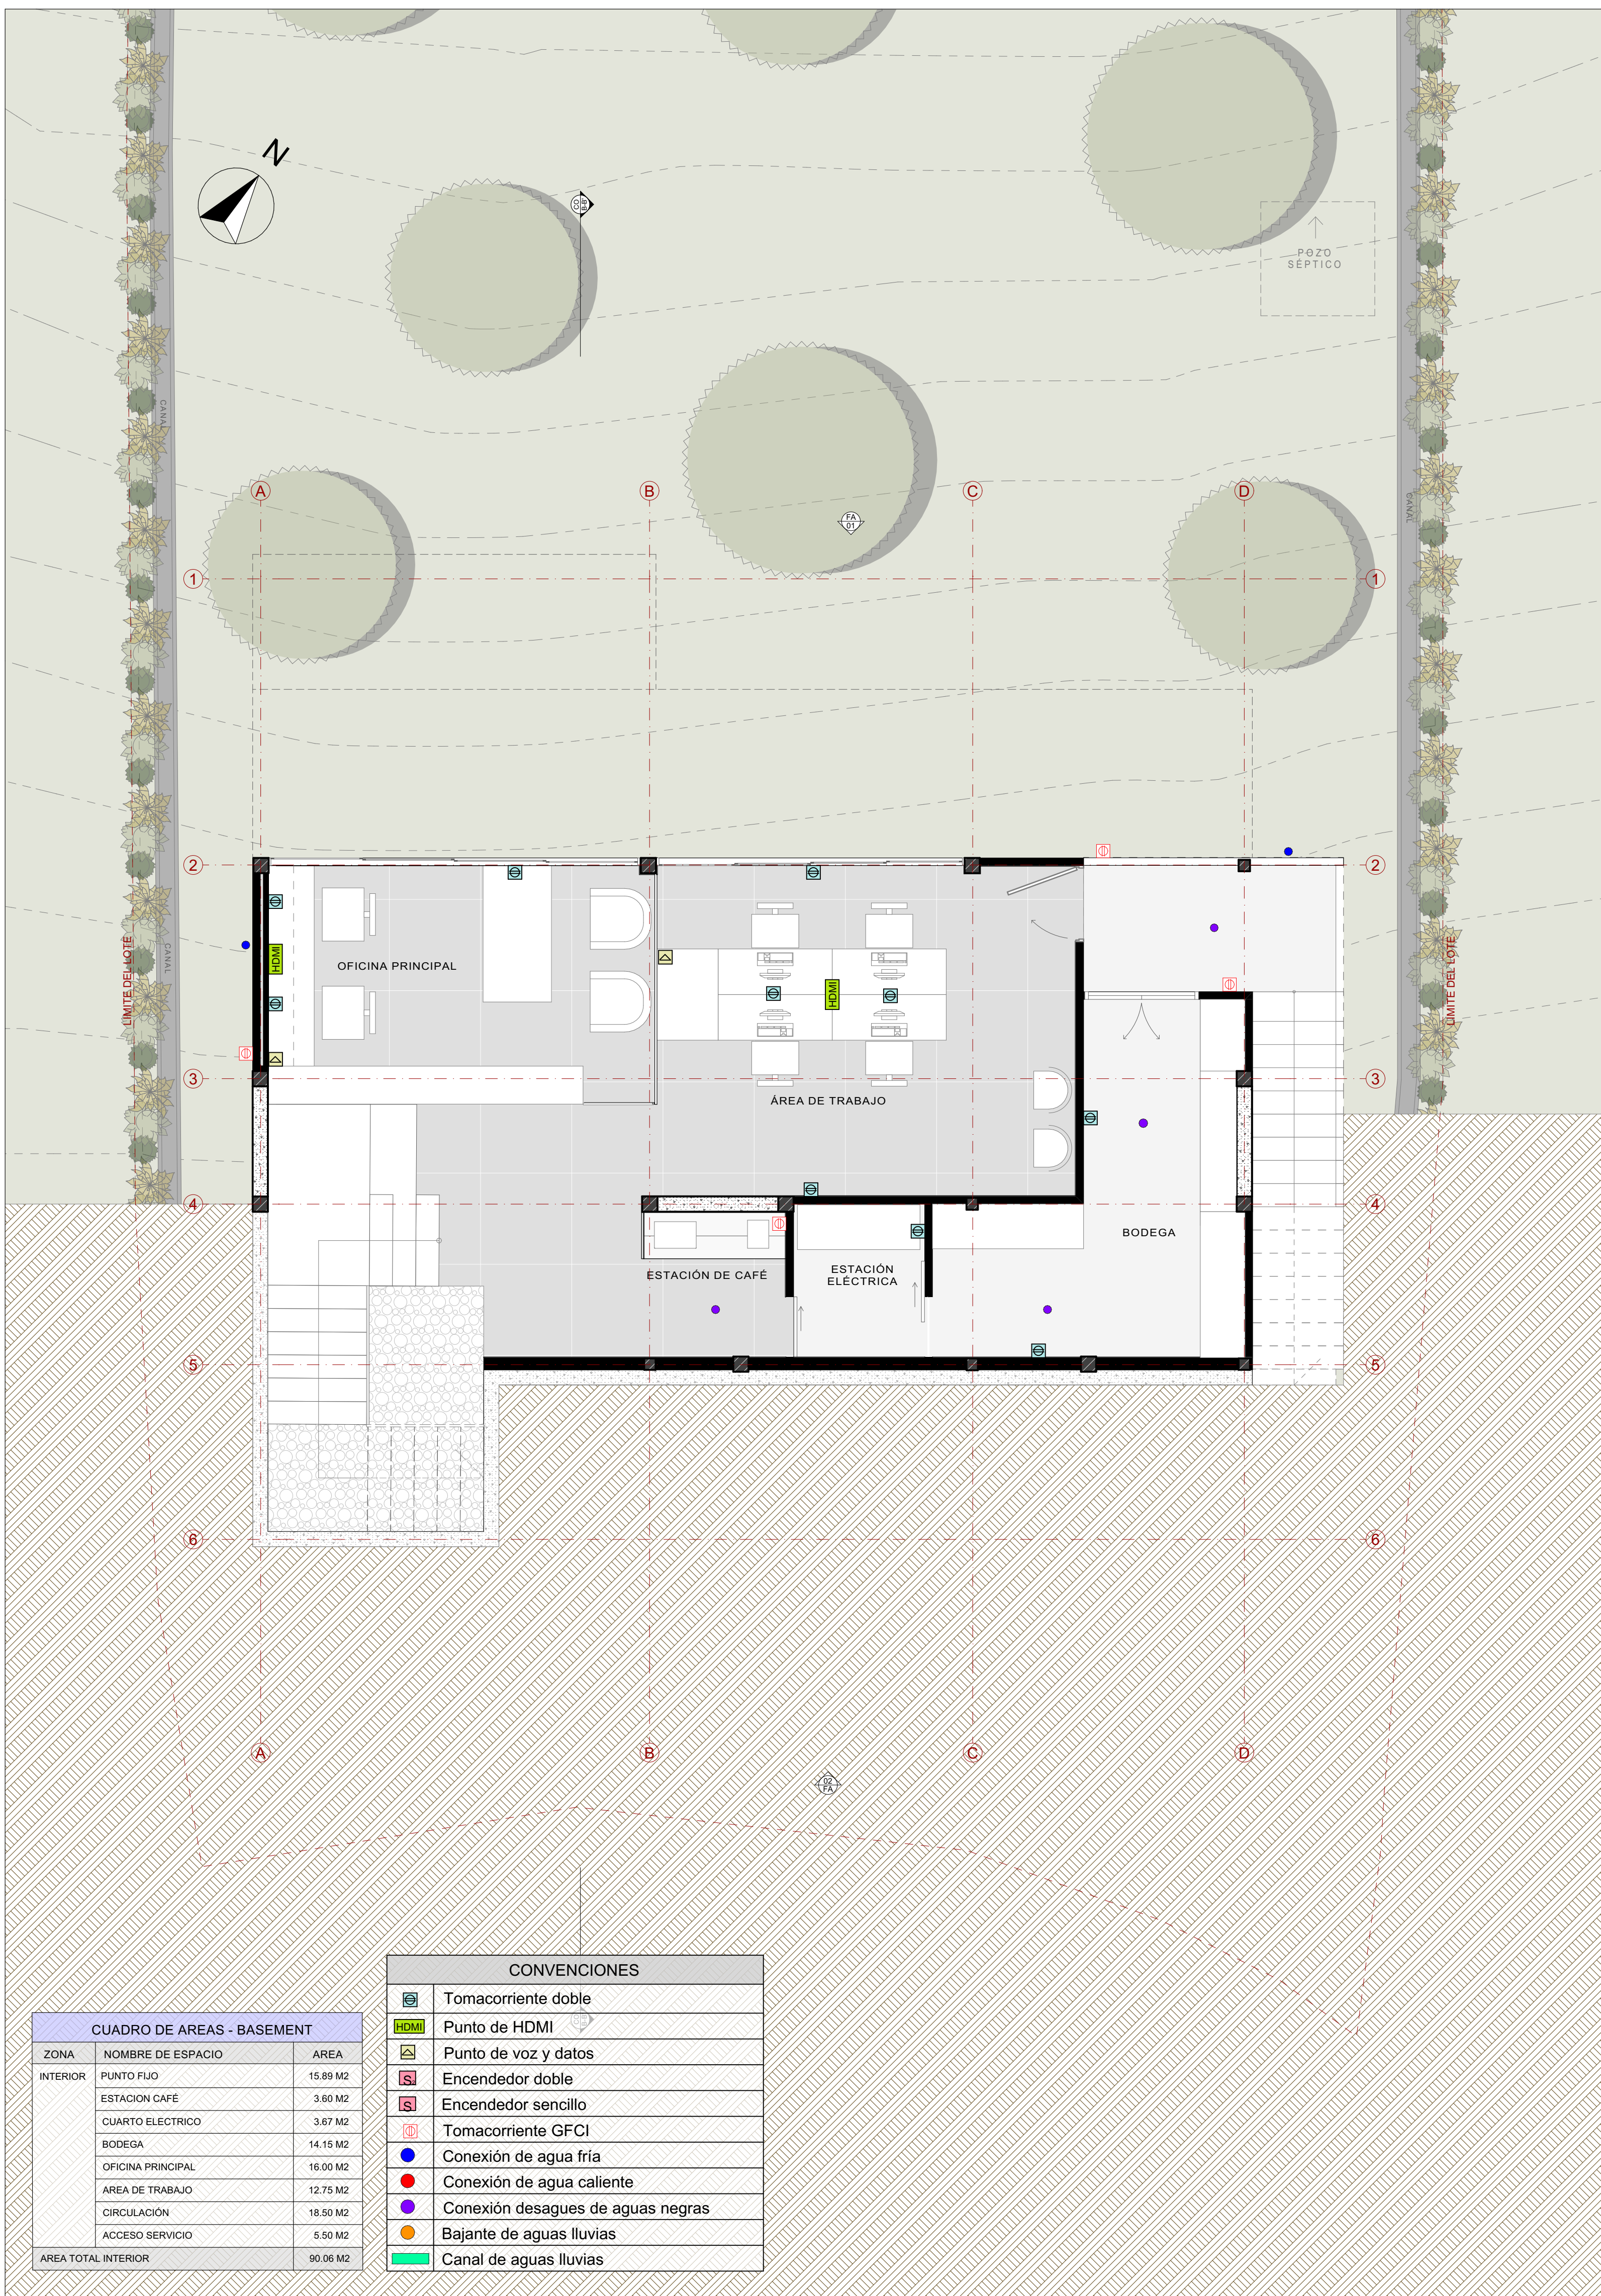

Plano de Primer Piso:

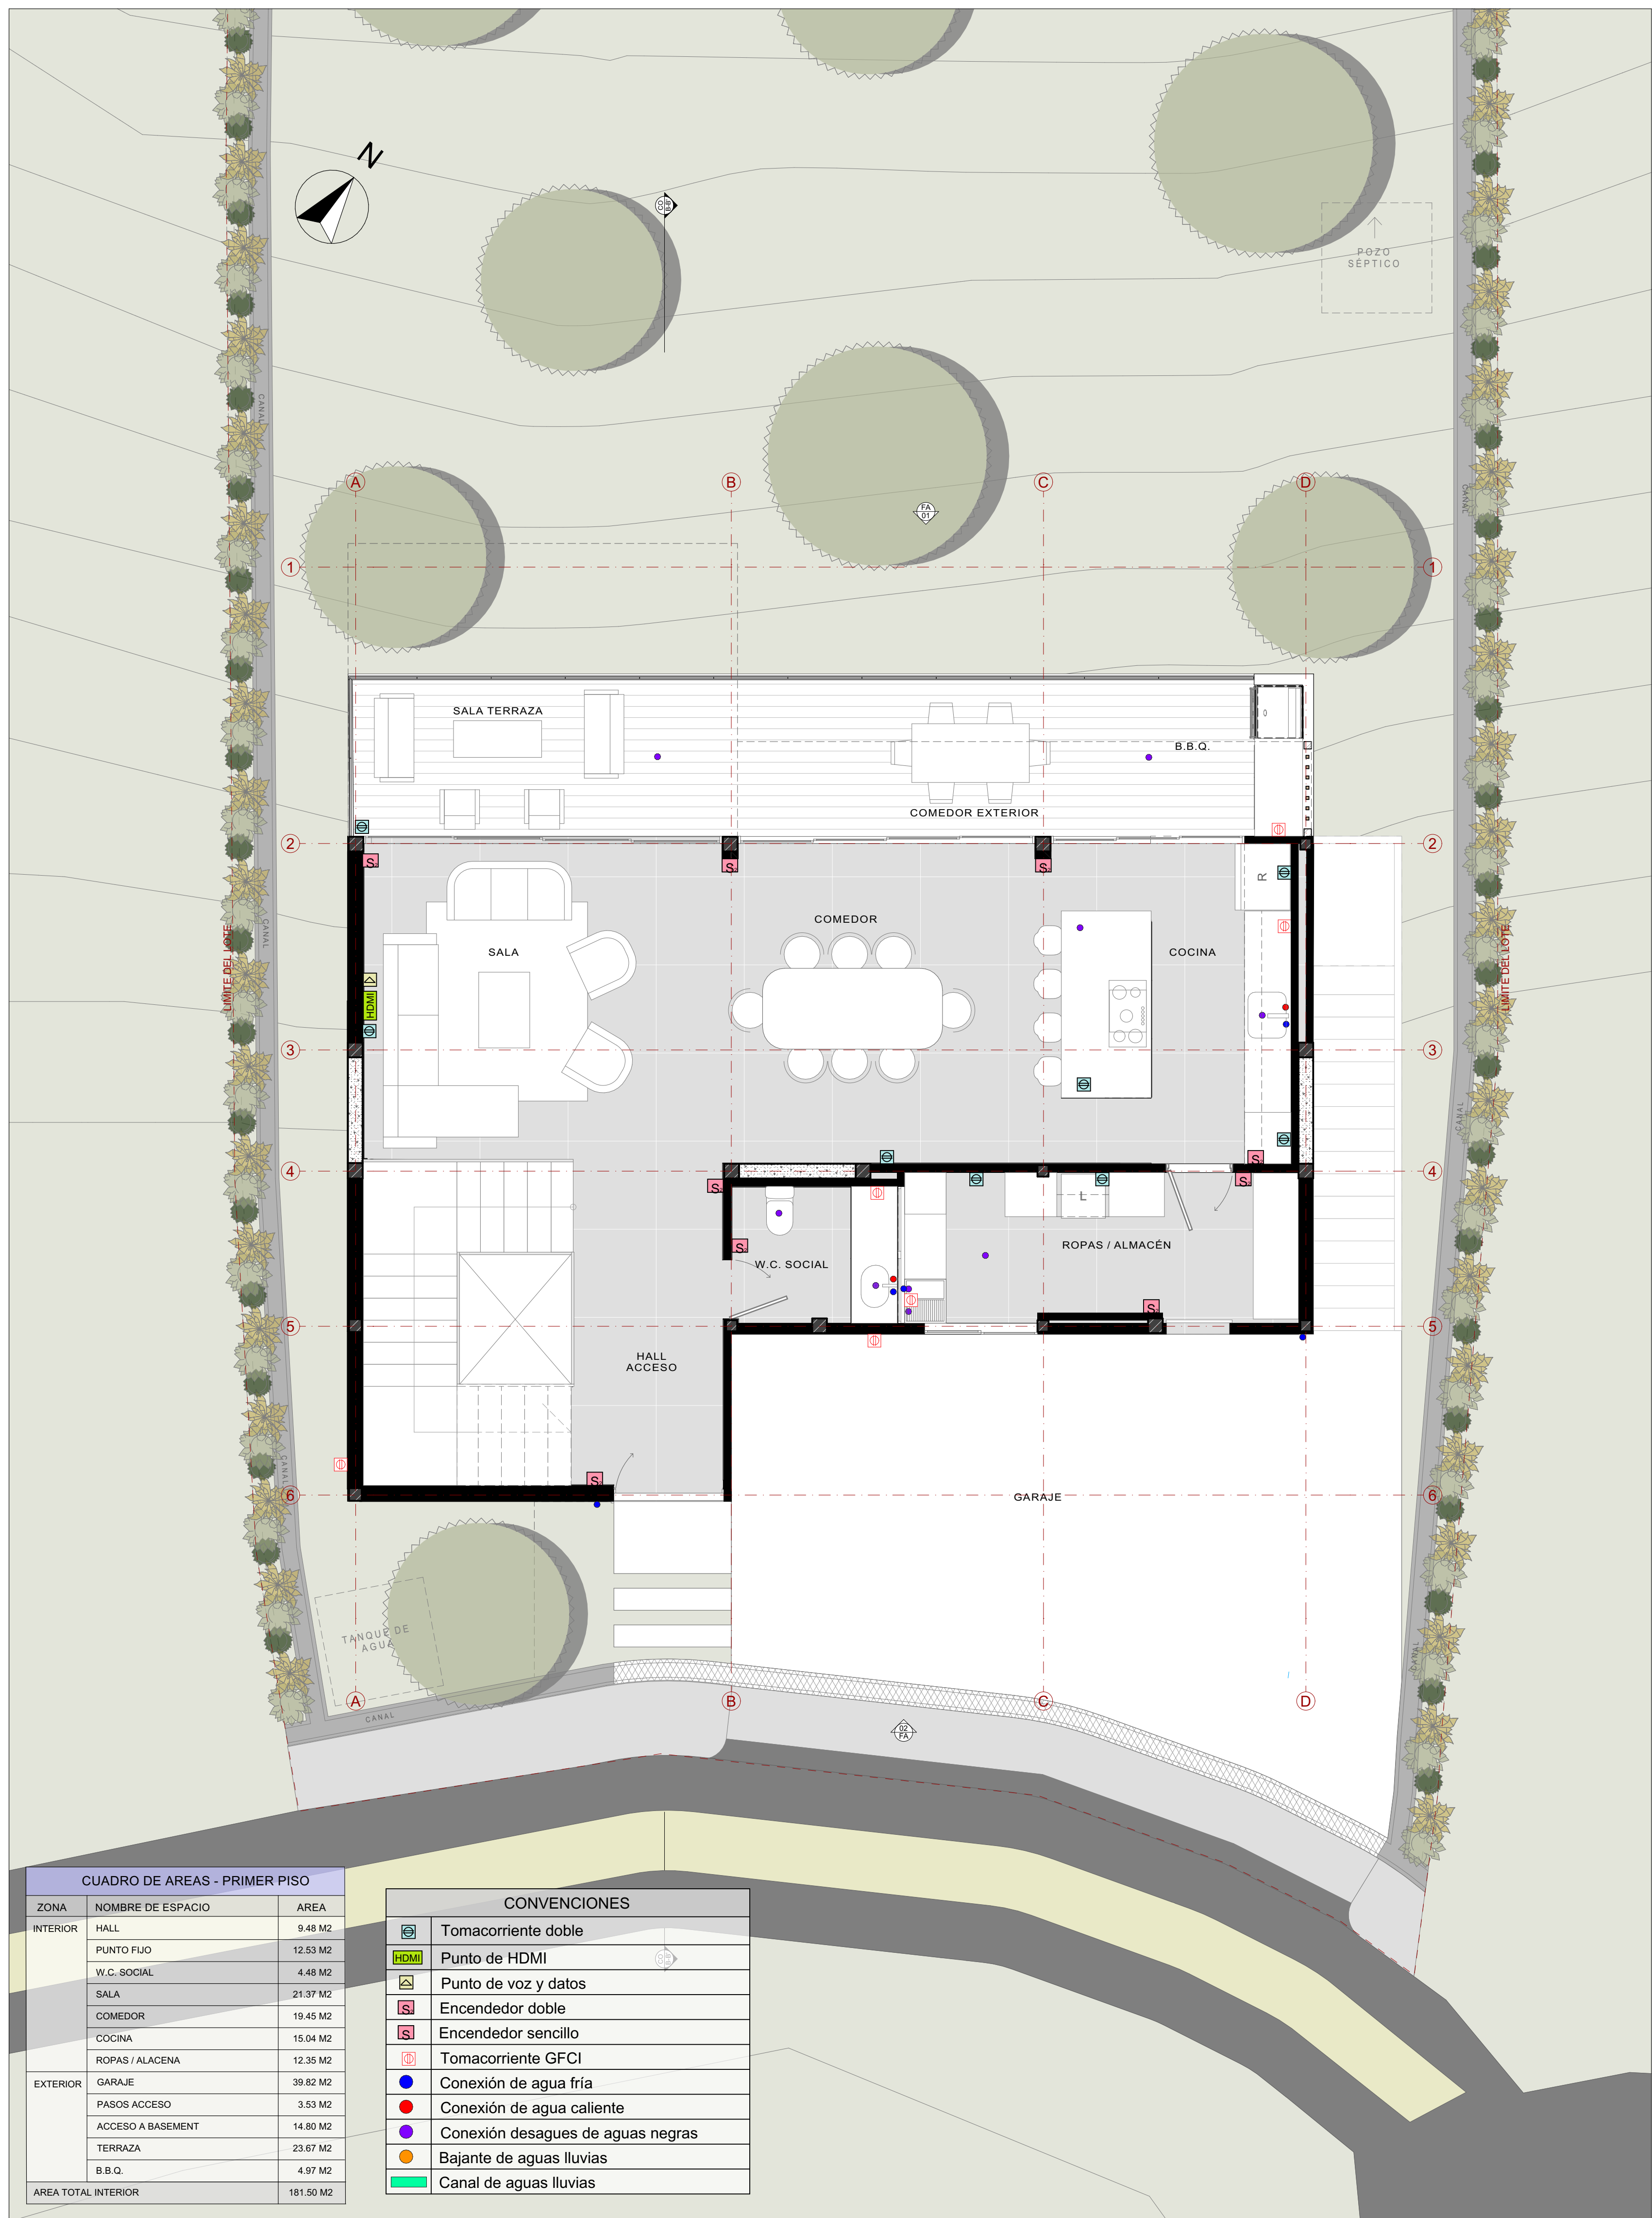

LIIT ARQUITECTURA

LOCALIZACION



DATOS DE PREDIO	
1	2
3	4
5	6
7	8
9	10
11	12
13	14
15	16
17	18
19	20
21	22
23	24
25	26
27	28
29	30
31	32
33	34
35	36
37	38
39	40
41	42
43	44
45	46
47	48
49	50
51	52
53	54
55	56
57	58
59	60
61	62
63	64
65	66
67	68
69	70
71	72
73	74
75	76
77	78
79	80
81	82
83	84
85	86
87	88
89	90
91	92
93	94
95	96
97	98
99	100

DIRECCION:

VILLA GUADALQUIVIR, LOTE 4-12,
FLORIDABLANCA

PROPIETARIOS

BRAYAN PÉREZ DELGADO
C.C. 1.098.810.706

DISEÑADOR

ARQ. JUAN SEBASTIAN SALAMANCA A
M.R. 630323019-1098742250

LIIT ARQUITECTURA

ACTUACION

PLANIMETRIAS ARQUITECTONICAS
PROYECTO DE VIVIENDA UNIFAMILIAR,
EN VILLA GUADALQUIVIR,
FLORIDABLANCA

CONTENIDC

- PLANO ARQUITECTÓNICO DE
INSTALACIONES GENERALES DEL
SÓTANO

- PLANO ARQUITECTÓNICO DE
INSTALACIONES GENERALES DEL PRIMER
PISO

NOTAS GENERALES

ESCALAS

1:50

28/11/2025

10 - PLANO ARQ. DE INSTALACIONES GENERALES

PLANO 10 DE 13