


PLANO ARQUITECTONICO DE INSTALACIONES GENERALES

Plano de Segundo Piso:



Plano de Cubiertas:

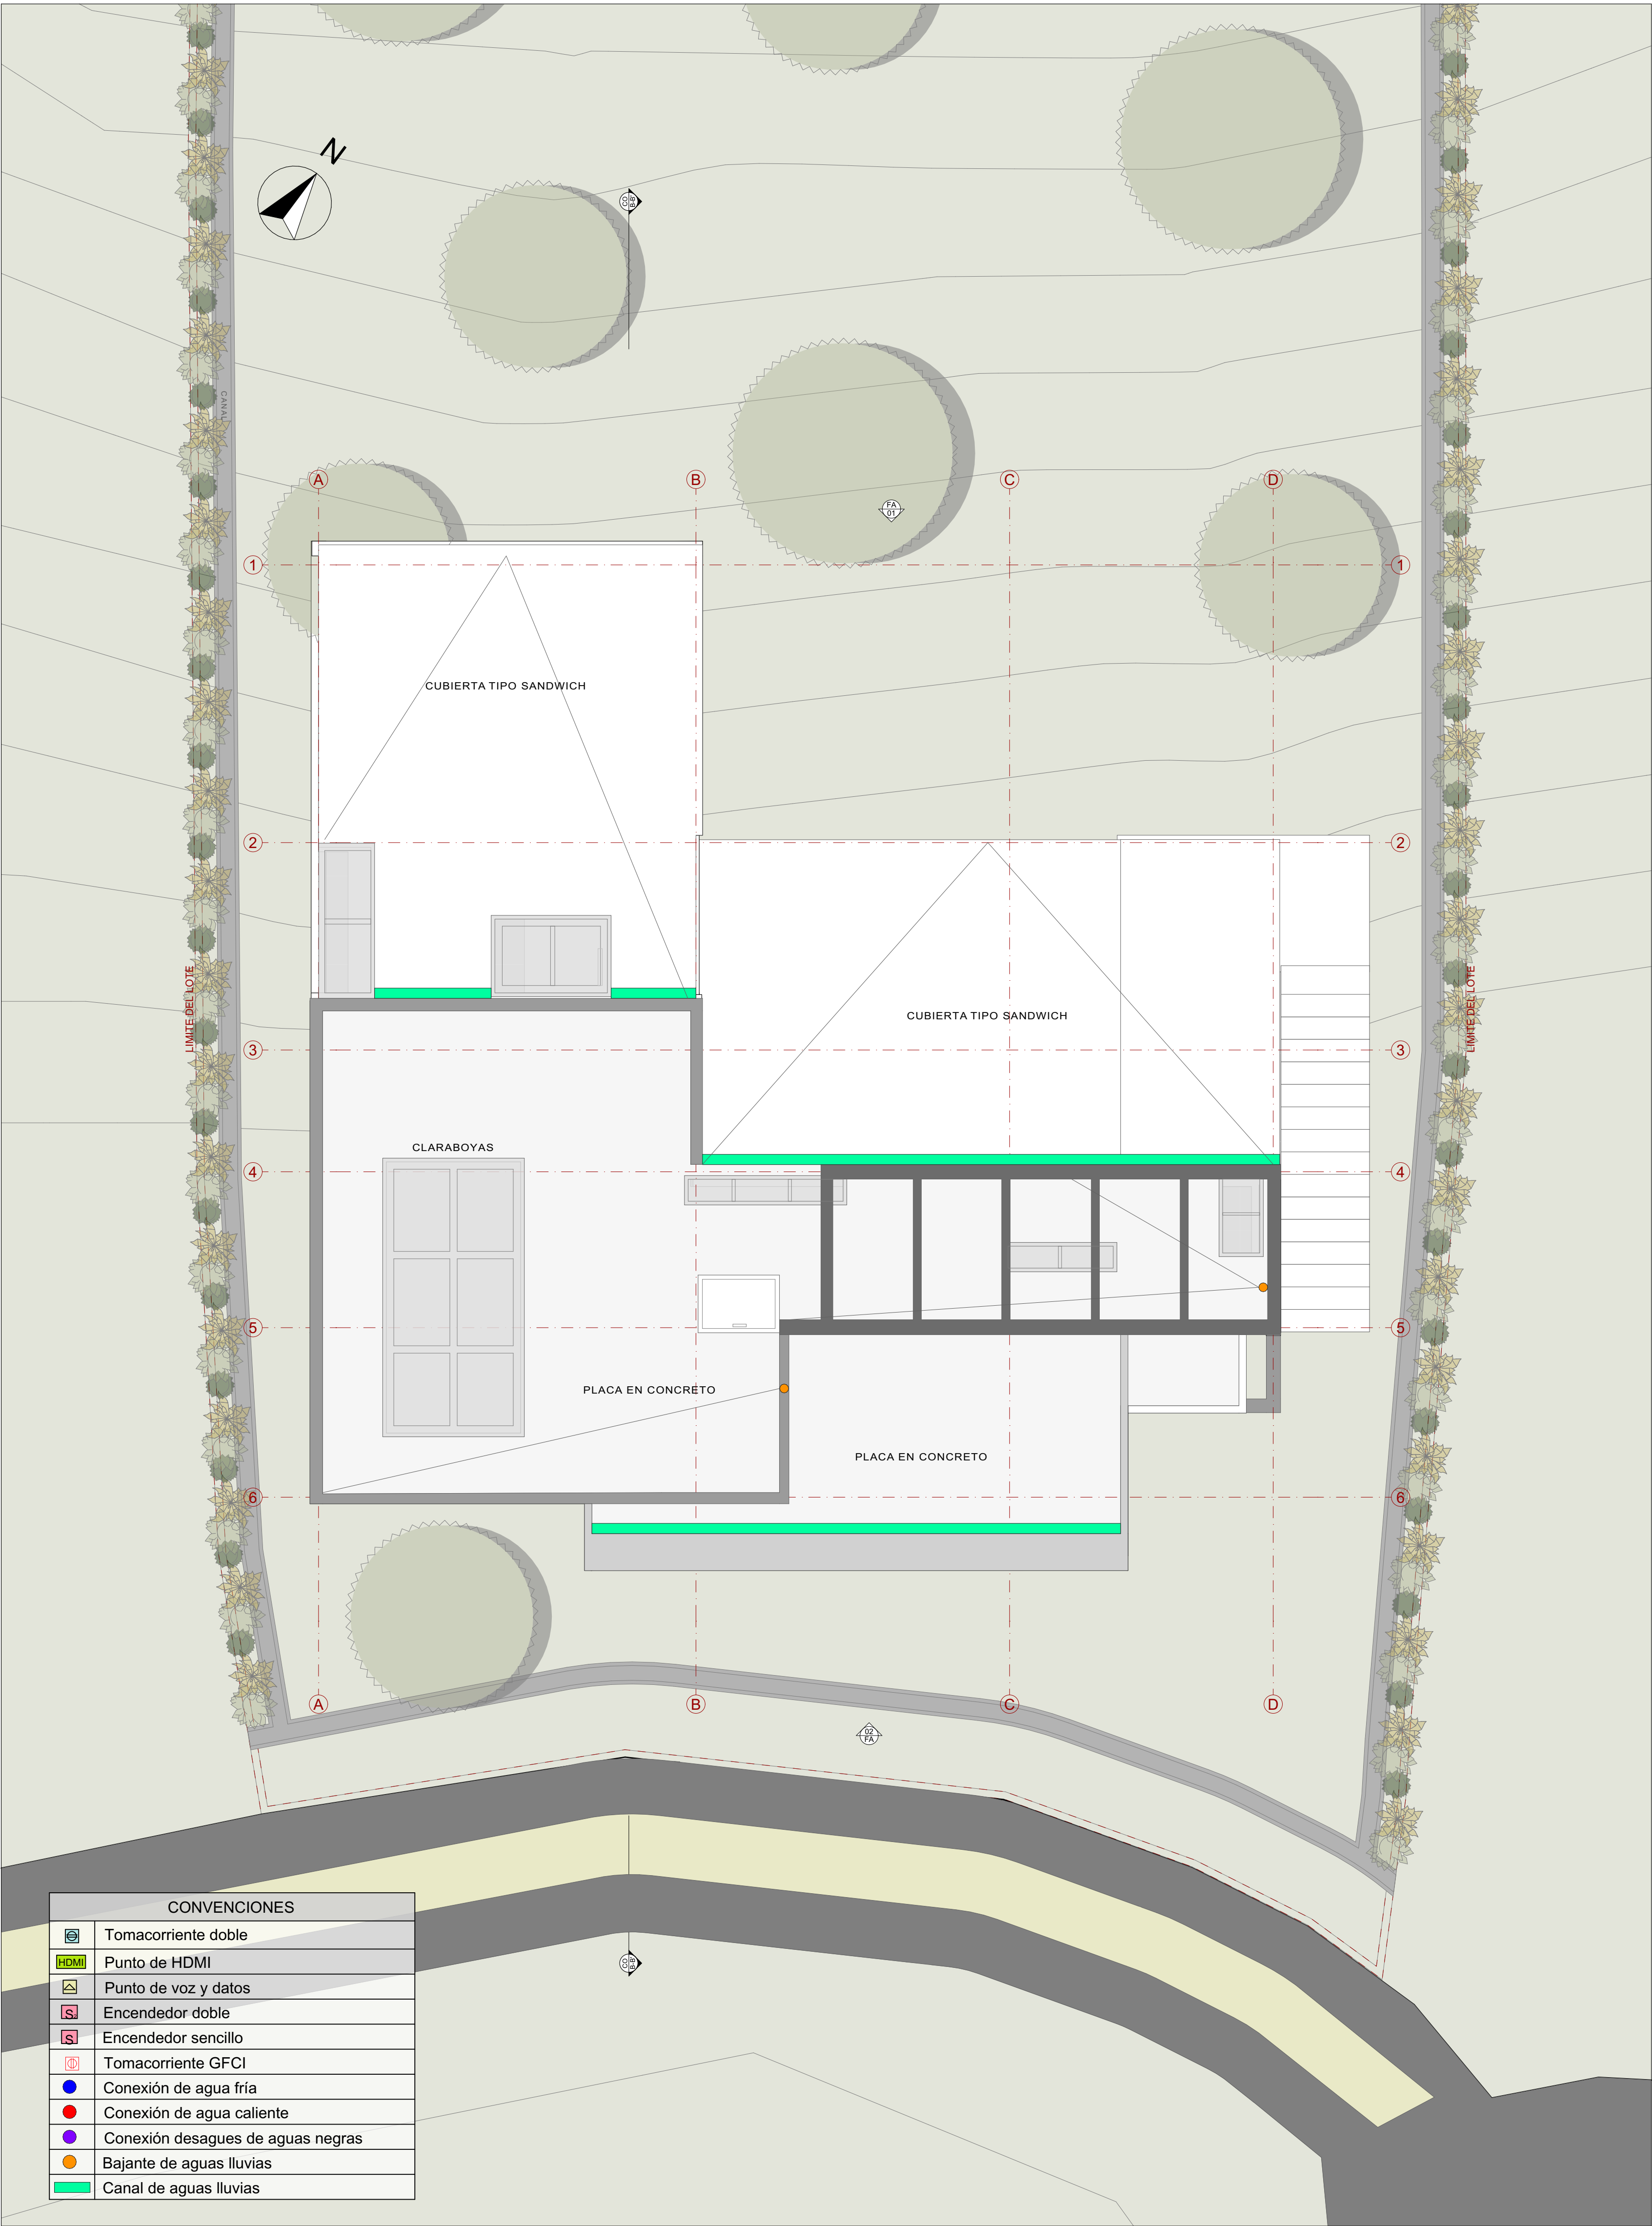

LIIT ARQUITECTURA

LOCALIZACION



DATOS DE PREDIO

DIRECCION:

VILLA GUADALQUIVIR, LOTE 4-12,
FLORIDABLANCA

PROPIETARIOS

BRAYAN PÉREZ DELGADO
C.C. 1.098.810.706

DISEÑADOR

ARQ. JUAN SEBASTIAN SALAMANCA ARDILA
M.P. A36322019-1098742250

LIIT ARQUITECTURA

ACTUACION

PLANIMETRÍAS ARQUITECTÓNICAS
PROYECTO DE VIVIENDA UNIFAMILIAR,
EN VILLA GUADALQUIVIR,
FLORIDABLANCA

CONTENIDO

- PLANO ARQUITECTÓNICO DE
INSTALACIONES GENERALES DEL
SEGUNDO PISO

NOTAS GENERALES

ESCALAS

1:50

28/11/2025

11 - PLANO ARQ. DE
INSTALACIONES GENERALES