



Plano del Primero Piso:

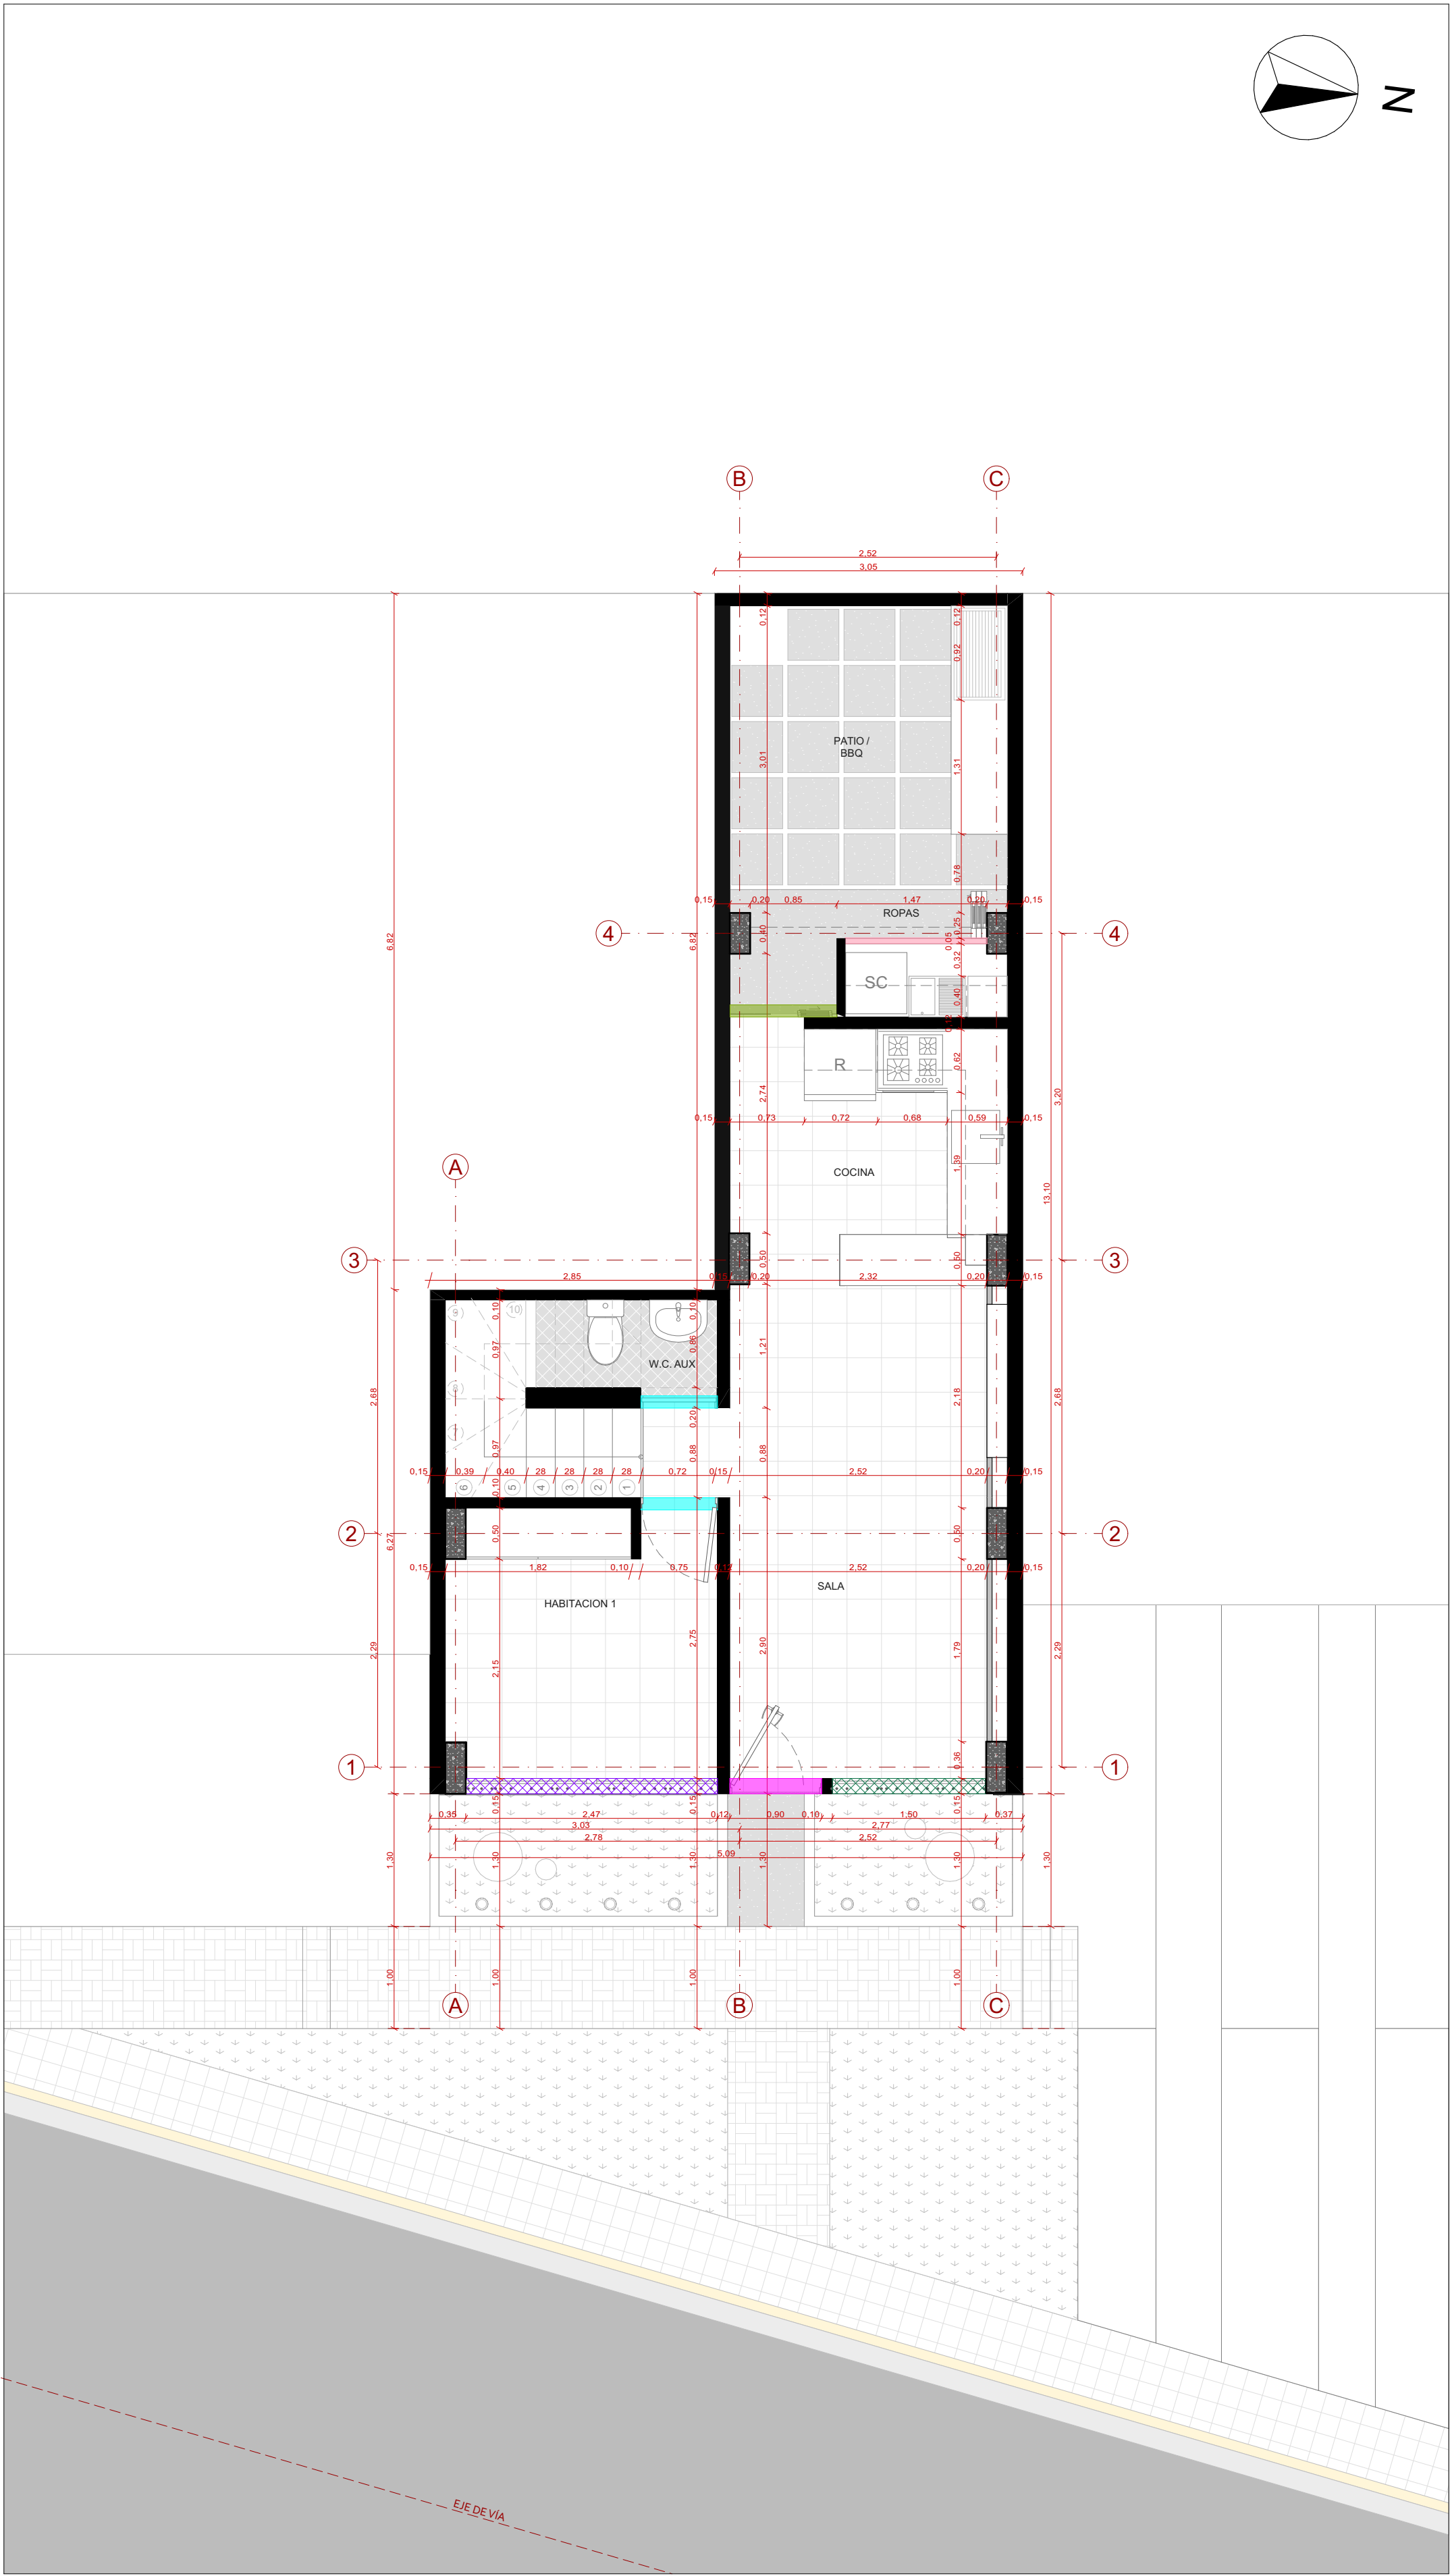


VT - 01	VT - 02	PTA - 01	PTA - 02	PTA - 03	PTA - 04
Ventana en aluminio color de preferencia, dimensiones 1.70x1.45 m	Ventana en aluminio color de preferencia, dimensiones 1.70x1.45 m	Puerta en madera reforzada, con cerradura en aluminio y dimensiones 0.90x2.10 m	Puerta en madera con cerradura en aluminio y dimensiones 0.75x2.10 m	Puerta en aluminio con vidrio corrediza en 3 tramos de 2.10x1.00m	Puerta en madera tipo rejilla plegable de 3 tramos y dimensiones de 2.0x1.4m

Plano del Segundo Piso:

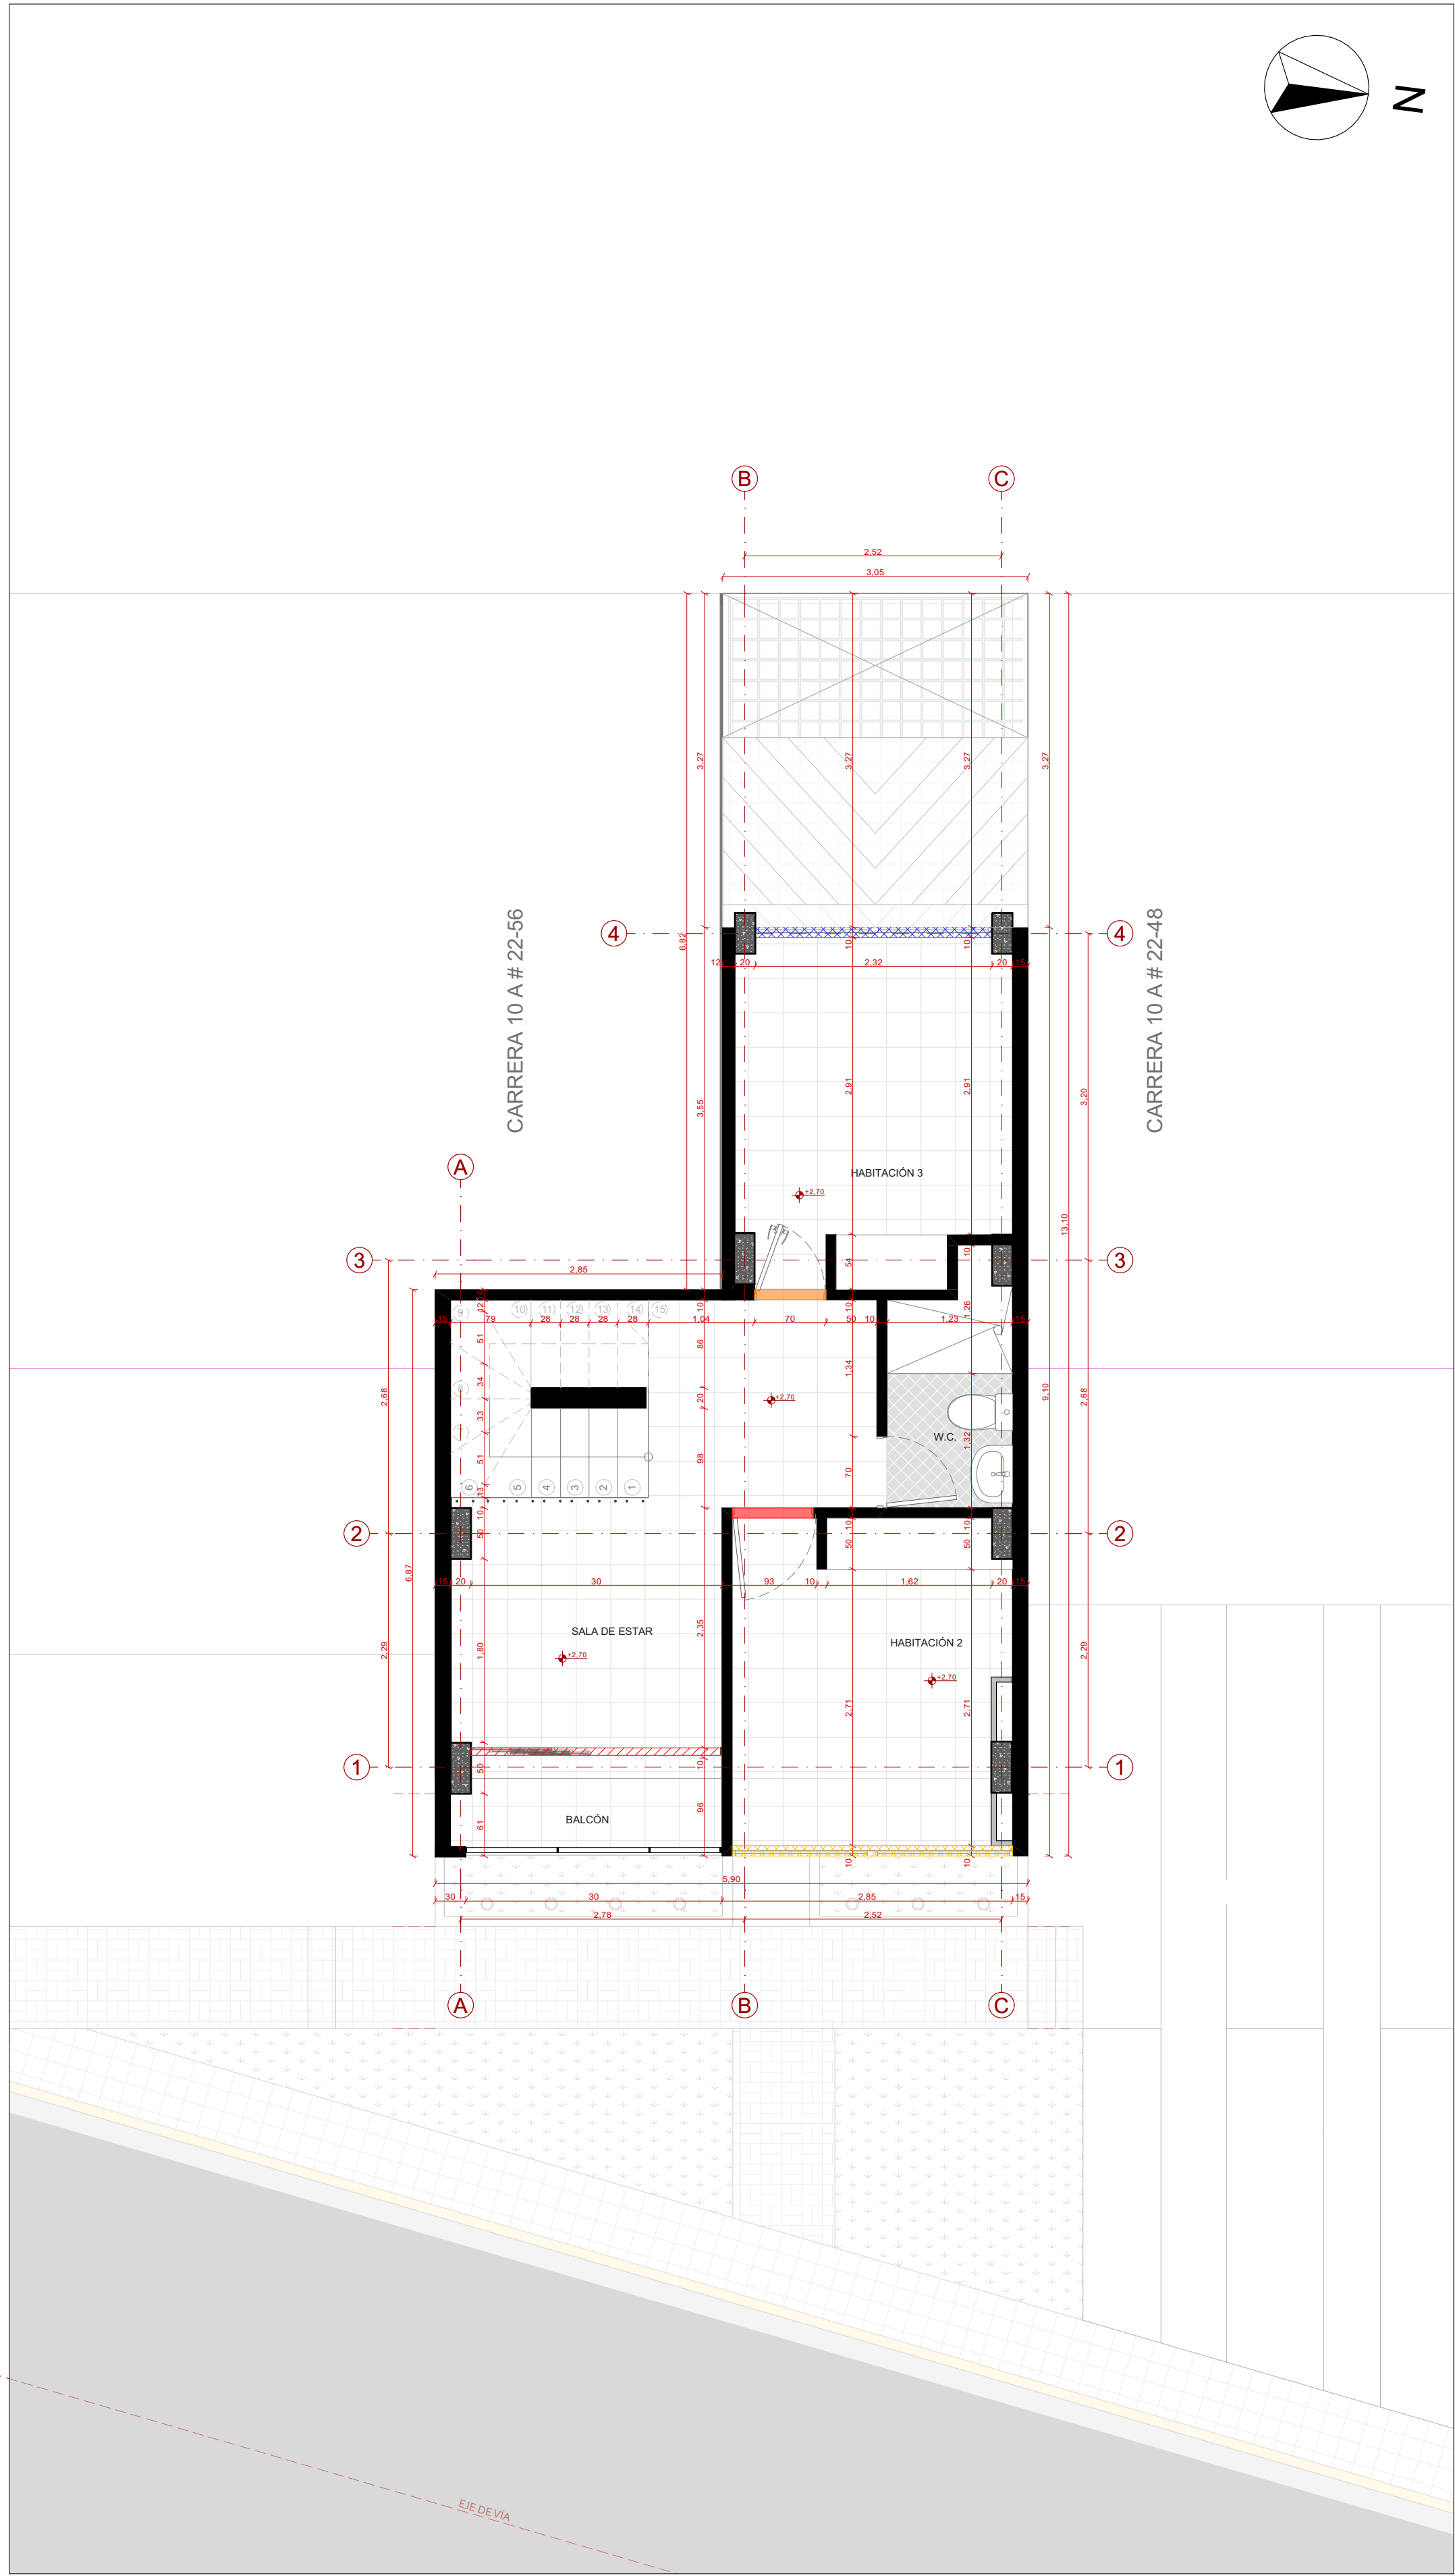

VT - 01	VT - 02	PTA VT - 01	PTA - 01	PTA - 02
Ventana en aluminio color de preferencia, dimensiones 2.70x1.75 m	Ventana en aluminio color de preferencia, dimensiones 2.70x2.30 m	Puerta ventana en aluminio color de preferencia, dimensiones 2.50x2.45 m	Puerta en madera color de preferencia, dimensiones 2.10x0.80 m	Puerta en madera color de preferencia, dimensiones 2.10x0.70 m

Plano del Tercer Piso:

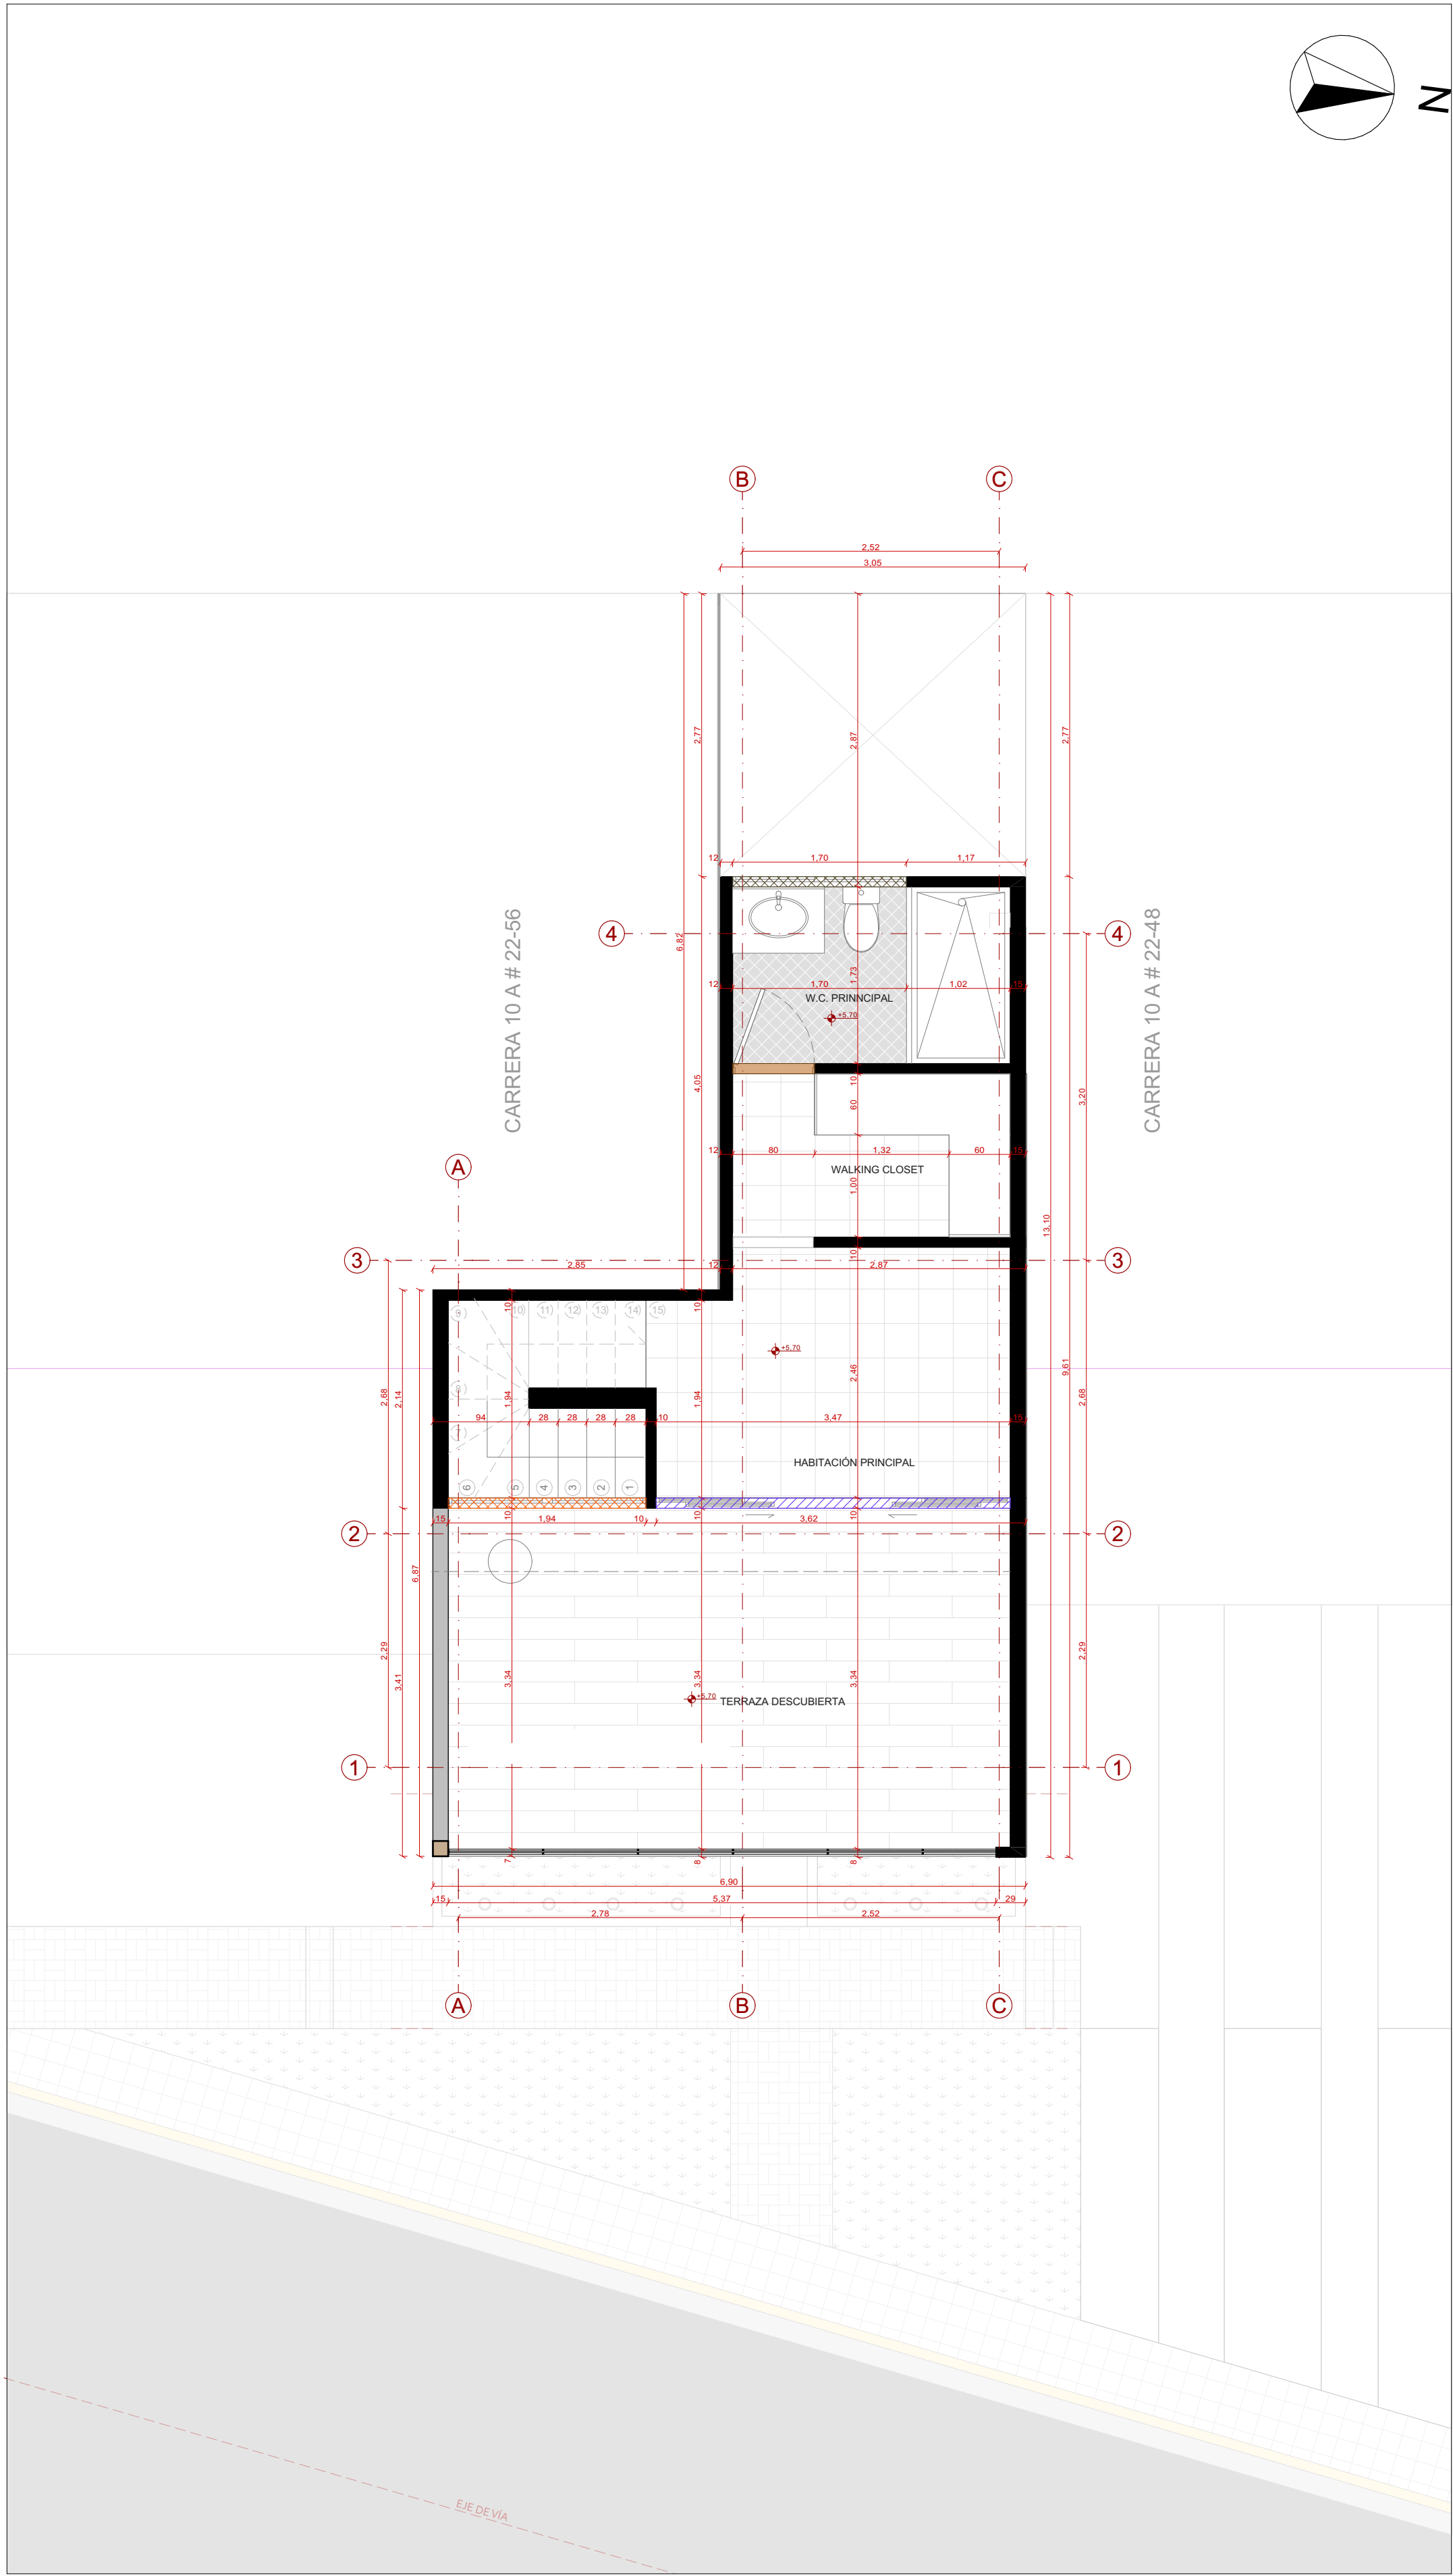

VT - 01	VT - 02	PTA VT - 01	PTA - 01
Ventana fija en aluminio color de preferencia, dimensiones 1.50x1.90 m	Ventana fija en aluminio color de preferencia, dimensiones 1.50x1.90 m	Puerta ventana en aluminio color de preferencia, dimensiones 2.50x2.45 m	Puerta en madera color de preferencia, dimensiones 2.10x0.80 m