



PROYECTO DE REMODELACIÓN Y AMPLIACIÓN FABRICA LA TOULoust, BUCARAMANGA

PLANO DE ACABADOS Y ESPECIFICACIONES GENERALES

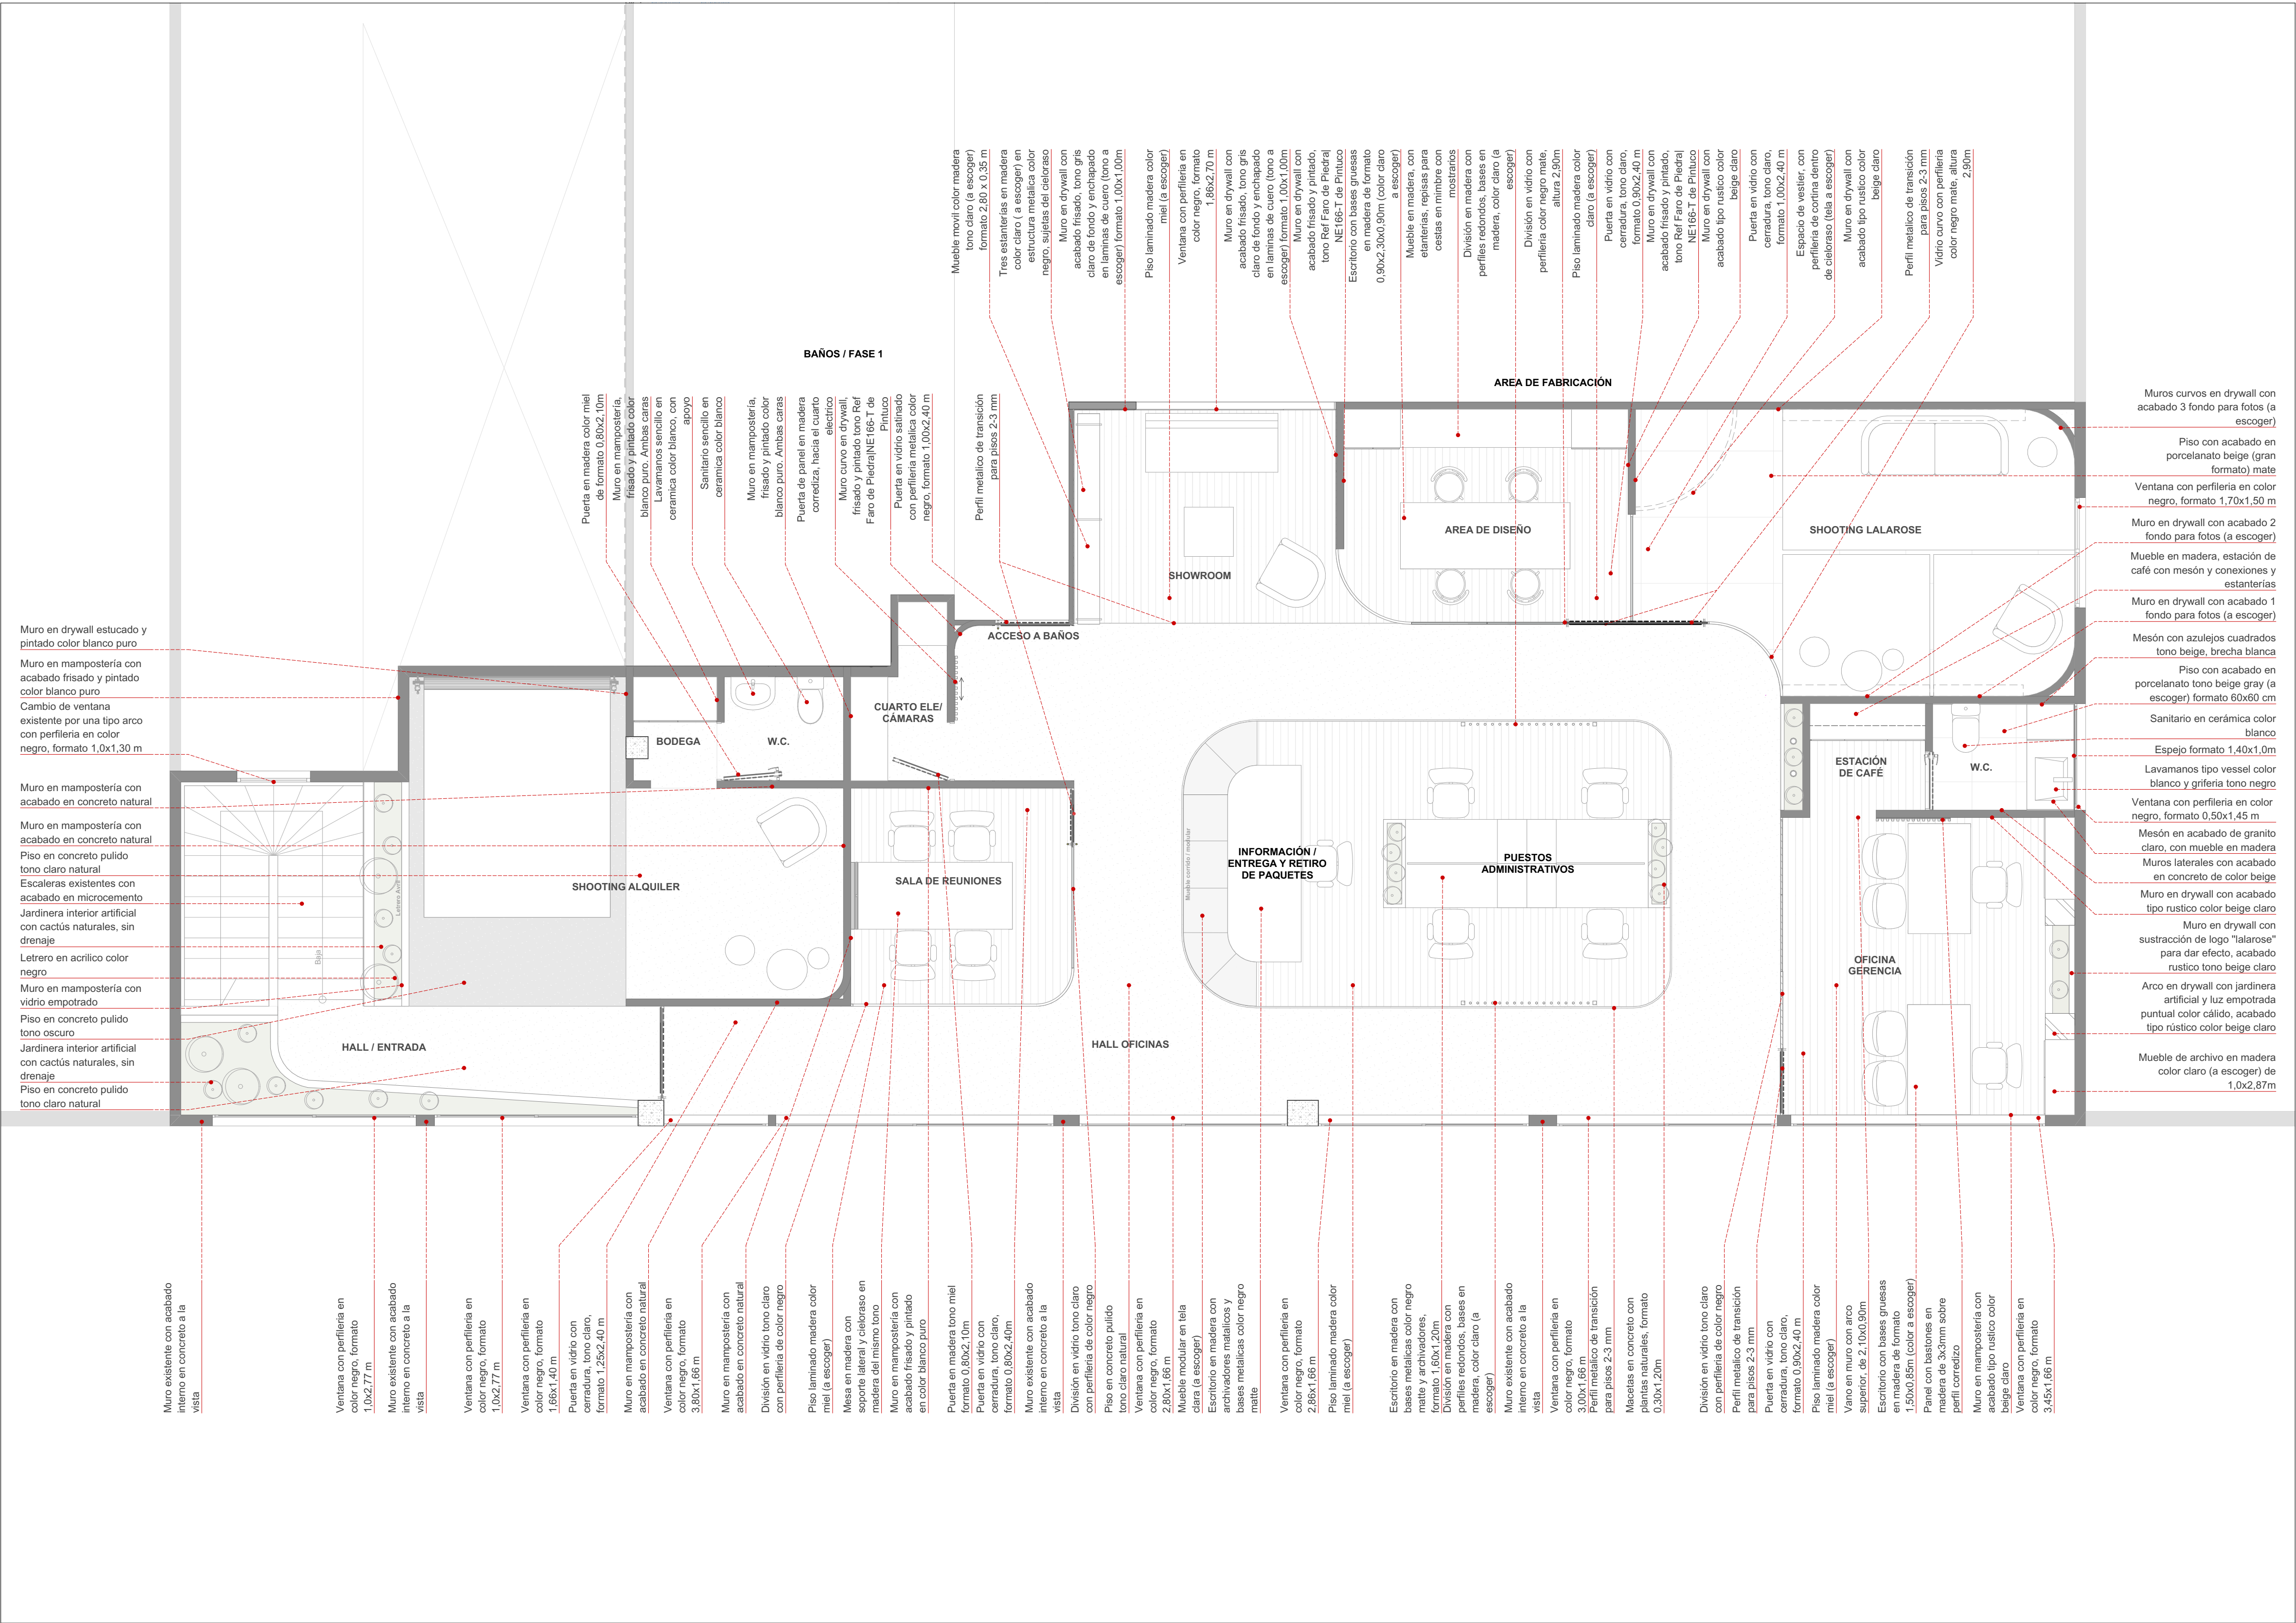

LOCALIZACION

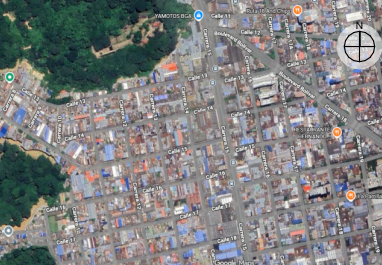

DATOS DE PREDIO

DIRECCION:
CARRERA 14 # 14-40, BUCARAMANGA

PROPIETARIOS

LAURA TOLOZA
JEAN CHACÓN

DISEÑADOR

ARQ. JUAN SEBASTIAN SALAMANCA-AVELLA
M.P. A30322019-1098742290

ARQ. SEBASTIAN SALAMANCA

ACTUACION

PLANIMETRÍAS ARQUITECTONICAS
PROYECTO LA TOULoust,
BUCARAMANGA

CONTENIDO

- PLANO DE ACABADOS Y
ESPECIFICACIONES GENERALES

NOTAS GENERALES

ESCALA

1:50

13/02/2026