

PROYECTO DE REMODELACIÓN Y AMPLIACIÓN FABRICA LA TOULoust, BUCARAMANGA

PLANO GENERAL DE INSTALACIONES



LIIT

ARQUITECTURA

LOCALIZACION

DATOS DE PREDIO

DIRECCION:  
CARRERA 14 # 14-40, BUCARAMANGA

PROPIETARIOS

LAURA TOLOZA  
JEAN CHACÓN

DISEÑADOR

ARQ. JUAN SEBASTIÁN SALAMANCA AVILA  
M.P. A30322019-1098742290

ARQ. SEBASTIAN SALAMANCA

ACTUACION

PLANIMETRÍAS ARQUITECTONICAS  
PROYECTO LA TOULoust,  
BUCARAMANGA

CONTENIDO

- PLANO GENERAL DE INSTALACIONES  
- PLANO GENERAL DE ILUMINACIÓN Y CIELORASOS

NOTAS GENERALES


ESCALA

1:50

13/02/2026

PLANO 4 DE 6

PLANO GENERAL DE ILUMINACIÓN Y CIELORASOS

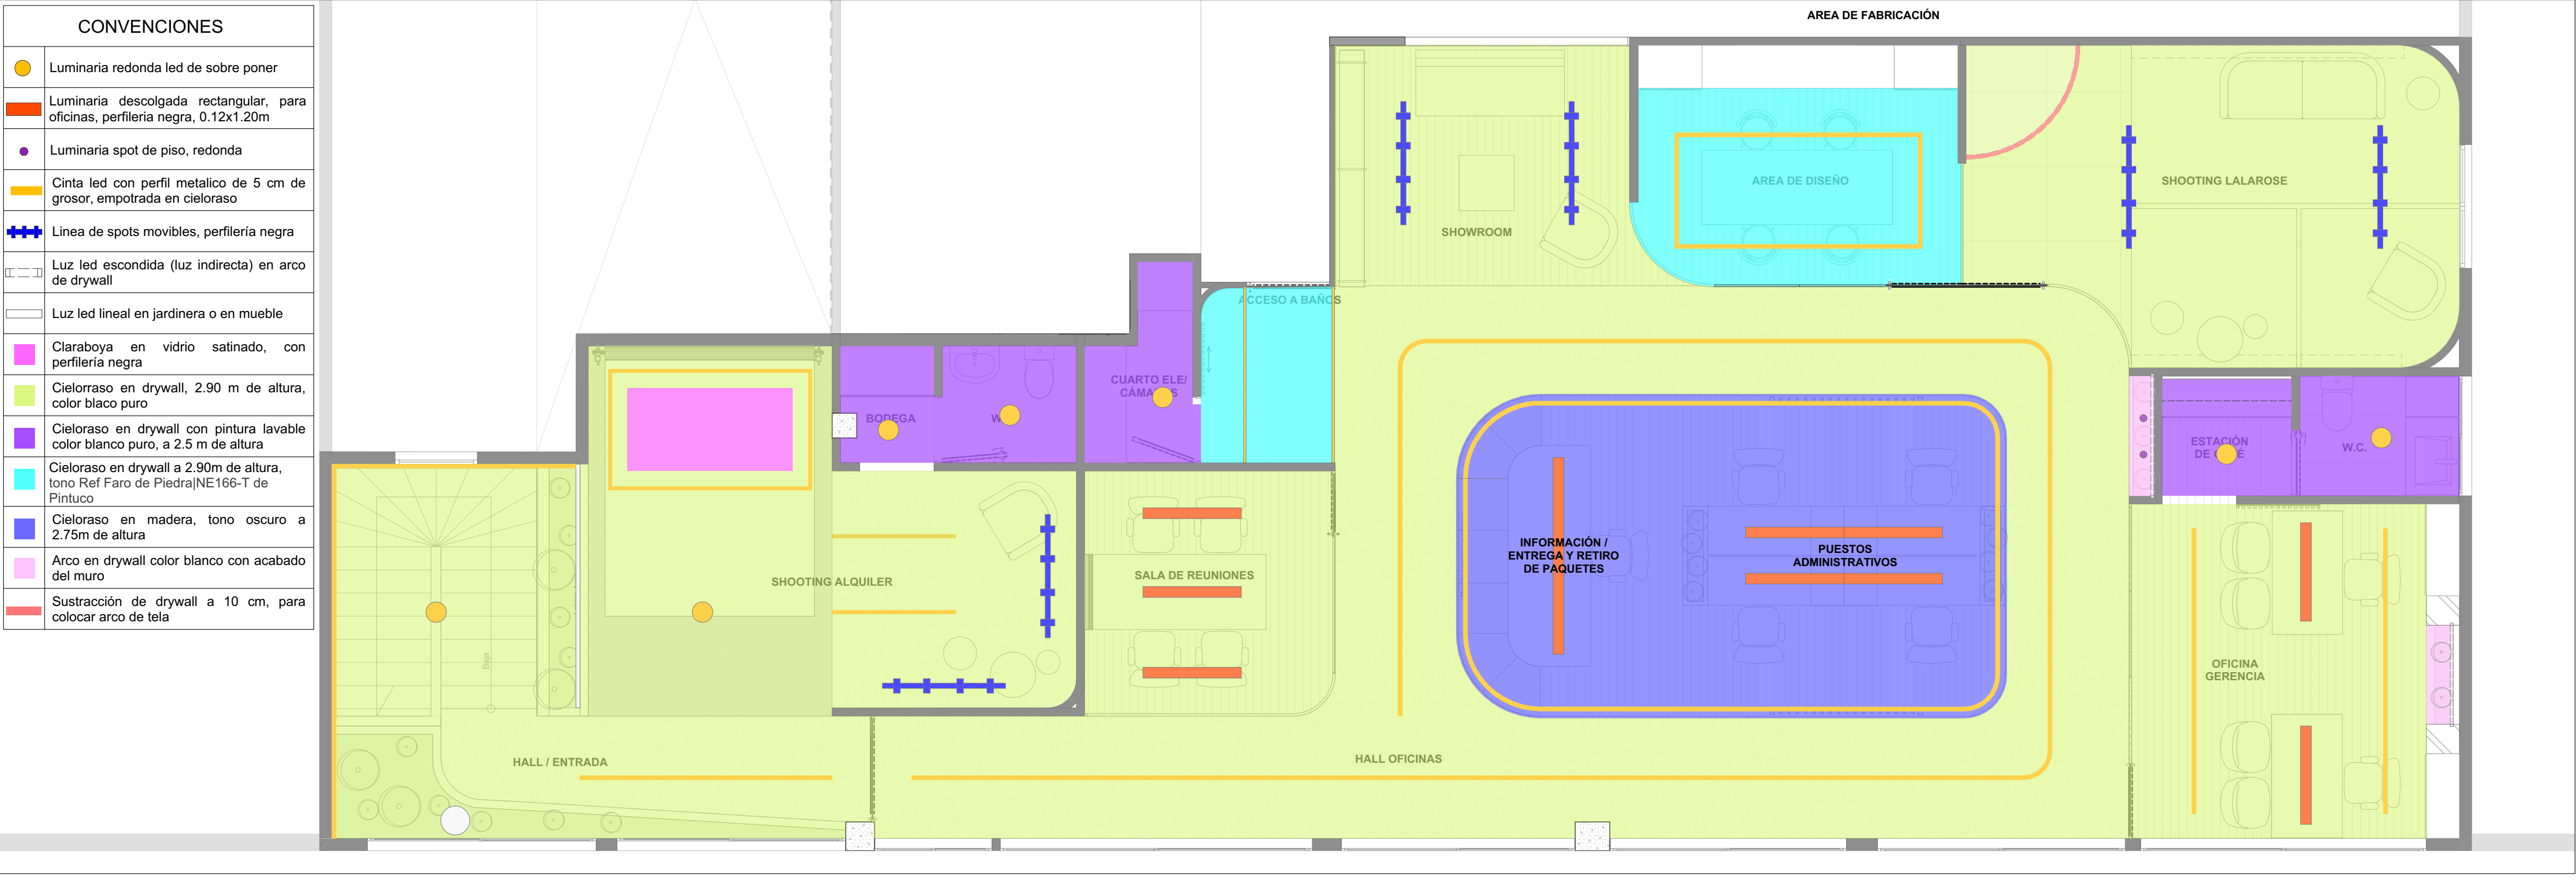

LIIT

ARQUITECTURA

LOCALIZACION

DATOS DE PREDIO

DIRECCION:  
CARRERA 14 # 14-40, BUCARAMANGA

PROPIETARIOS

LAURA TOLOZA  
JEAN CHACÓN

DISEÑADOR

ARQ. JUAN SEBASTIÁN SALAMANCA AVILA  
M.P. A30322019-1098742290

ARQ. SEBASTIAN SALAMANCA

ACTUACION

PLANIMETRÍAS ARQUITECTONICAS  
PROYECTO LA TOULoust,  
BUCARAMANGA

CONTENIDO

- PLANO GENERAL DE INSTALACIONES  
- PLANO GENERAL DE ILUMINACIÓN Y CIELORASOS

NOTAS GENERALES

ESCALA

1:50

13/02/2026

PLANO 4 DE 6