


PLANO DE PRIMER PISO CON COTAS GENERALES - PROYECTO PARCELA TOLOZA JIMENEZ

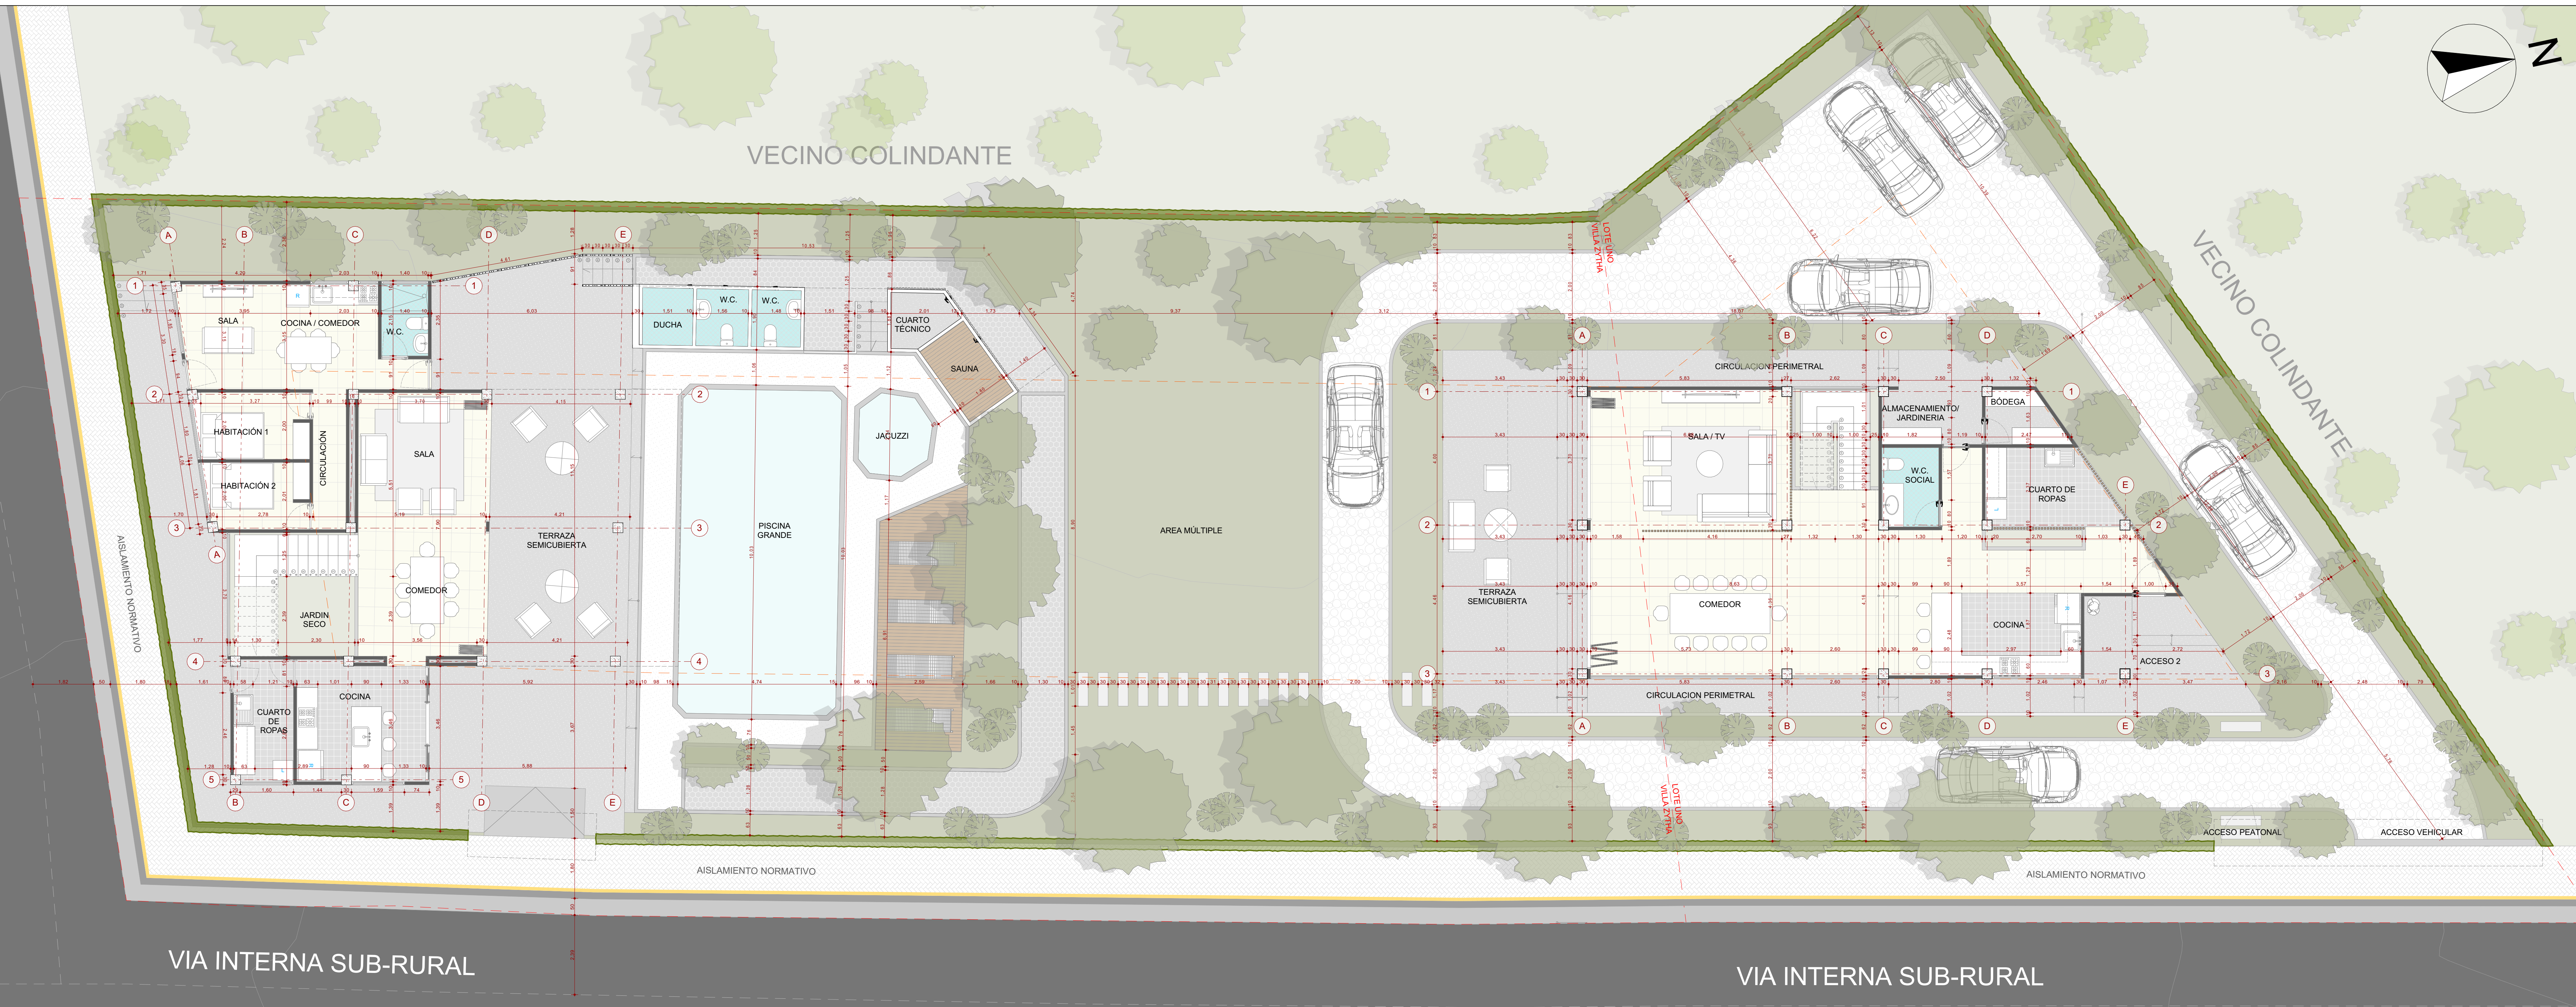

PLANO DE SEGUNDO PISO CON COTAS GENERALES - PROYECTO PARCELA TOLOZA JIMENEZ

