

PLANO Nº:
6/10

PROYECTO:
LIIT ARQUITECTURA

FECHA:
06/06/2025

ESCALA:

CONTENIDO:

Plano General de Iluminación y Cielorastos


Proyecto Parcela Tolosa Jimenez

Piedecuesta, Santander

LIIT

ARQUITECTURA

PLANO DE PRIMER PISO CON ILUMINACION Y CIELORASTOS - PROYECTO PARCELA TOLOZA JIMENEZ

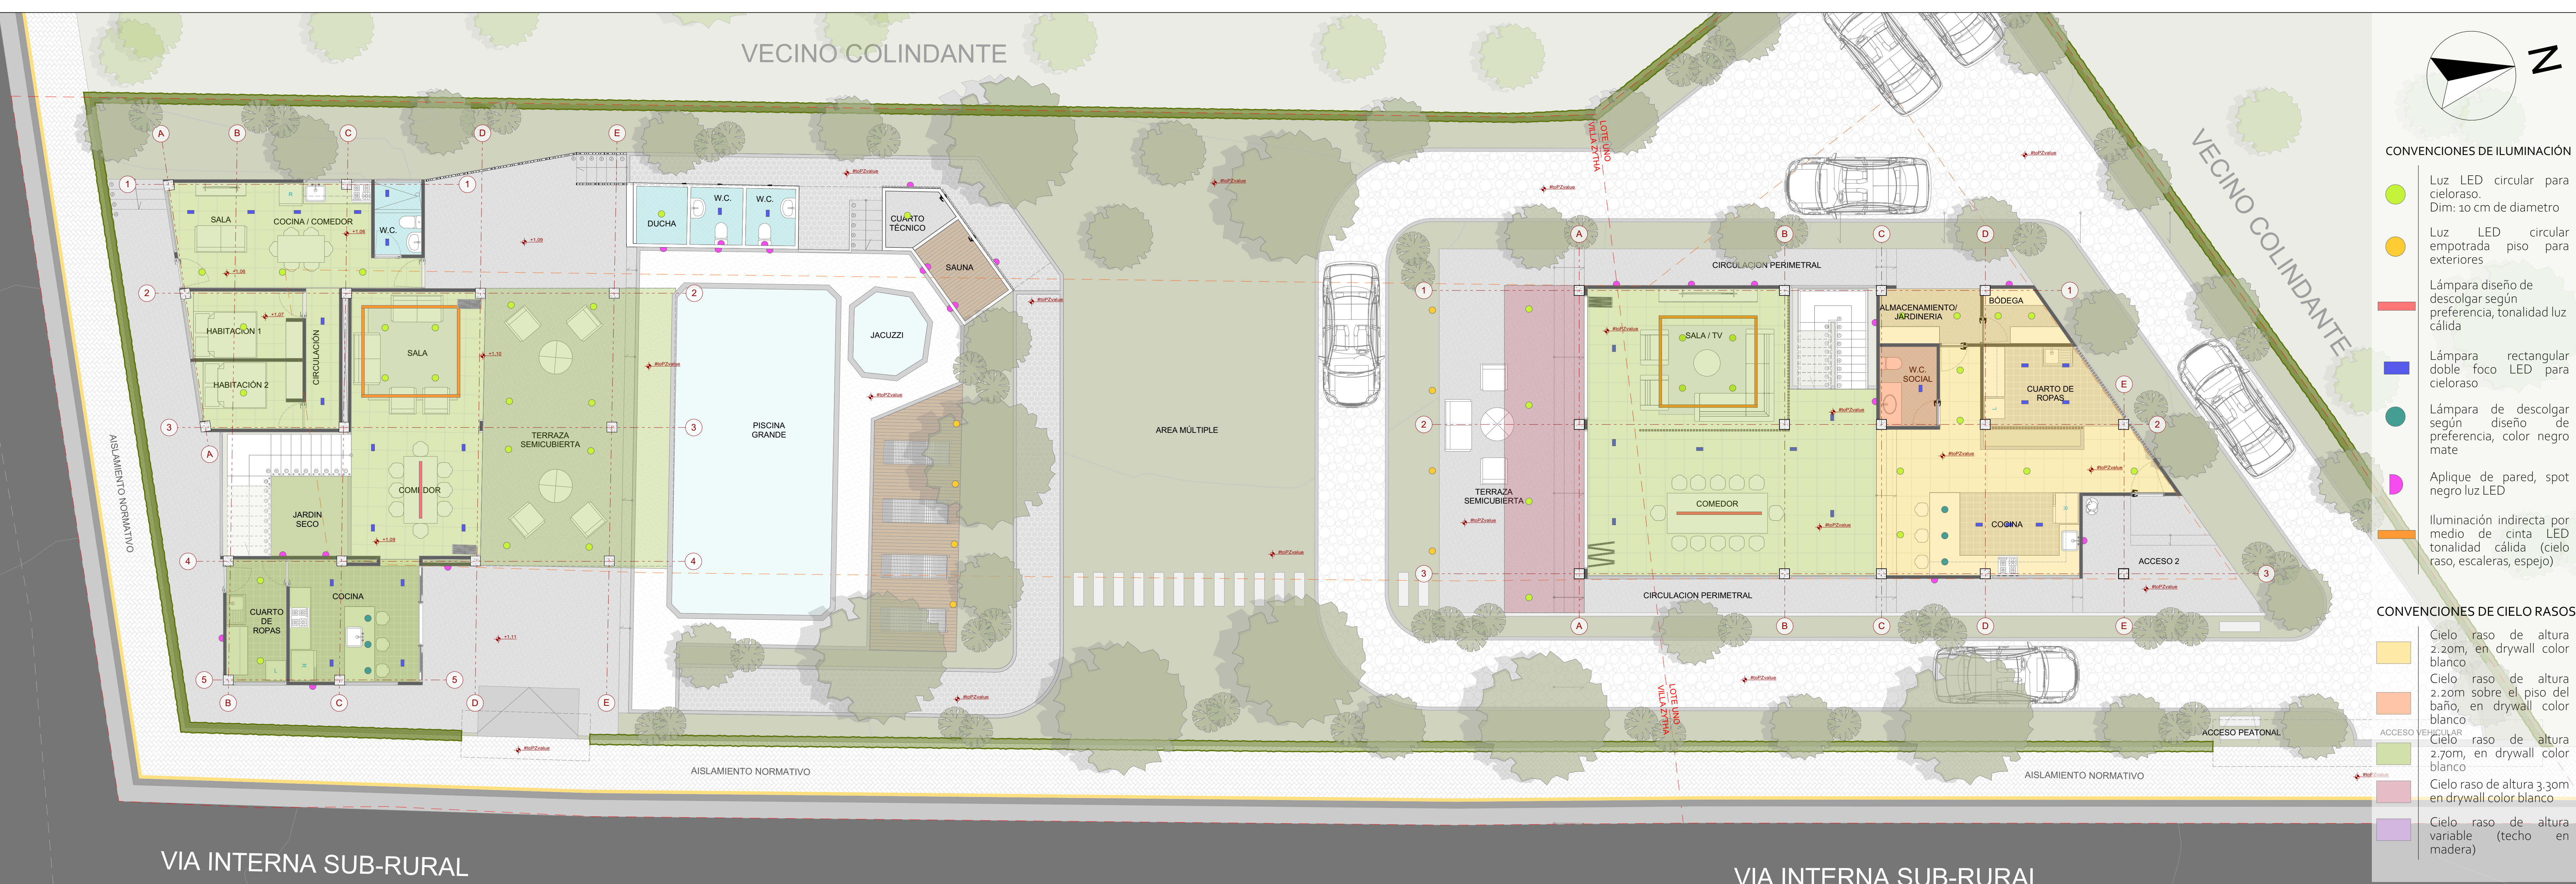

PLANO DE SEGUNDO PISO CON ILUMINACIÓN Y CIELORASTOS - PROYECTO PARCELA TOLOZA JIMENEZ

