



PLANTA ARQUITECTONICA GENERAL

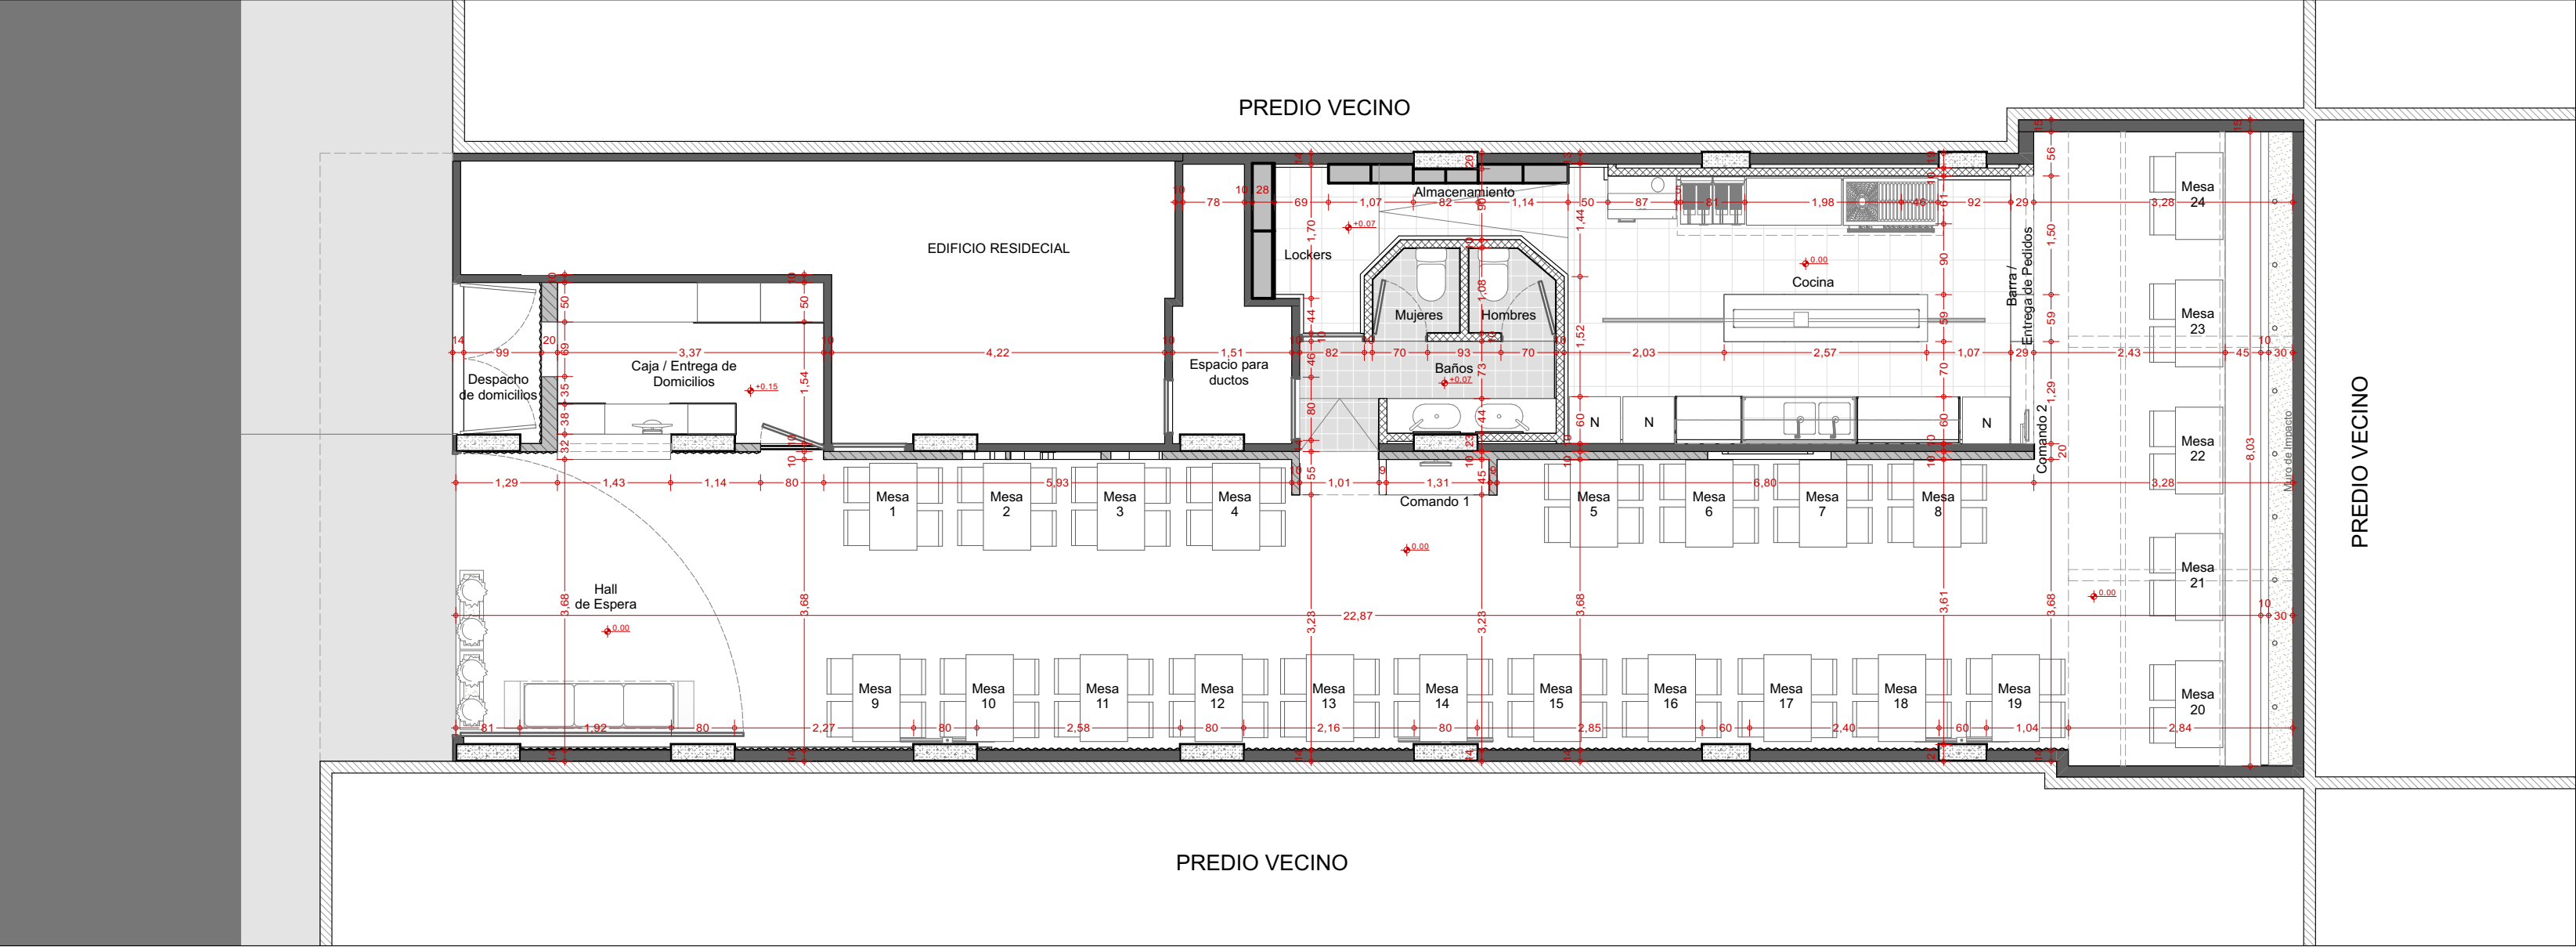

CORTE GENERAL A-A'

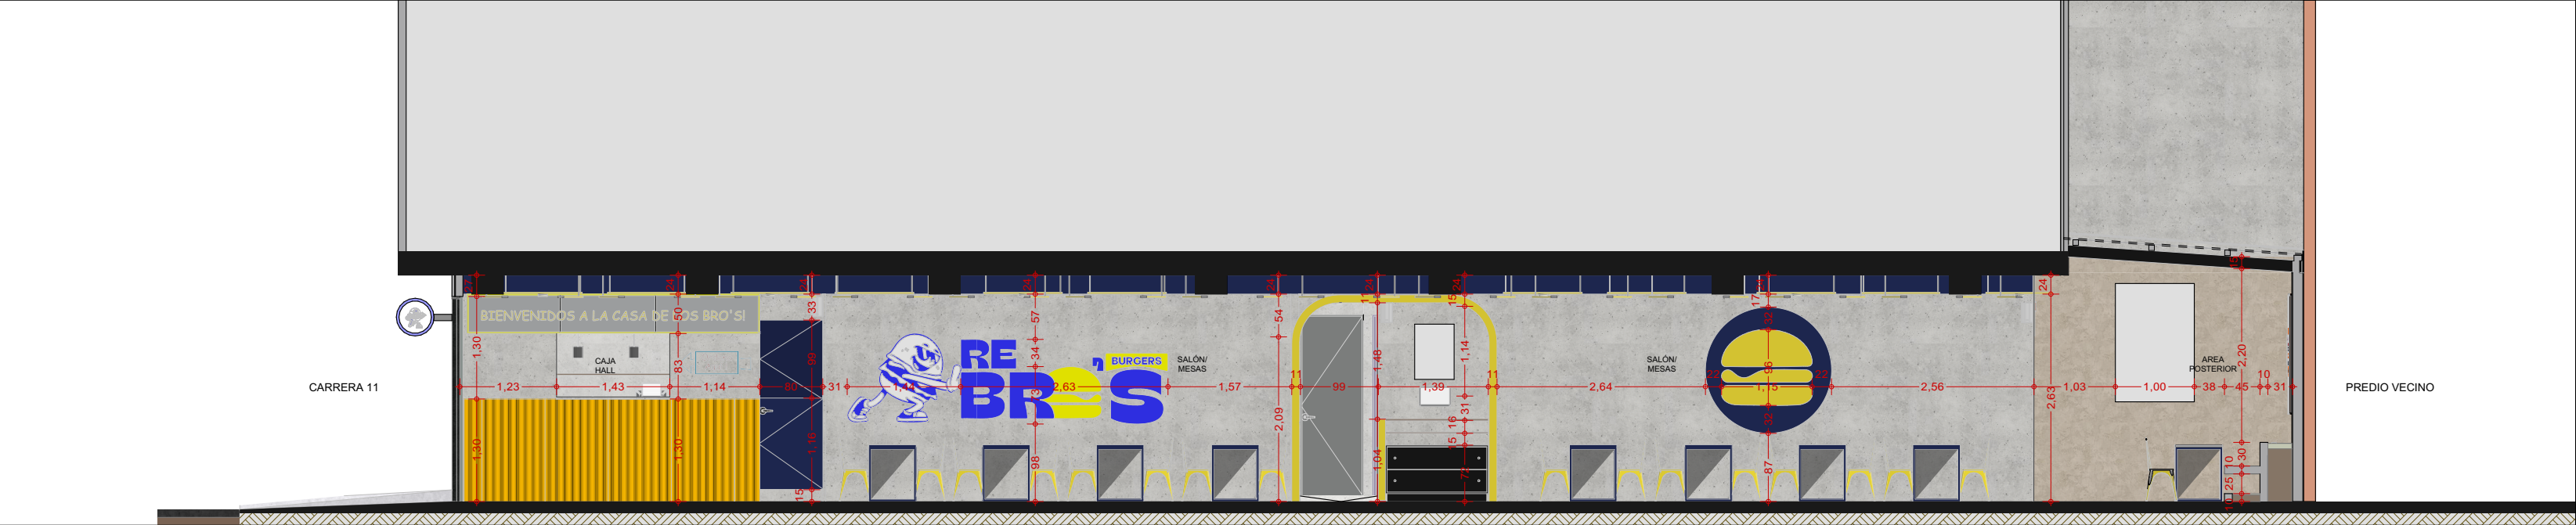

LIIT

ARQUITECTURA

LOCALIZACION

DATOS DE PREDIO

DIRECCION:

CRA 11 CON CALLE 7, FLORIDABLANCA

PROPIETARIOS

CHRISTIAN CUEVAS
ROBERT CUEVAS

DISEÑADOR

ARQ. JUAN SEBASTIAN SALAMANCA ARSLA
M.P. 330322019-1098742250

ARQ. SEBASTIAN SALAMANCA

ACTUACION

PLANIMETRIAS ARQUITECTONICAS
PROYECTO COMERCIAL - COMIDAS
RAPIDAS REBRO'S, FLORIDABLANCA

CONTENIDO

-PLANTA ARQUITECTONICA GENERAL

-CORTE GENERAL A-A'

NOTAS GENERALES

ESCALAS

1:75

15/01/2026

PLANO 1 DE 6