



PROYECTO COMERCIAL - COMIDAS RAPIDAS RE BRO'S, FLORIDABLANCA

CORTE B-B'

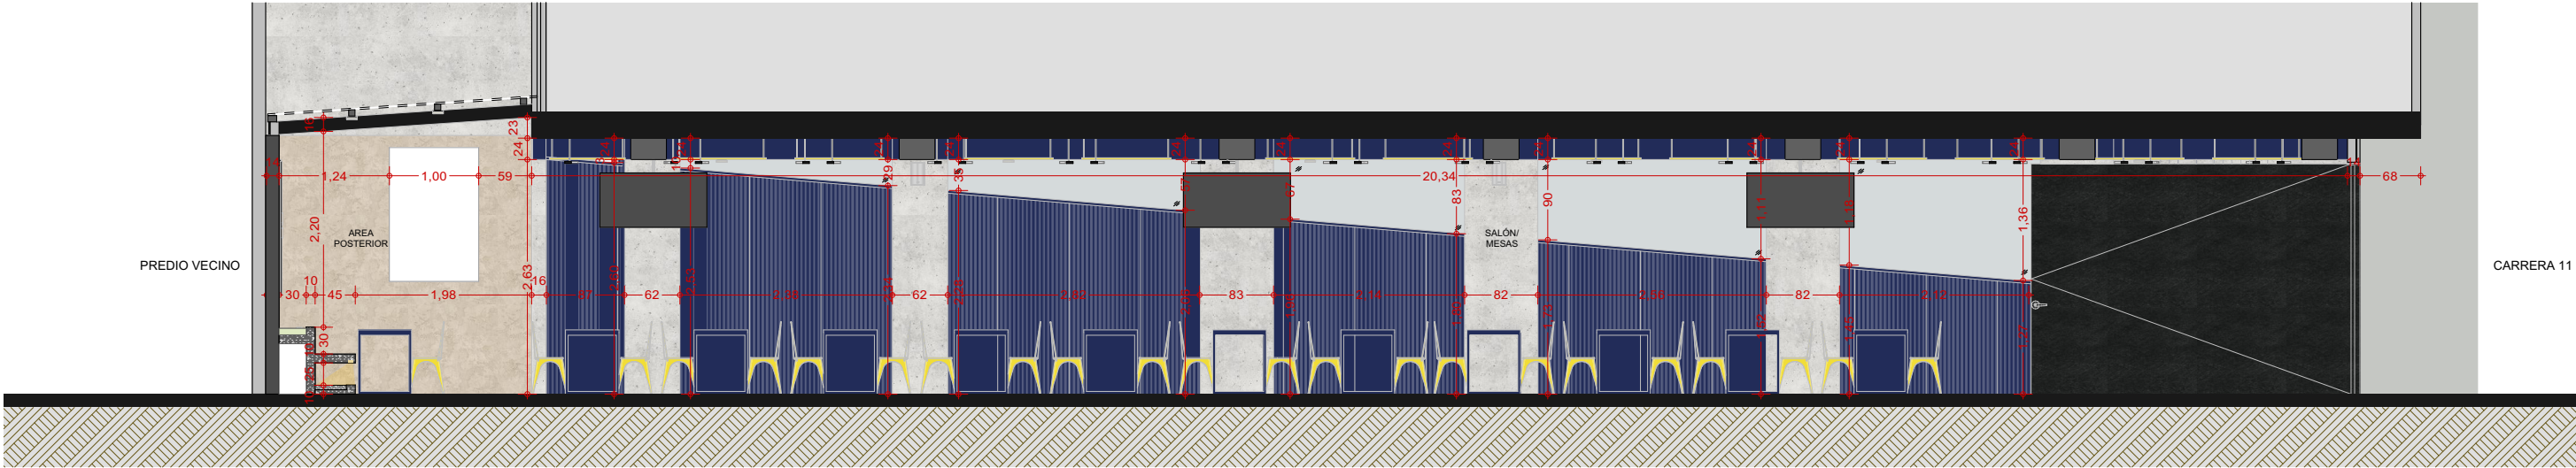


CORTE C-C'

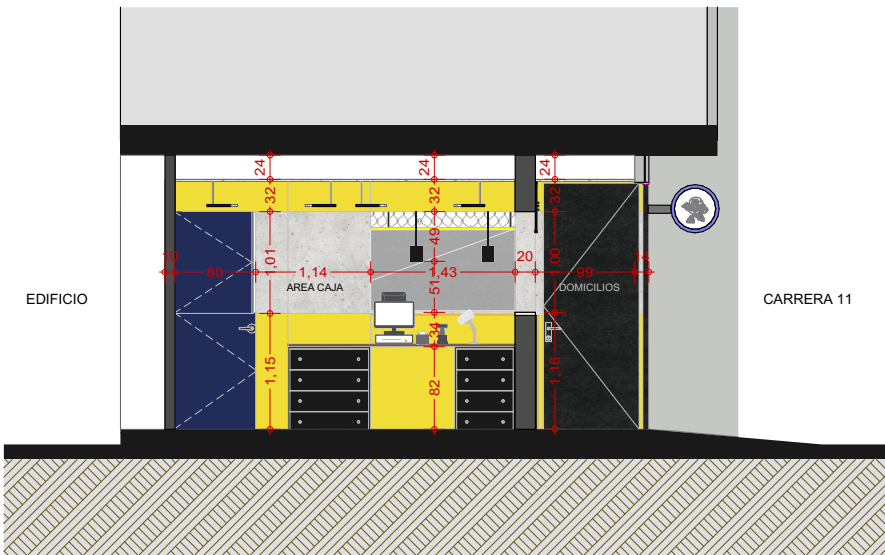


CORTE D-D'



CORTE E-E'

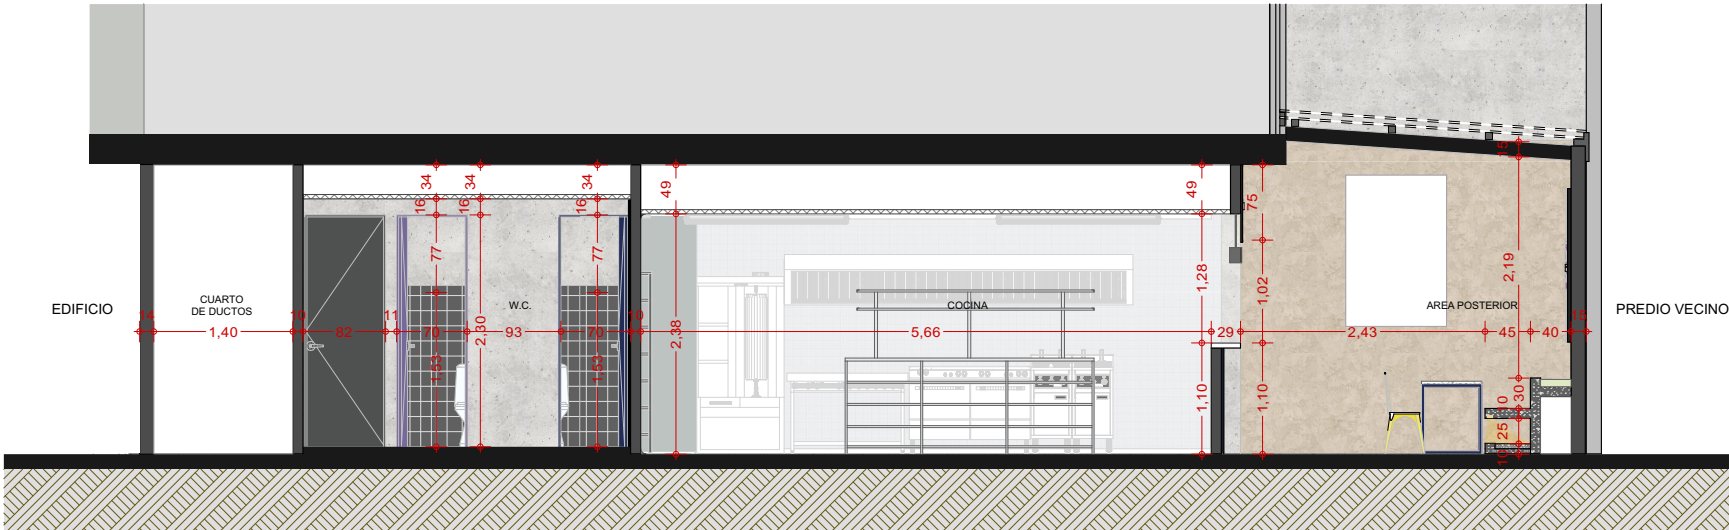

CORTE F-F'

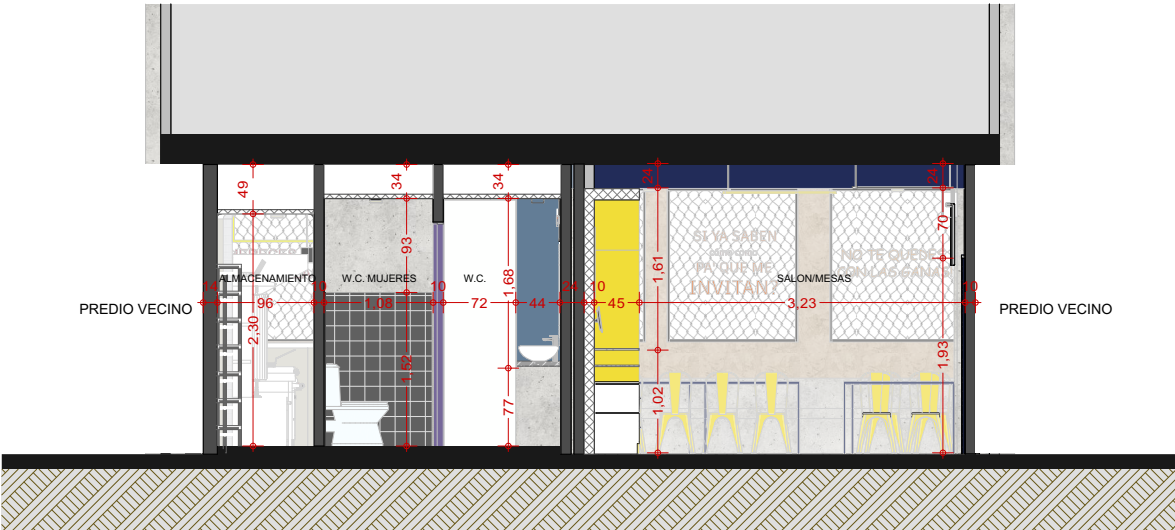

LIIT ARQUITECTURA

LOCALIZACION



DATOS DE PREDIO

DIRECCION:
CRA 11 CON CALLE 7, FLORIDABLANCA

PROPIETARIOS

CHRISTIAN CUEVAS
ROBERT CUEVAS

DISEÑADOR

ARQ. JUAN SEBASTIAN SALAMANCA ARSLA
M.P. 330322019-1098742250
ARQ. SEBASTIAN SALAMANCA

ACTUACION

PLANIMETRIAS ARQUITECTONICAS
PROYECTO COMERCIAL - COMIDAS
RAPIDAS REBRO'S, FLORIDABLANCA

CONTENIDO

- CORTE GENERAL B-B'
- CORTE GENERAL C-C'
- CORTE GENERAL D-D'
- CORTE GENERAL E-E'
- CORTE GENERAL F-F'

NOTAS GENERALES

ESCALAS

1:75

15/01/2026