



PROYECTO COMERCIAL - COMIDAS RAPIDAS RE BRO'S, FLORIDABLANCA

PLANO GENERAL CON PUNTOS DE INSTALACIONES Y PUERTAS

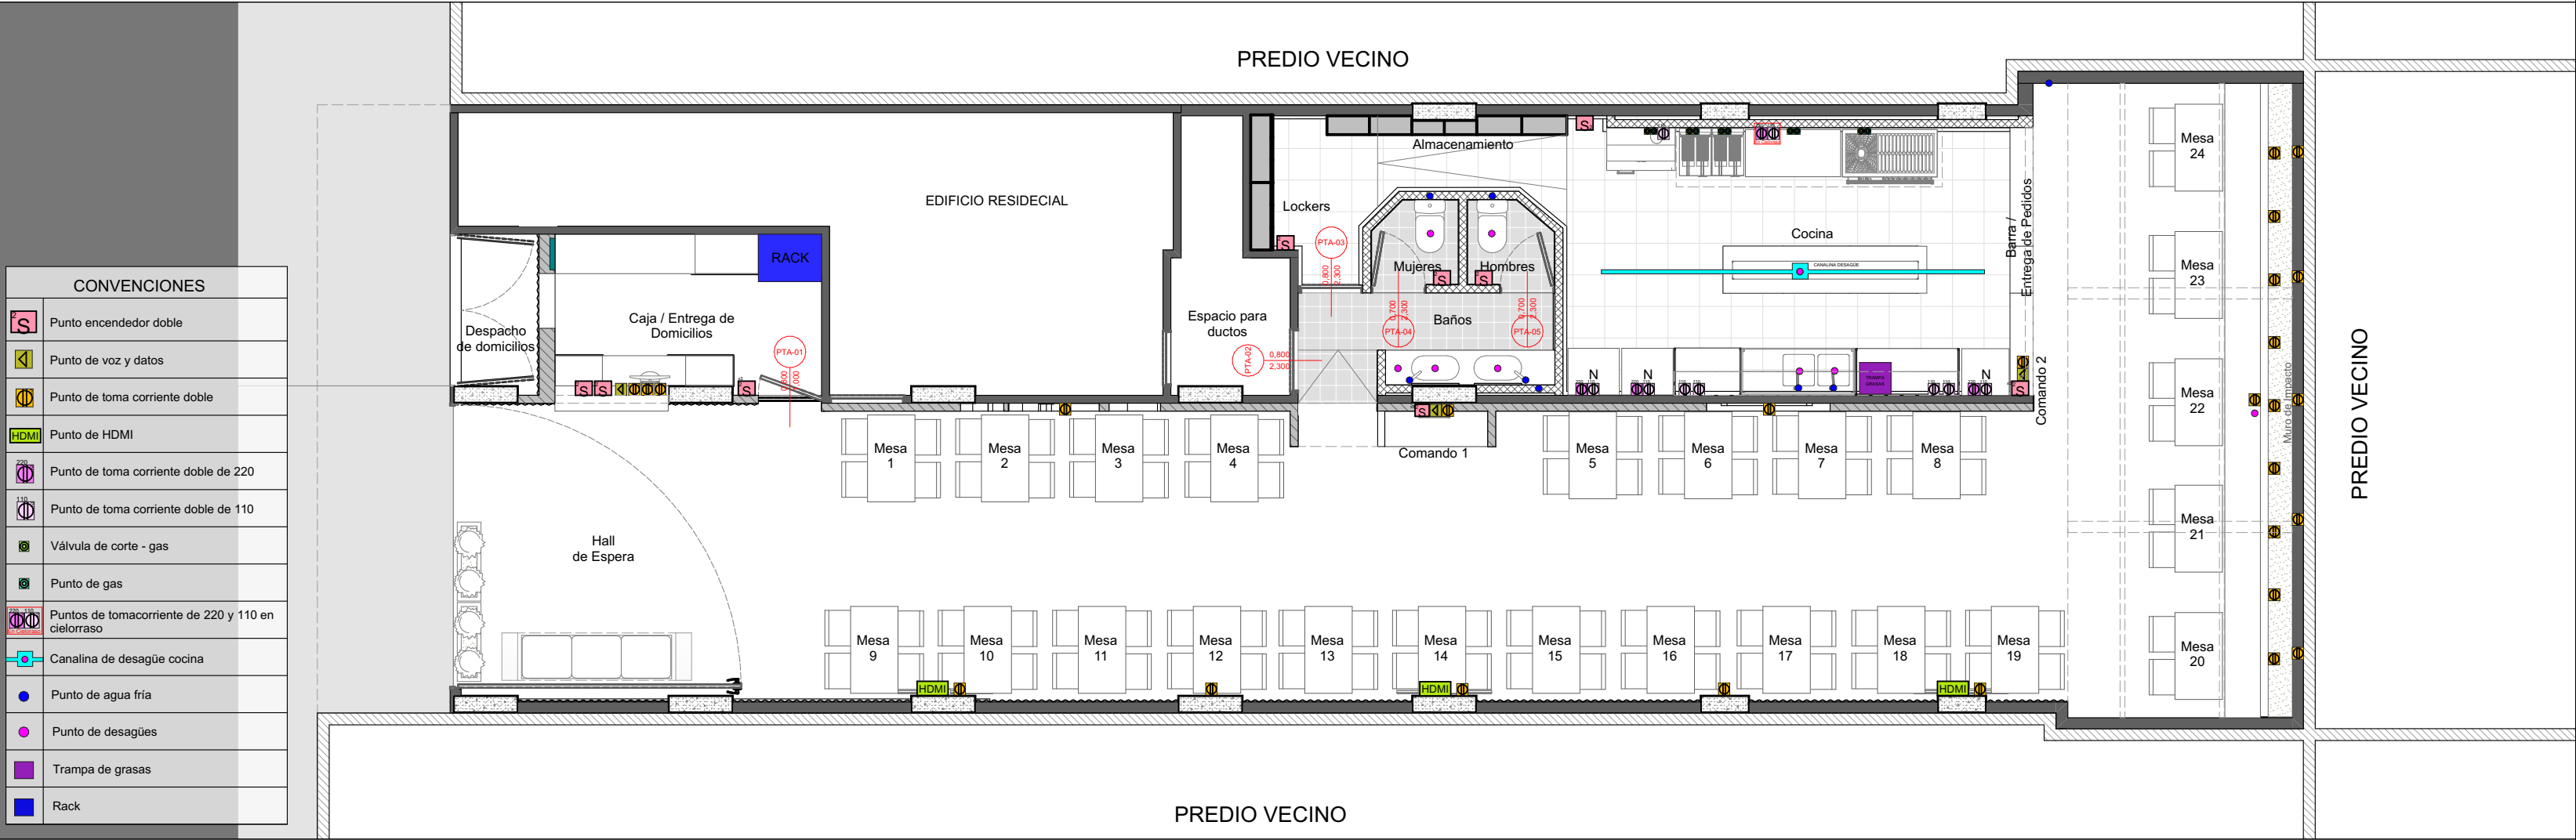

PLANO GENERAL DE CIELORASO E ILUMINACION

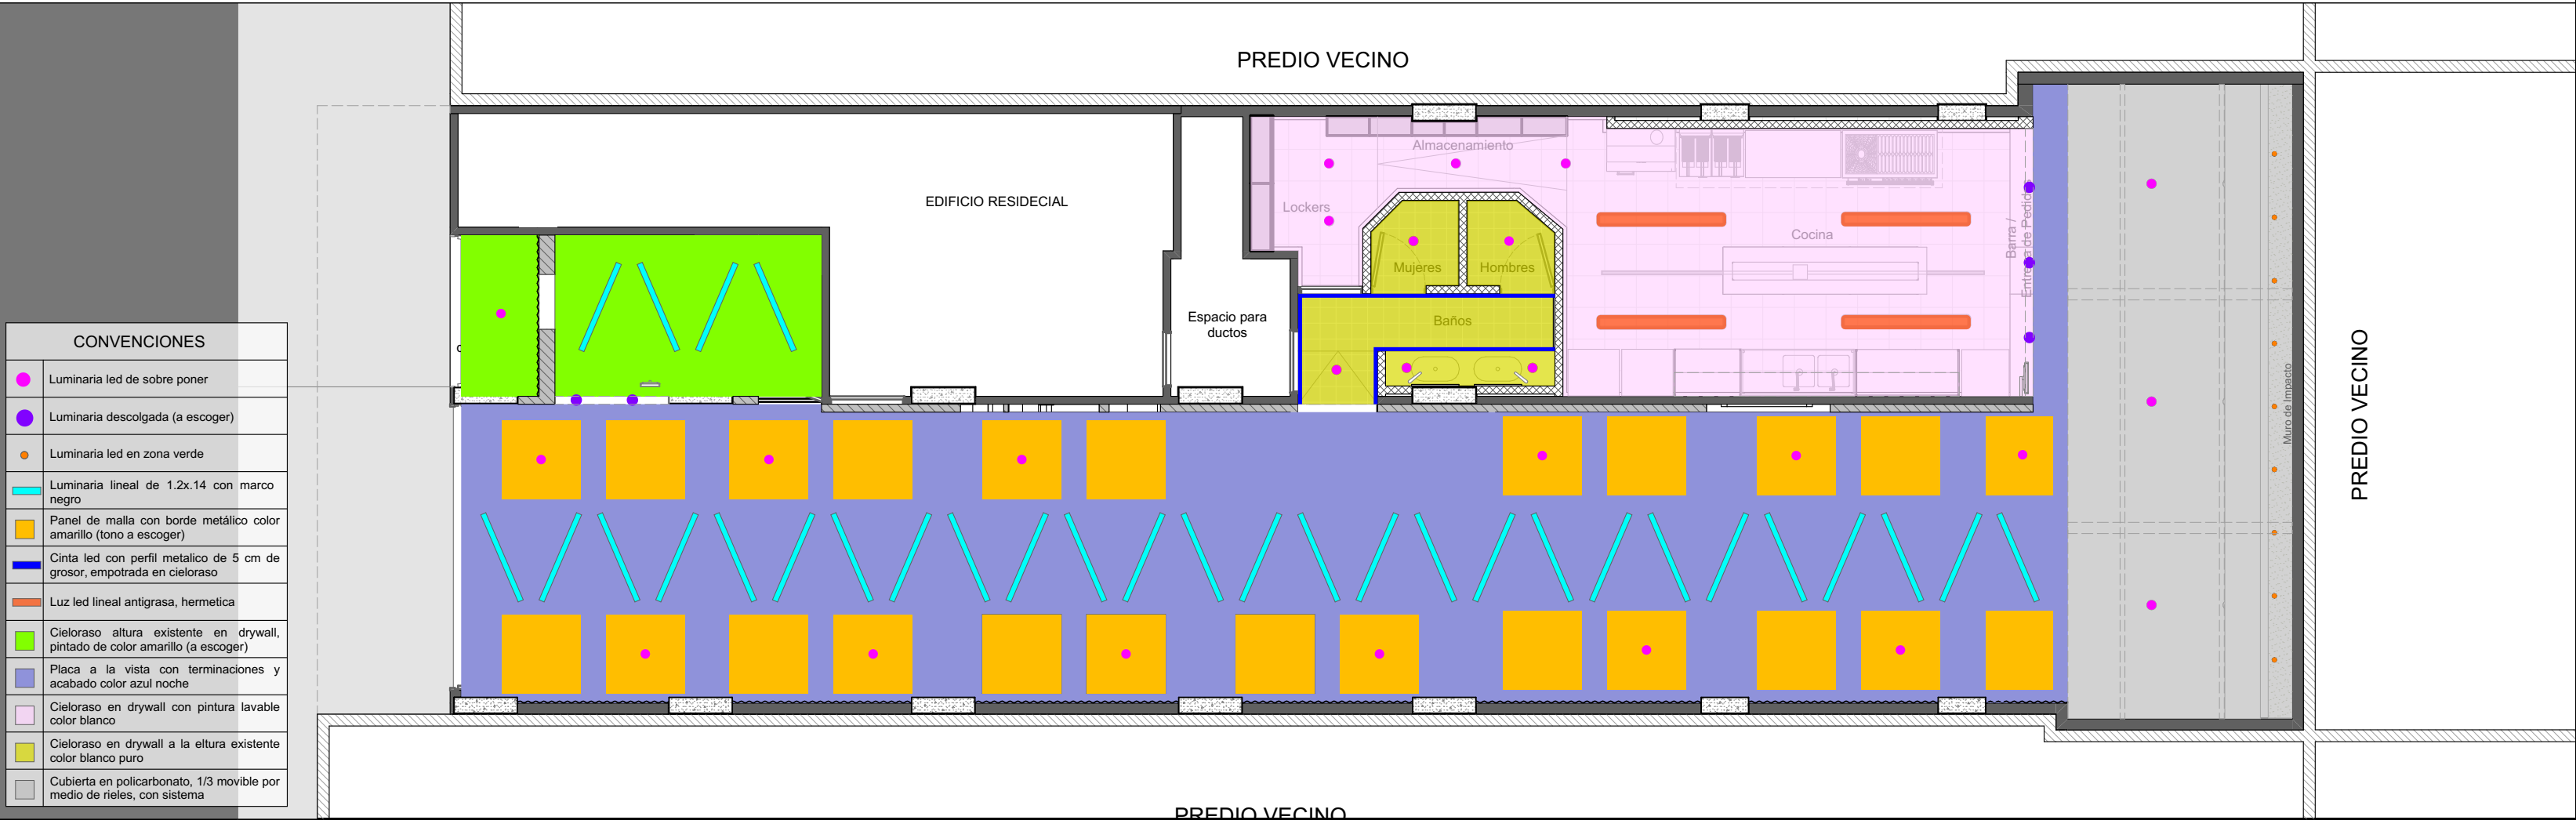

LIIT ARQUITECTURA

LOCALIZACION



DATOS DE PREDIO

DIRECCION:
CRA 11 CON CALLE 7, FLORIDABLANCA

PROPIETARIOS

CHRISTIAN CUEVAS
ROBERT CUEVAS

DISEÑADOR

ARQ. SEBASTIAN SALAMANCA
M.P. 330322-19-1098742250

ACTUACION

PLANIMETRIAS ARQUITECTONICAS
PROYECTO COMERCIAL - COMIDAS
RAPIDAS REBRO'S, FLORIDABLANCA

CONTENIDO

- PLANO DE PUNTOS DE
INSTALACIONES
- PLANO DE CIELORASOS E
ILUMINACION

NOTAS GENERALES

ESCALAS
1:75

15/01/2026

PLANO 4 DE 6