



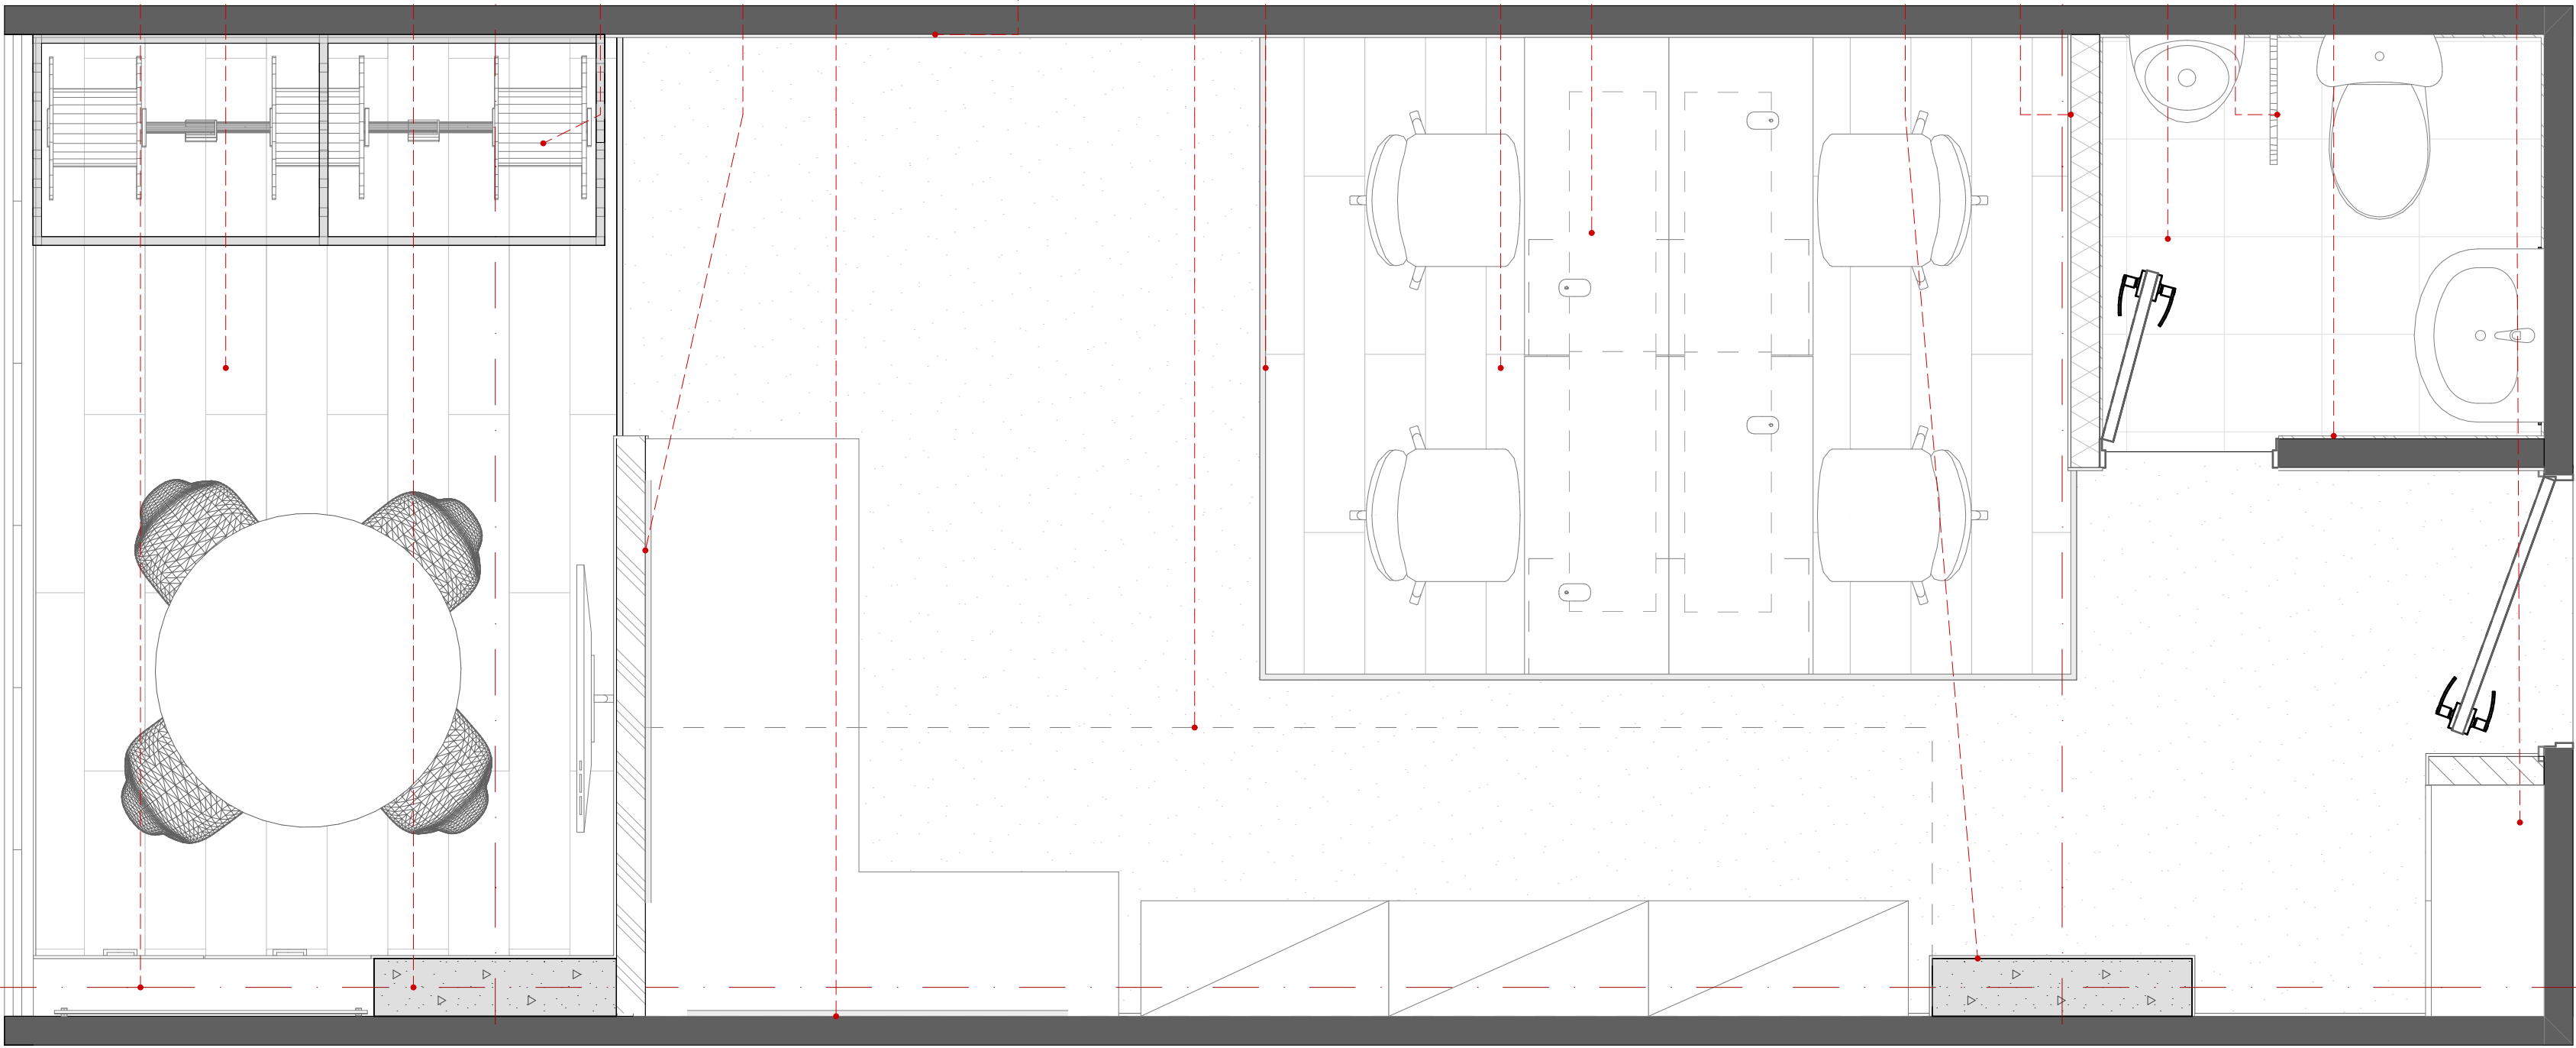

PLANTA DE ACABADOS Y ESPECIFICACIONES / CORTE B-B'

ESCALA 1:20

- Mobiliario con tablero en vidrio sobre pared
- Acabado de Piso laminado tipo madera
- Columna existente con acabado de pintura azul institucional
- Estantería paneles solares y cableado
- Muro en drywall reforzado con acabado en pintura Gris Grafito
- Muro existente en acabado en pintura Gris Grafito y Panel
- Señalografía con logo institucional
- Lamina en superboard anclada con tornillo autoperforante
- Dilatador en aluminio
- Acabado de Piso laminado tipo madera
- Adaptación de puestos de trabajo existentes junto con caleneras
- Columna existente con acabado de pintura azul institucional
- Muro en superboard con acabado de pintura Gris Grafito y Cerámica en zona del baño
- Acabado cerámica para pared y piso en baño, formato 30 x 60 cm
- División de baño en acero inoxidable
- Acabado cerámica para pared y piso estilo coco blanco formato 30 x 60 cm
- Muro en drywall con mueble en madera / solo puertas

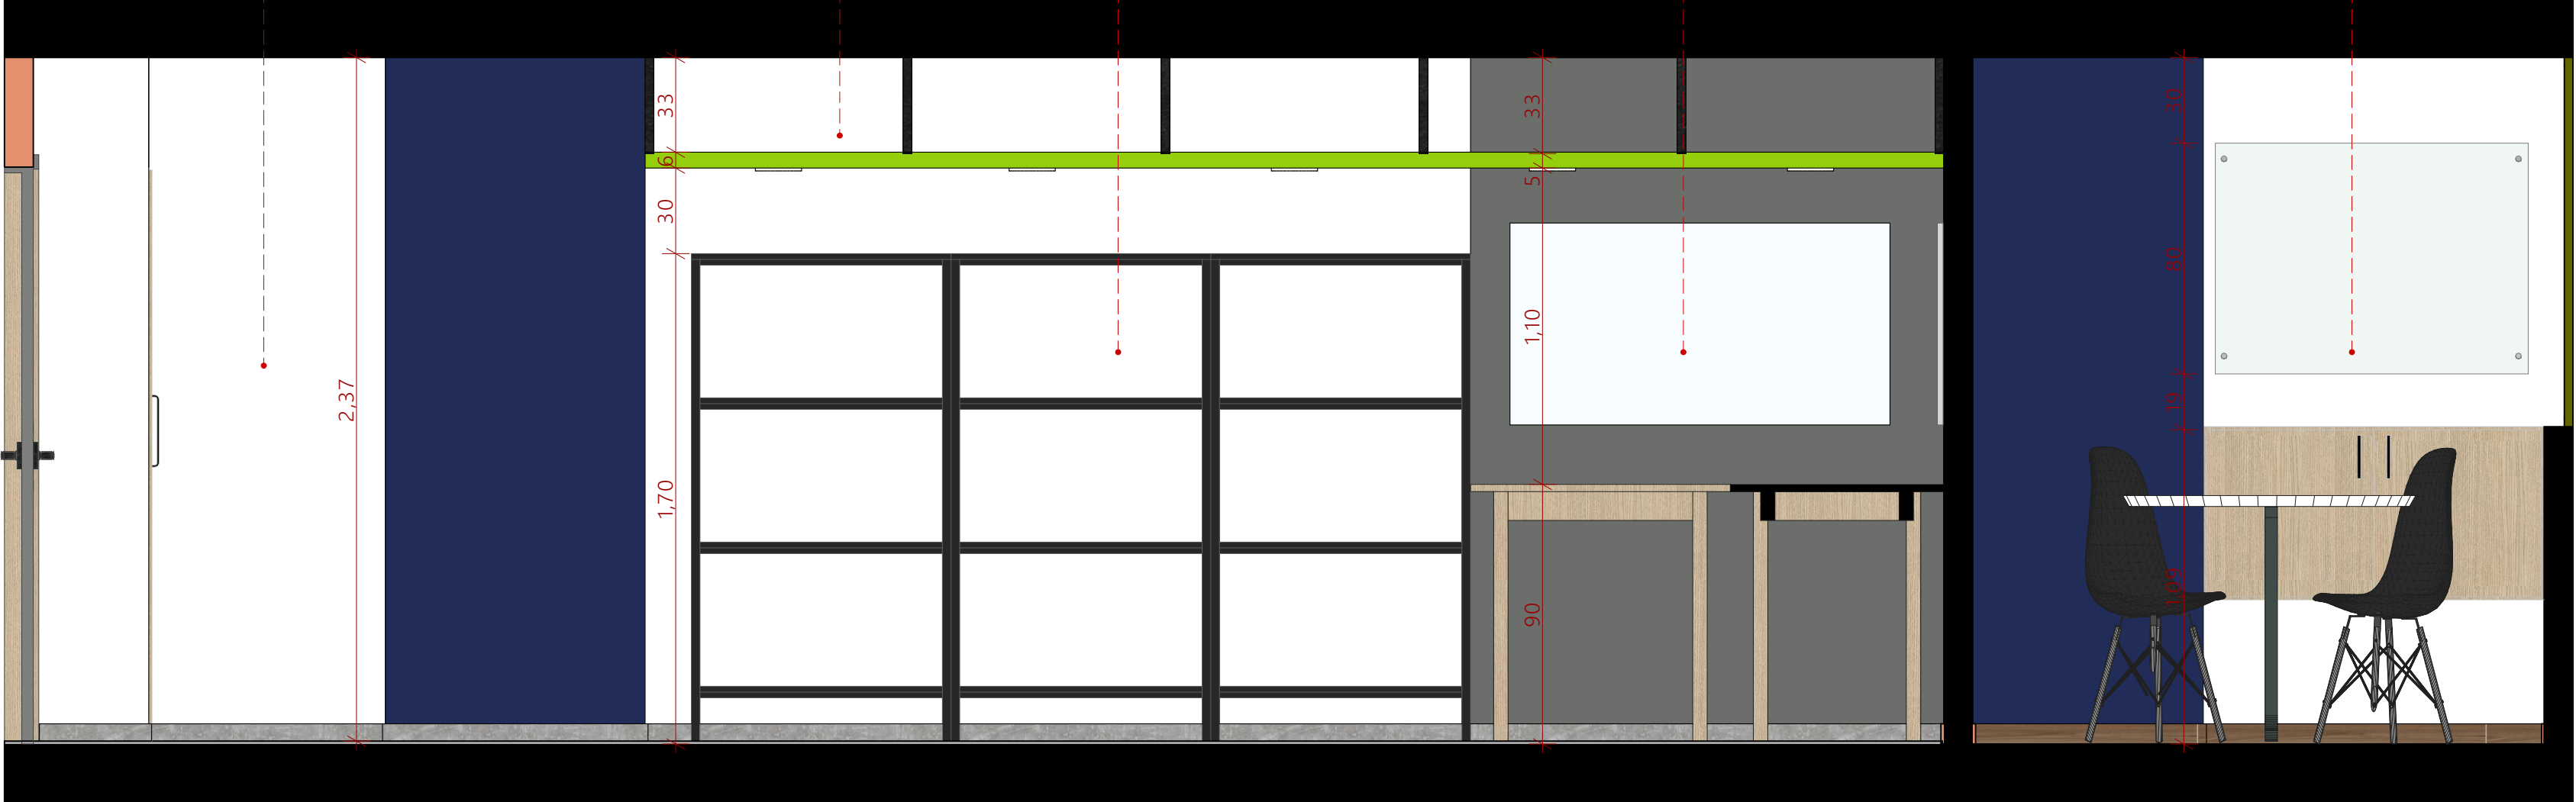